PHASE : A.P.S

Date : 16/01/2026 23:42:10

POLYCONCEPT GROUP

INTERNAT AS SALAM

AS SALAM

36 Mr AHMADOU KABA	VUE 1 Echelle:	**INTERNAT AS SALAM**	**_ RDC + 2 ETAGES + TERRASSE** **TAMBA**_ MISSIRAH	**A-001**

BY ING MOUSSA
TEL:+221 77 231 96 53
mail: moussac1994.1@gmail.com



PHASE : A.P.S

Date : 16/01/2026 23:42:11

POLYCONCEPT GROUP

Mr AHMADOU KABA

VUE 2

Echelle:

INTERNAT AS SALAM

_ RDC + 2 ETAGES + TERRASSE

TAMBA_ MISSIRAH

A-002

BY ING MOUSSA
TEL:+221 77 231 96 53
mail: moussac1994.1@gmail.com

PHASE : A.P.S


Date : 16/01/2026 23:42:11

POLYCONCEPT GROUP



Mr AHMADOU KABA	VUE 3 Echelle:	**INTERNAT AS SALAM**	**_ RDC + 2 ETAGES + TERRASSE** **TAMBA**_ MISSIRAH	**A-003**

BY ING MOUSSA
TEL:+221 77 231 96 53
mail: moussac1994.1@gmail.com

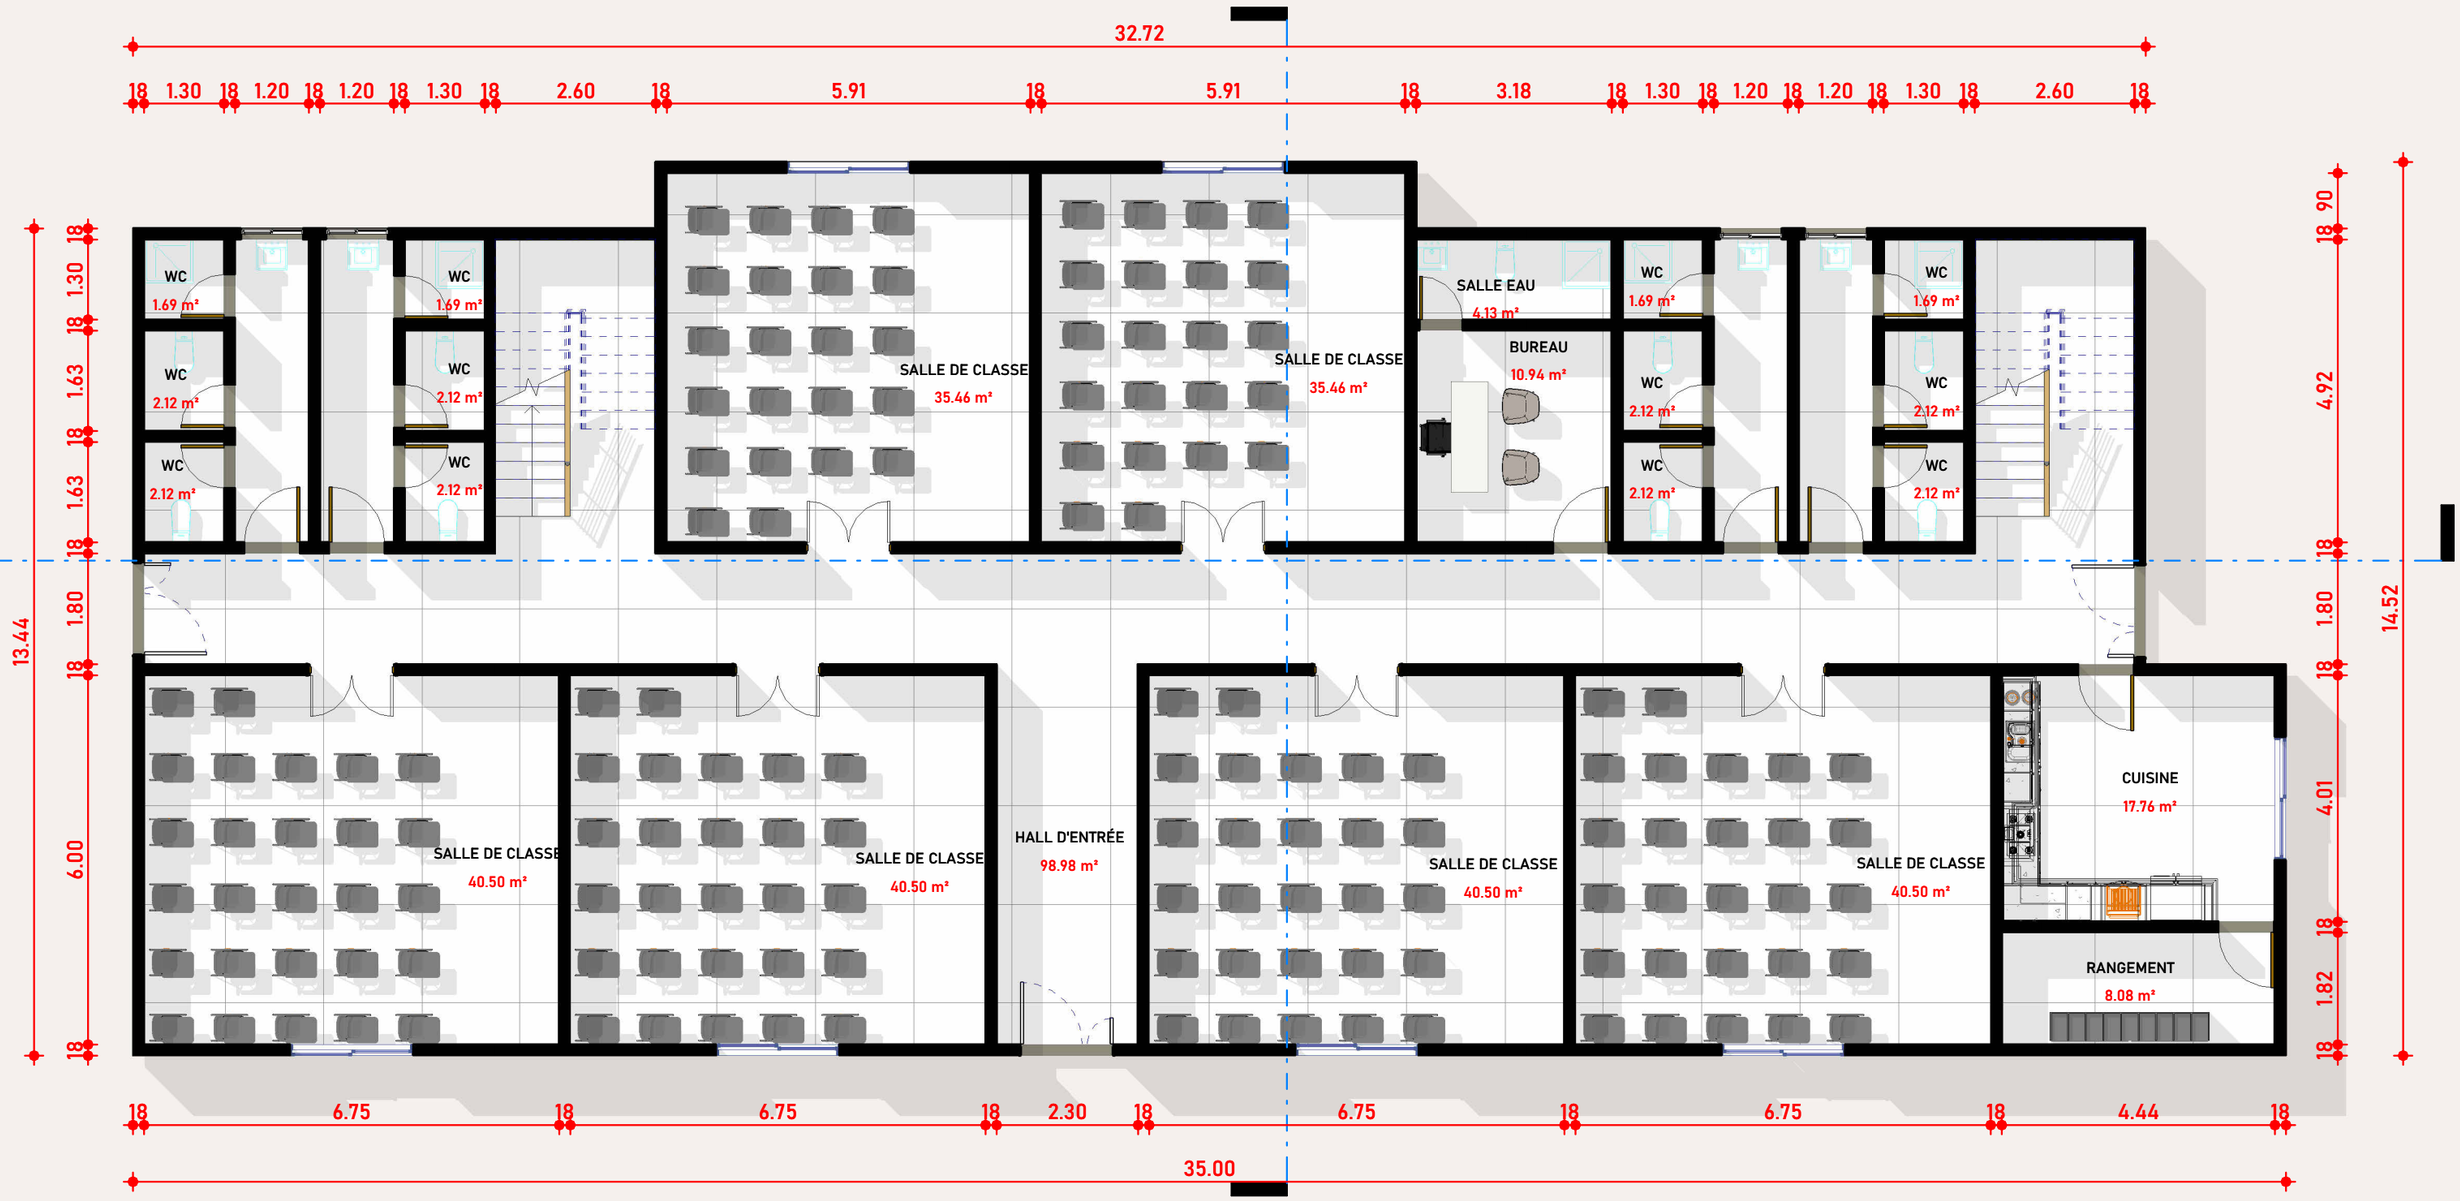


BY ING MOUSSA
TEL:+221 77 231 96 53
mail: polyconceptgroup@gmail.com



36 Mr AHMADOU KABA	ETAGE 1 Echelle: **1 : 100**	**INTERNAT AS SALAM**	**_ RDC + 2 ETAGES + TERRASSE** **TAMBA**_ MISSIRAH	**A-103**

BY ING MOUSSA
TEL:+221 77 231 96 53
mail: moussac1994.1@gmail.com

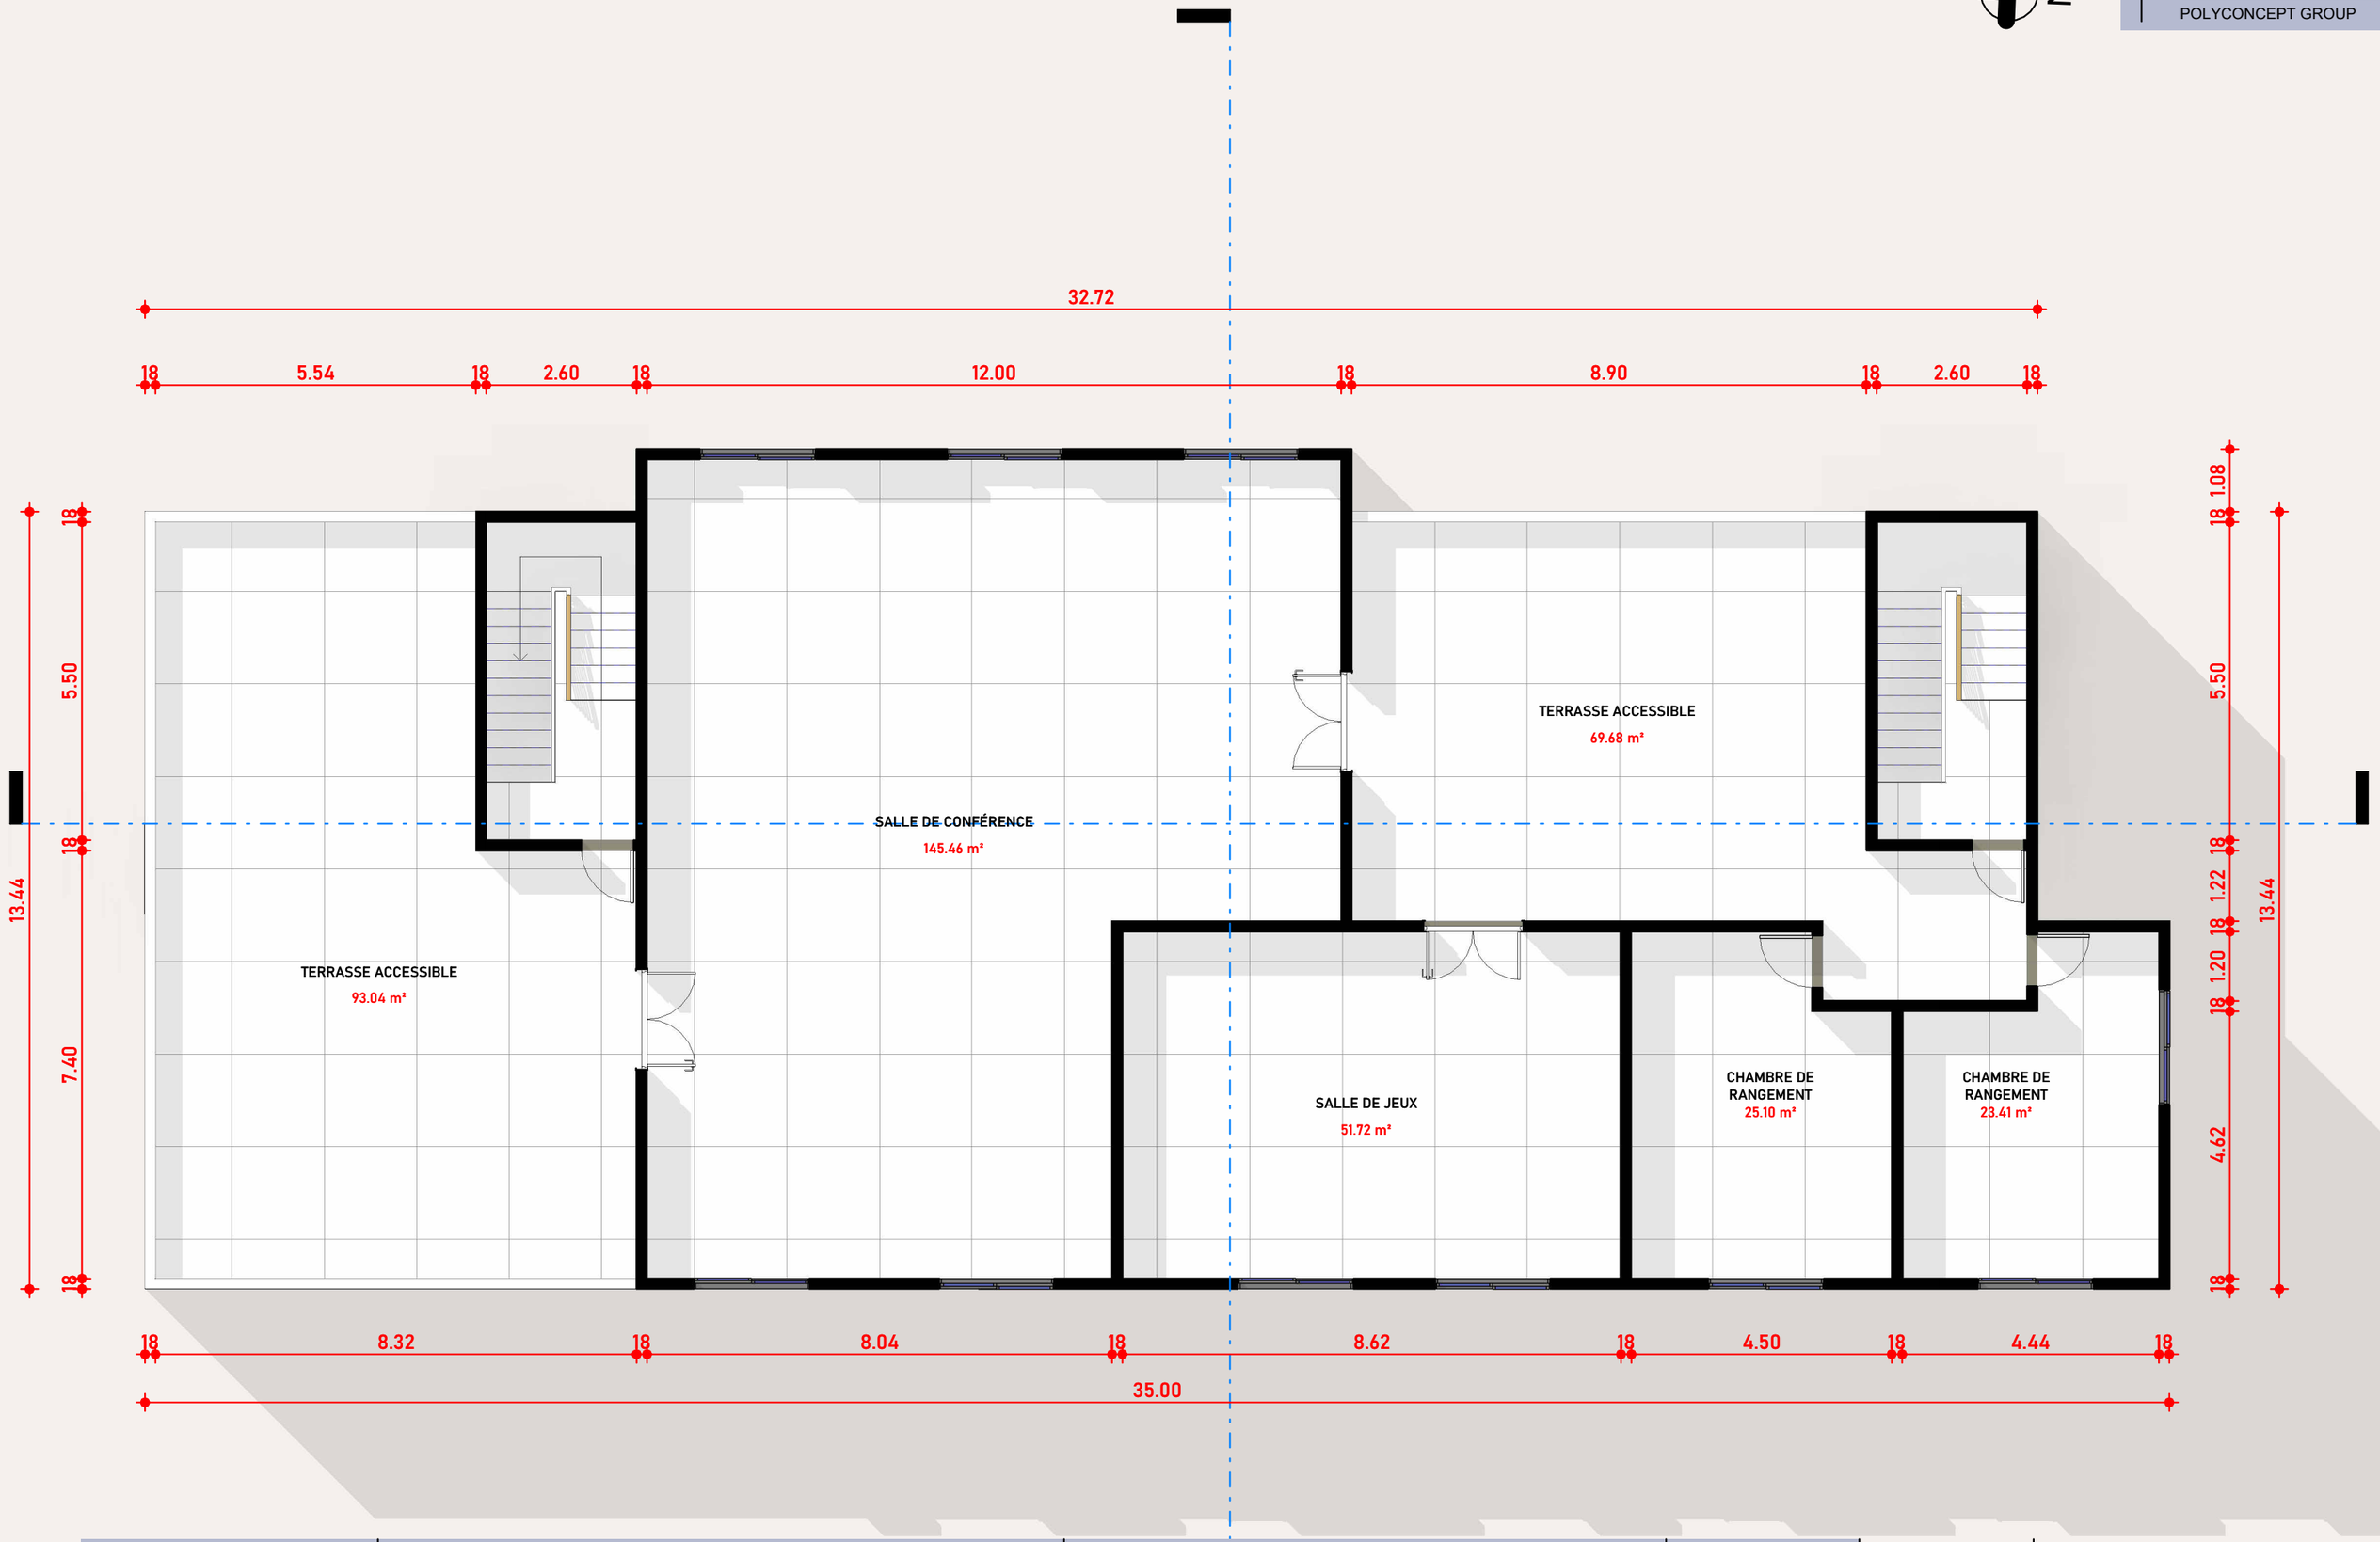

Mr AHMADOU KABA

ETAGE 2

Echelle: **1 : 100**

INTERNAT AS SALAM

_ RDC + 2 ETAGES + TERRASSE

TAMBA_ MISSIRAH


A-104

BY ING MOUSSA
TEL:+221 77 231 96 53
mail: moussac1994.1@gmail.com

PHASE : A.P.S

Date : 16/01/2026 23:42:33

POLYCONCEPT GROUP

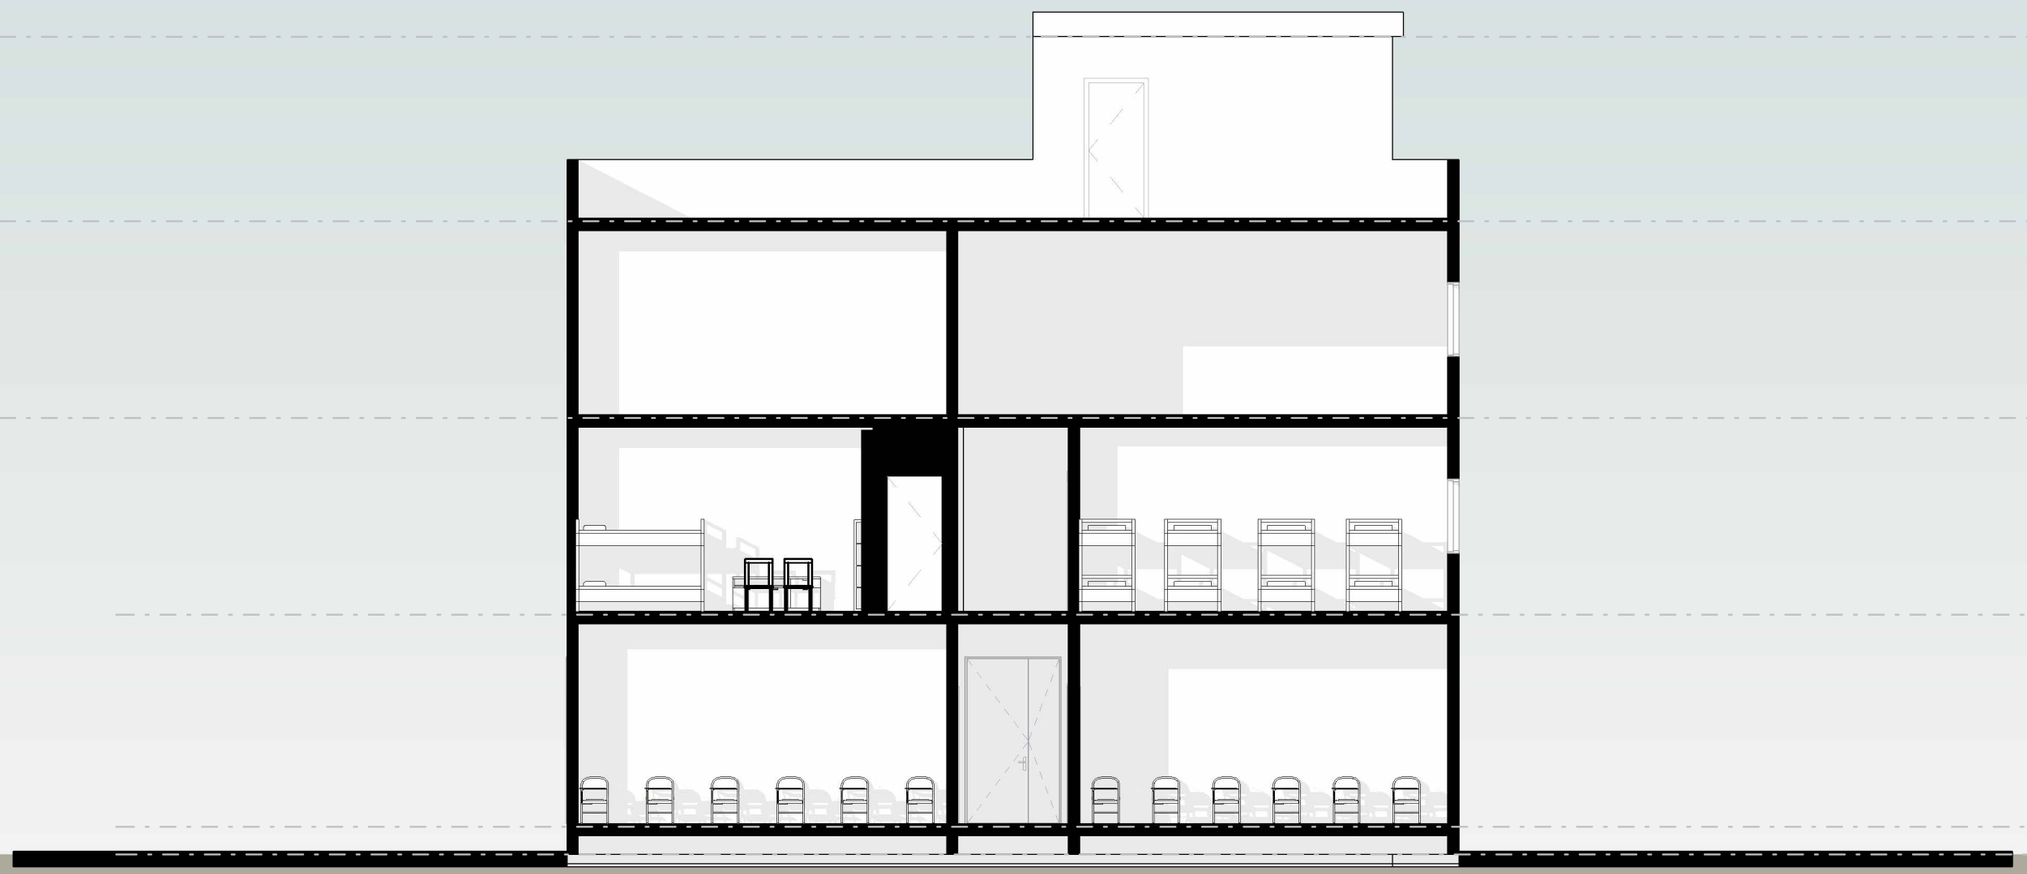

36 **Mr AHMADOU KABA**

COUPE A-A

Echelle: **1 : 100**

INTERNAT AS SALAM

_ RDC + 2 ETAGES + TERRASSE

TAMBA_ MISSIRAH


A-105

BY ING MOUSSA
TEL:+221 77 231 96 53
mail: moussac1994.1@gmail.com

PHASE : A.P.S

Date : 16/01/2026 23:42:35

POLYCONCEPT GROUP

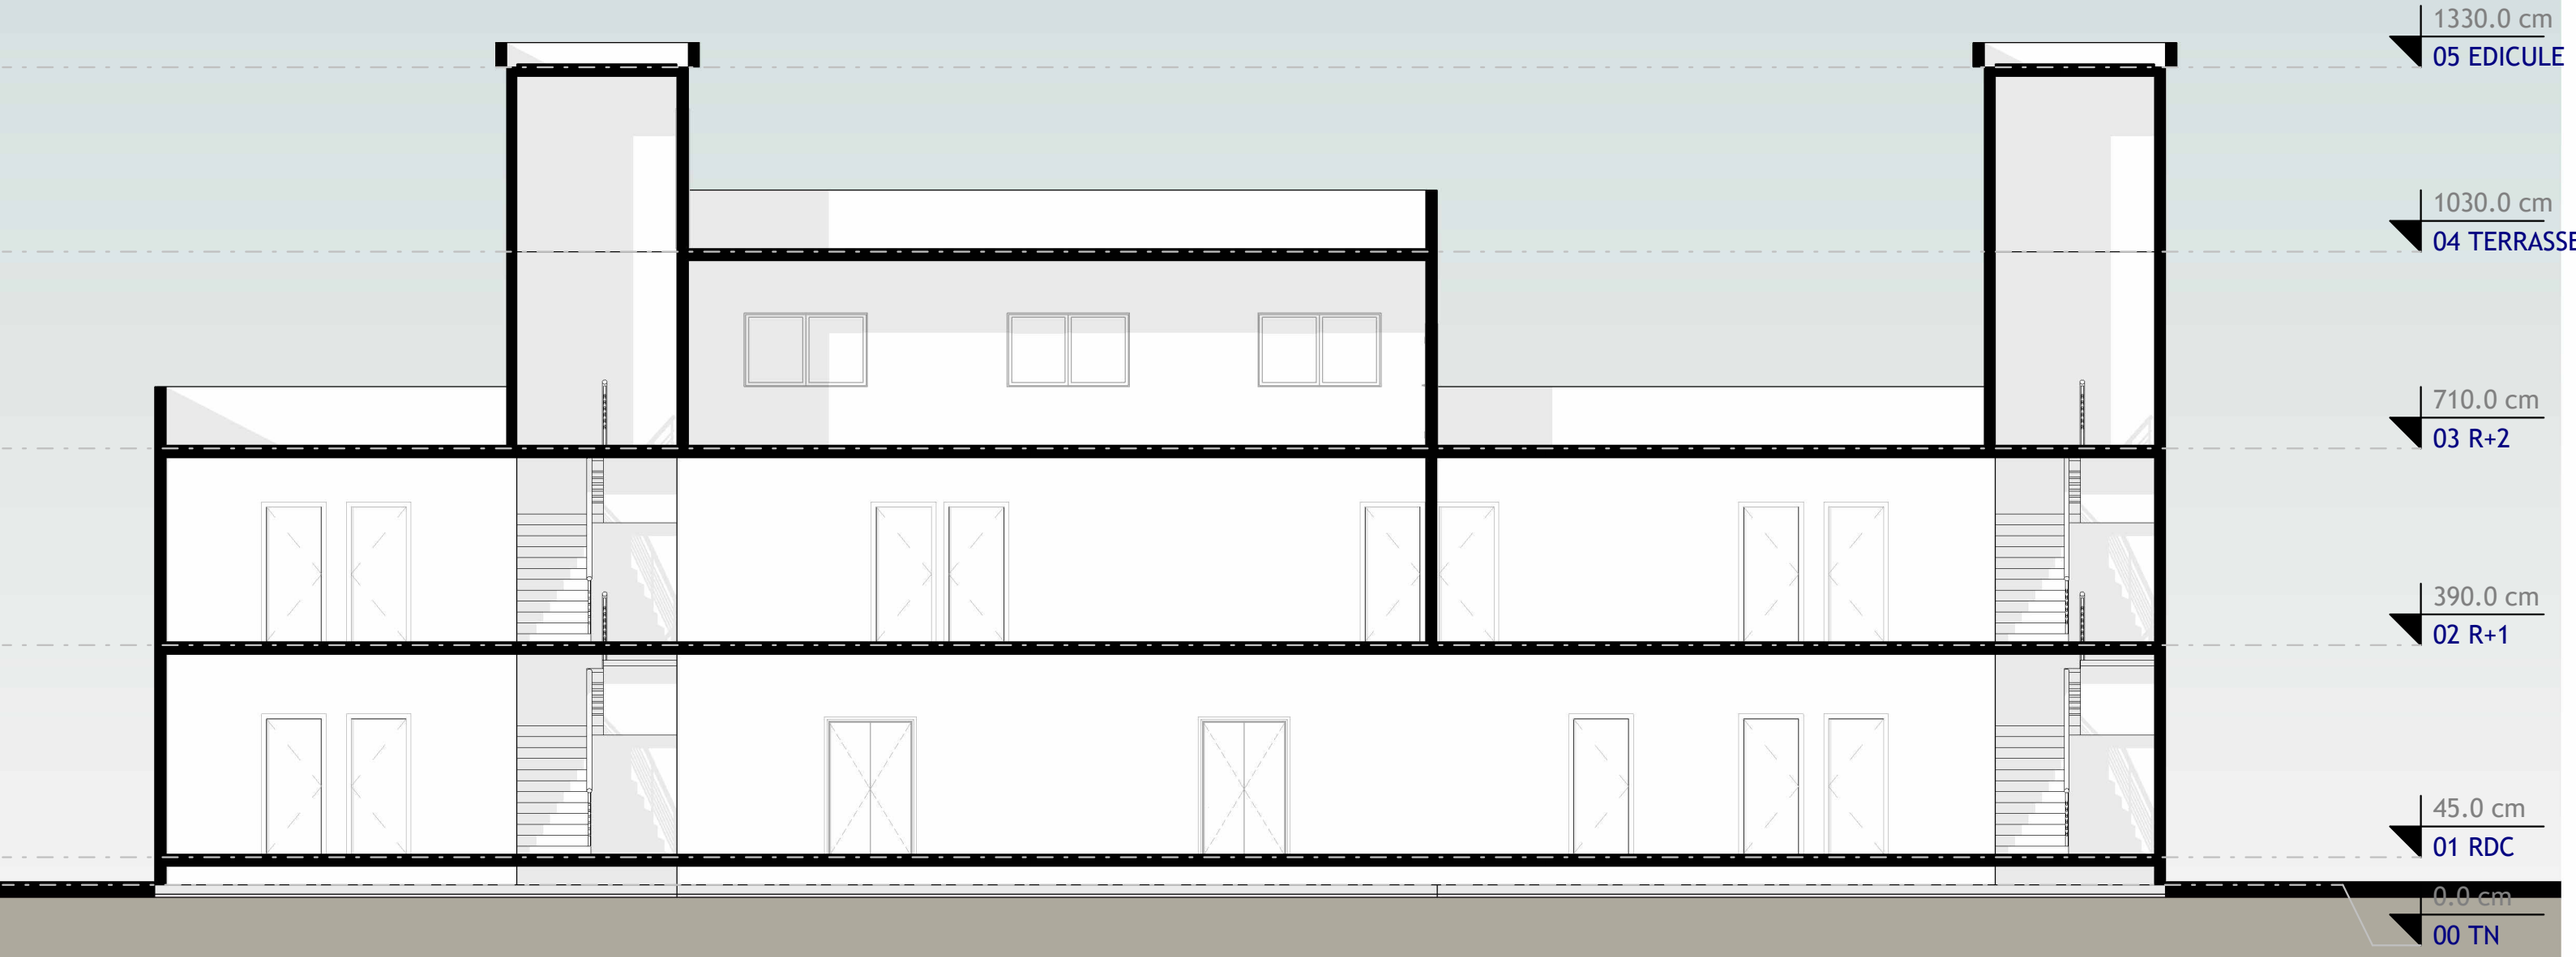

36 **Mr AHMADOU KABA**

COUPE B-B

Echelle: **1 : 100**

INTERNAT AS SALAM

_ RDC + 2 ETAGES + TERRASSE

TAMBA_ MISSIRAH


A-106

BY ING MOUSSA
TEL:+221 77 231 96 53
mail: moussac1994.1@gmail.com

PHASE : A.P.S

Date : 16/01/2026 23:42:39

POLYCONCEPT GROUP

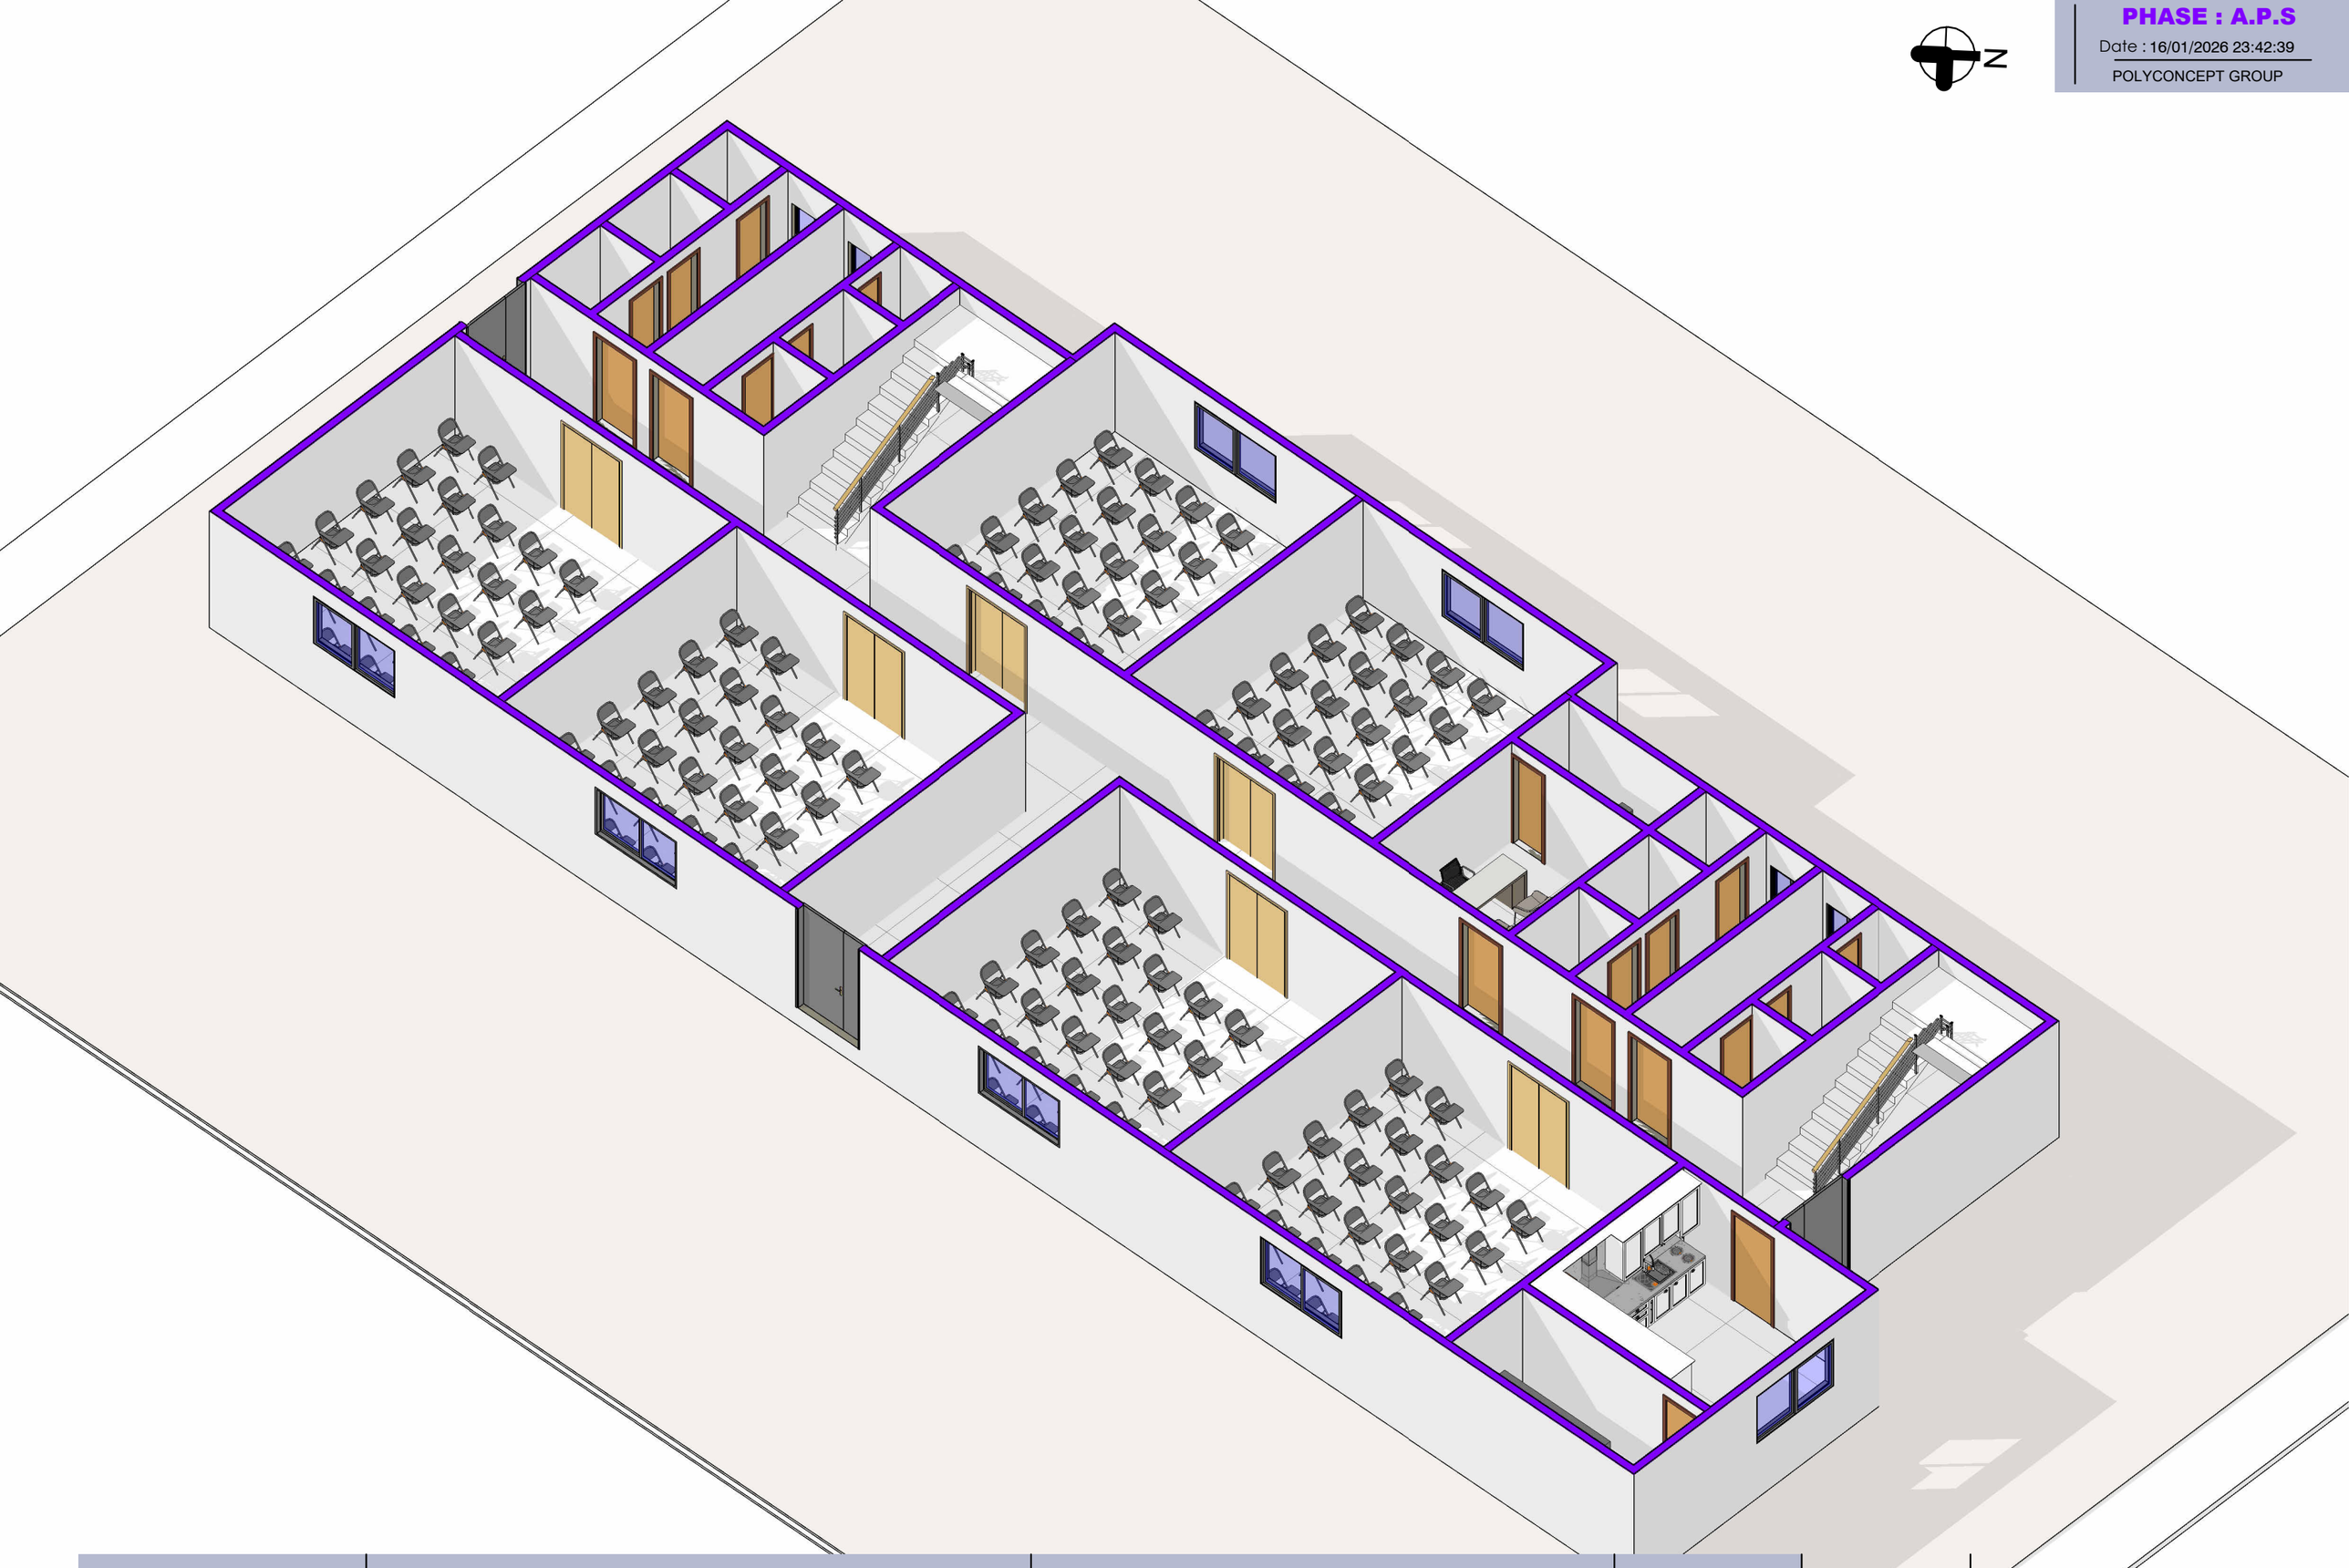

36

Mr AHMADOU KABA

AXO RDC

Echelle:

INTERNAT AS SALAM

_ RDC + 2 ETAGES + TERRASSE

TAMBA_ MISSIRAH

A-107

BY ING MOUSSA
TEL:+221 77 231 96 53
mail: moussac1994.1@gmail.com



PHASE : A.P.S

Date : 16/01/2026 23:42:43

POLYCONCEPT GROUP

36 **Mr AHMADOU KABA**

AXO ETAGE 1

Echelle:


INTERNAT AS SALAM

_ RDC + 2 ETAGES + TERRASSE

TAMBA_ MISSIRAH

A-108

BY ING MOUSSA
TEL:+221 77 231 96 53
mail: moussac1994.1@gmail.com

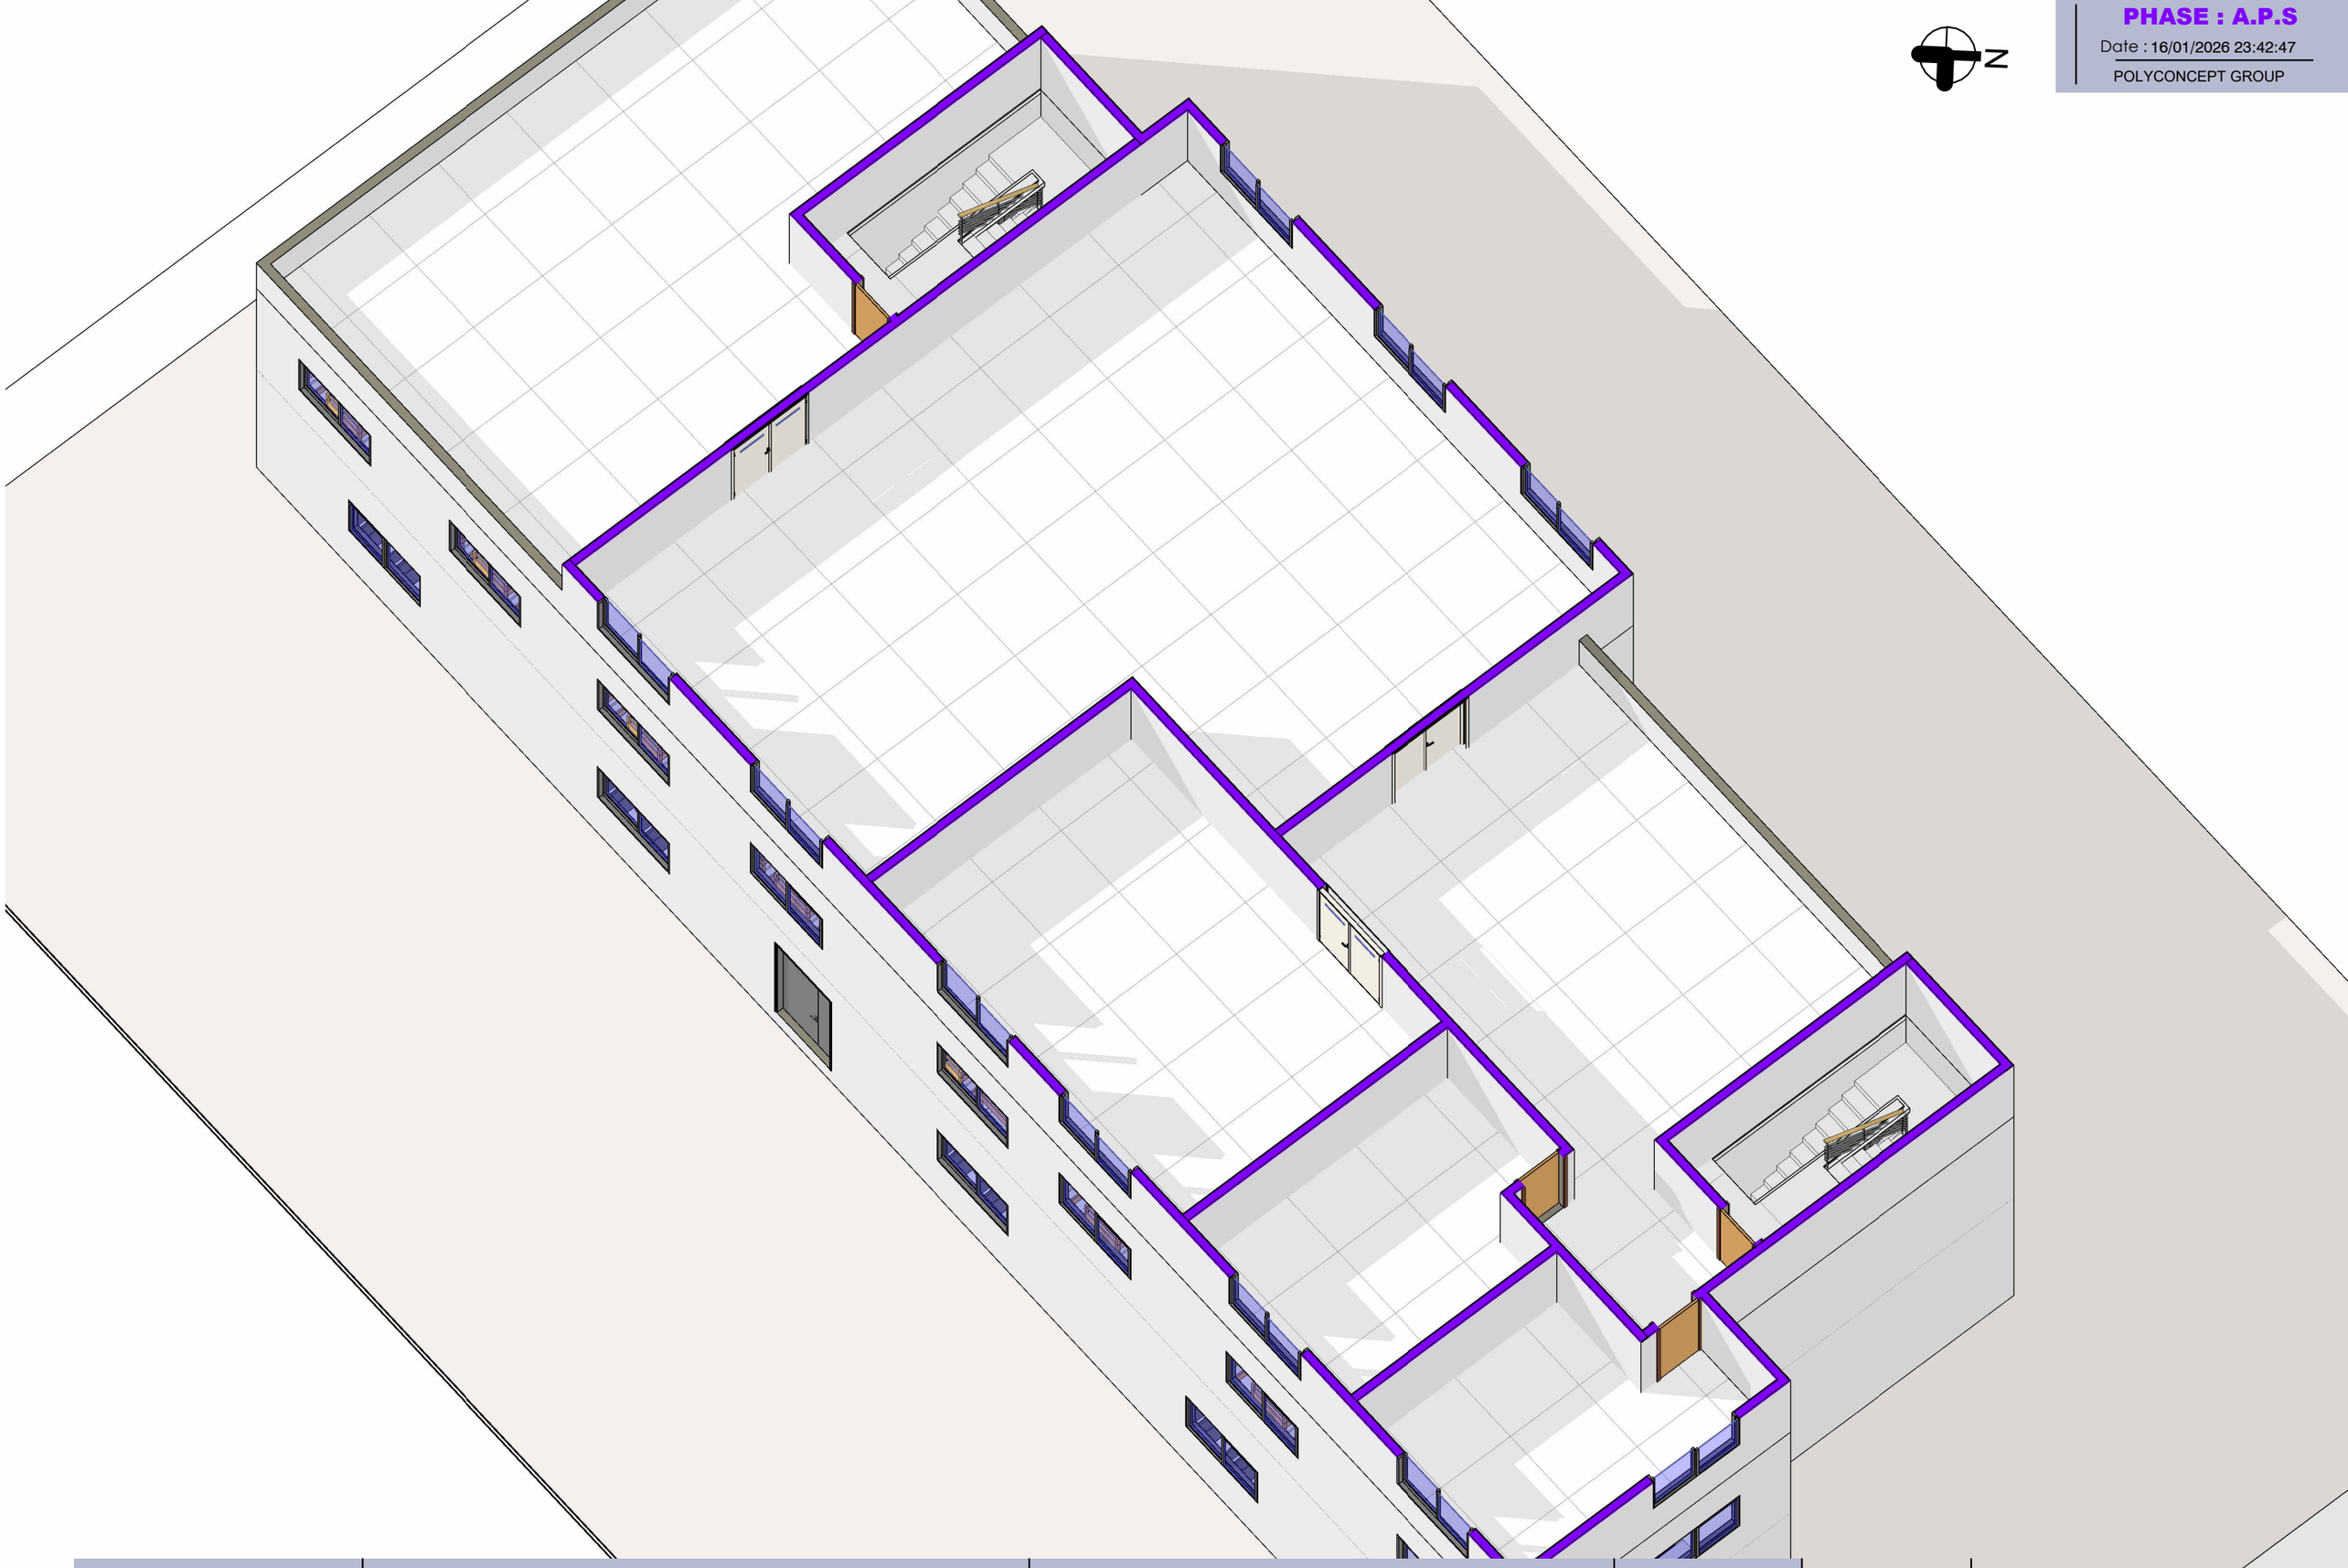

PHASE : A.P.S

Date : 16/01/2026 23:42:47

POLYCONCEPT GROUP

Mr AHMADOU KABA

AXO TERRASSE

Echelle:

INTERNAT AS SALAM

_ RDC + 2 ETAGES + TERRASSE

TAMBA_ MISSIRAH


A-109

BY ING MOUSSA
TEL:+221 77 231 96 53
mail: moussac1994.1@gmail.com

PHASE : A.P.S

Date : 16/01/2026 23:42:51

POLYCONCEPT GROUP

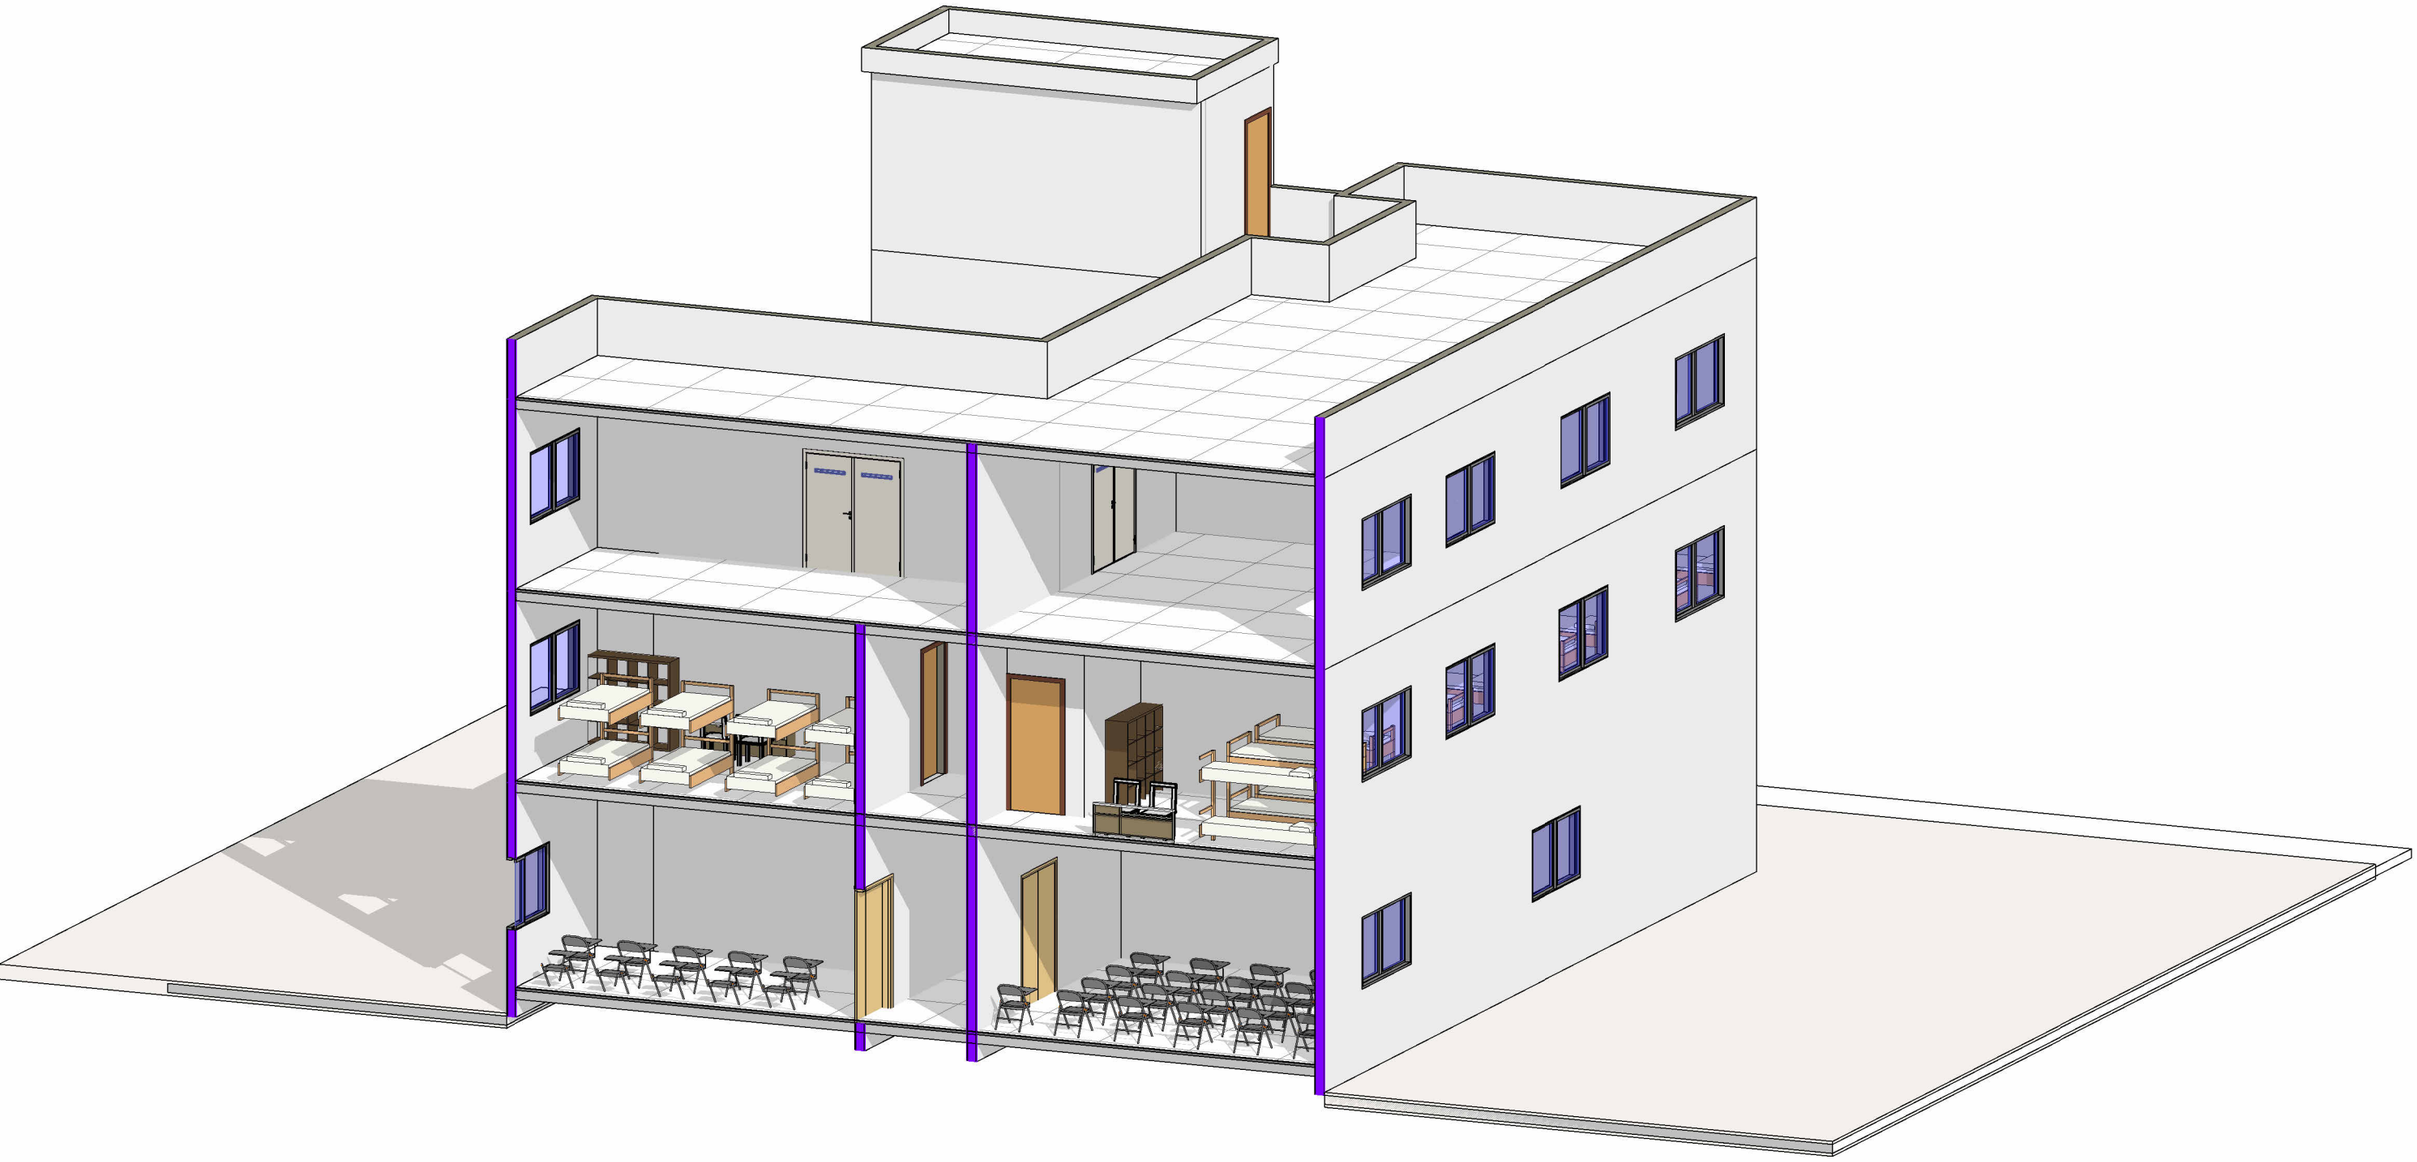

Mr AHMADOU KABA

AXO COUPE 1

Echelle:

INTERNAT AS SALAM

_ RDC + 2 ETAGES + TERRASSE

TAMBA_ MISSIRAH

A-110

BY ING MOUSSA
TEL:+221 77 231 96 53
mail: moussac1994.1@gmail.com



Mr AHMADOU KABA

AXO COUPE 2

Echelle:

INTERNAT AS SALAM

_ RDC + 2 ETAGES + TERRASSE

TAMBA_ MISSIRAH


A-111

BY ING MOUSSA
TEL:+221 77 231 96 53
mail: moussac1994.1@gmail.com

PHASE : A.P.D

Date : 12/08/2026 01:44:18

N

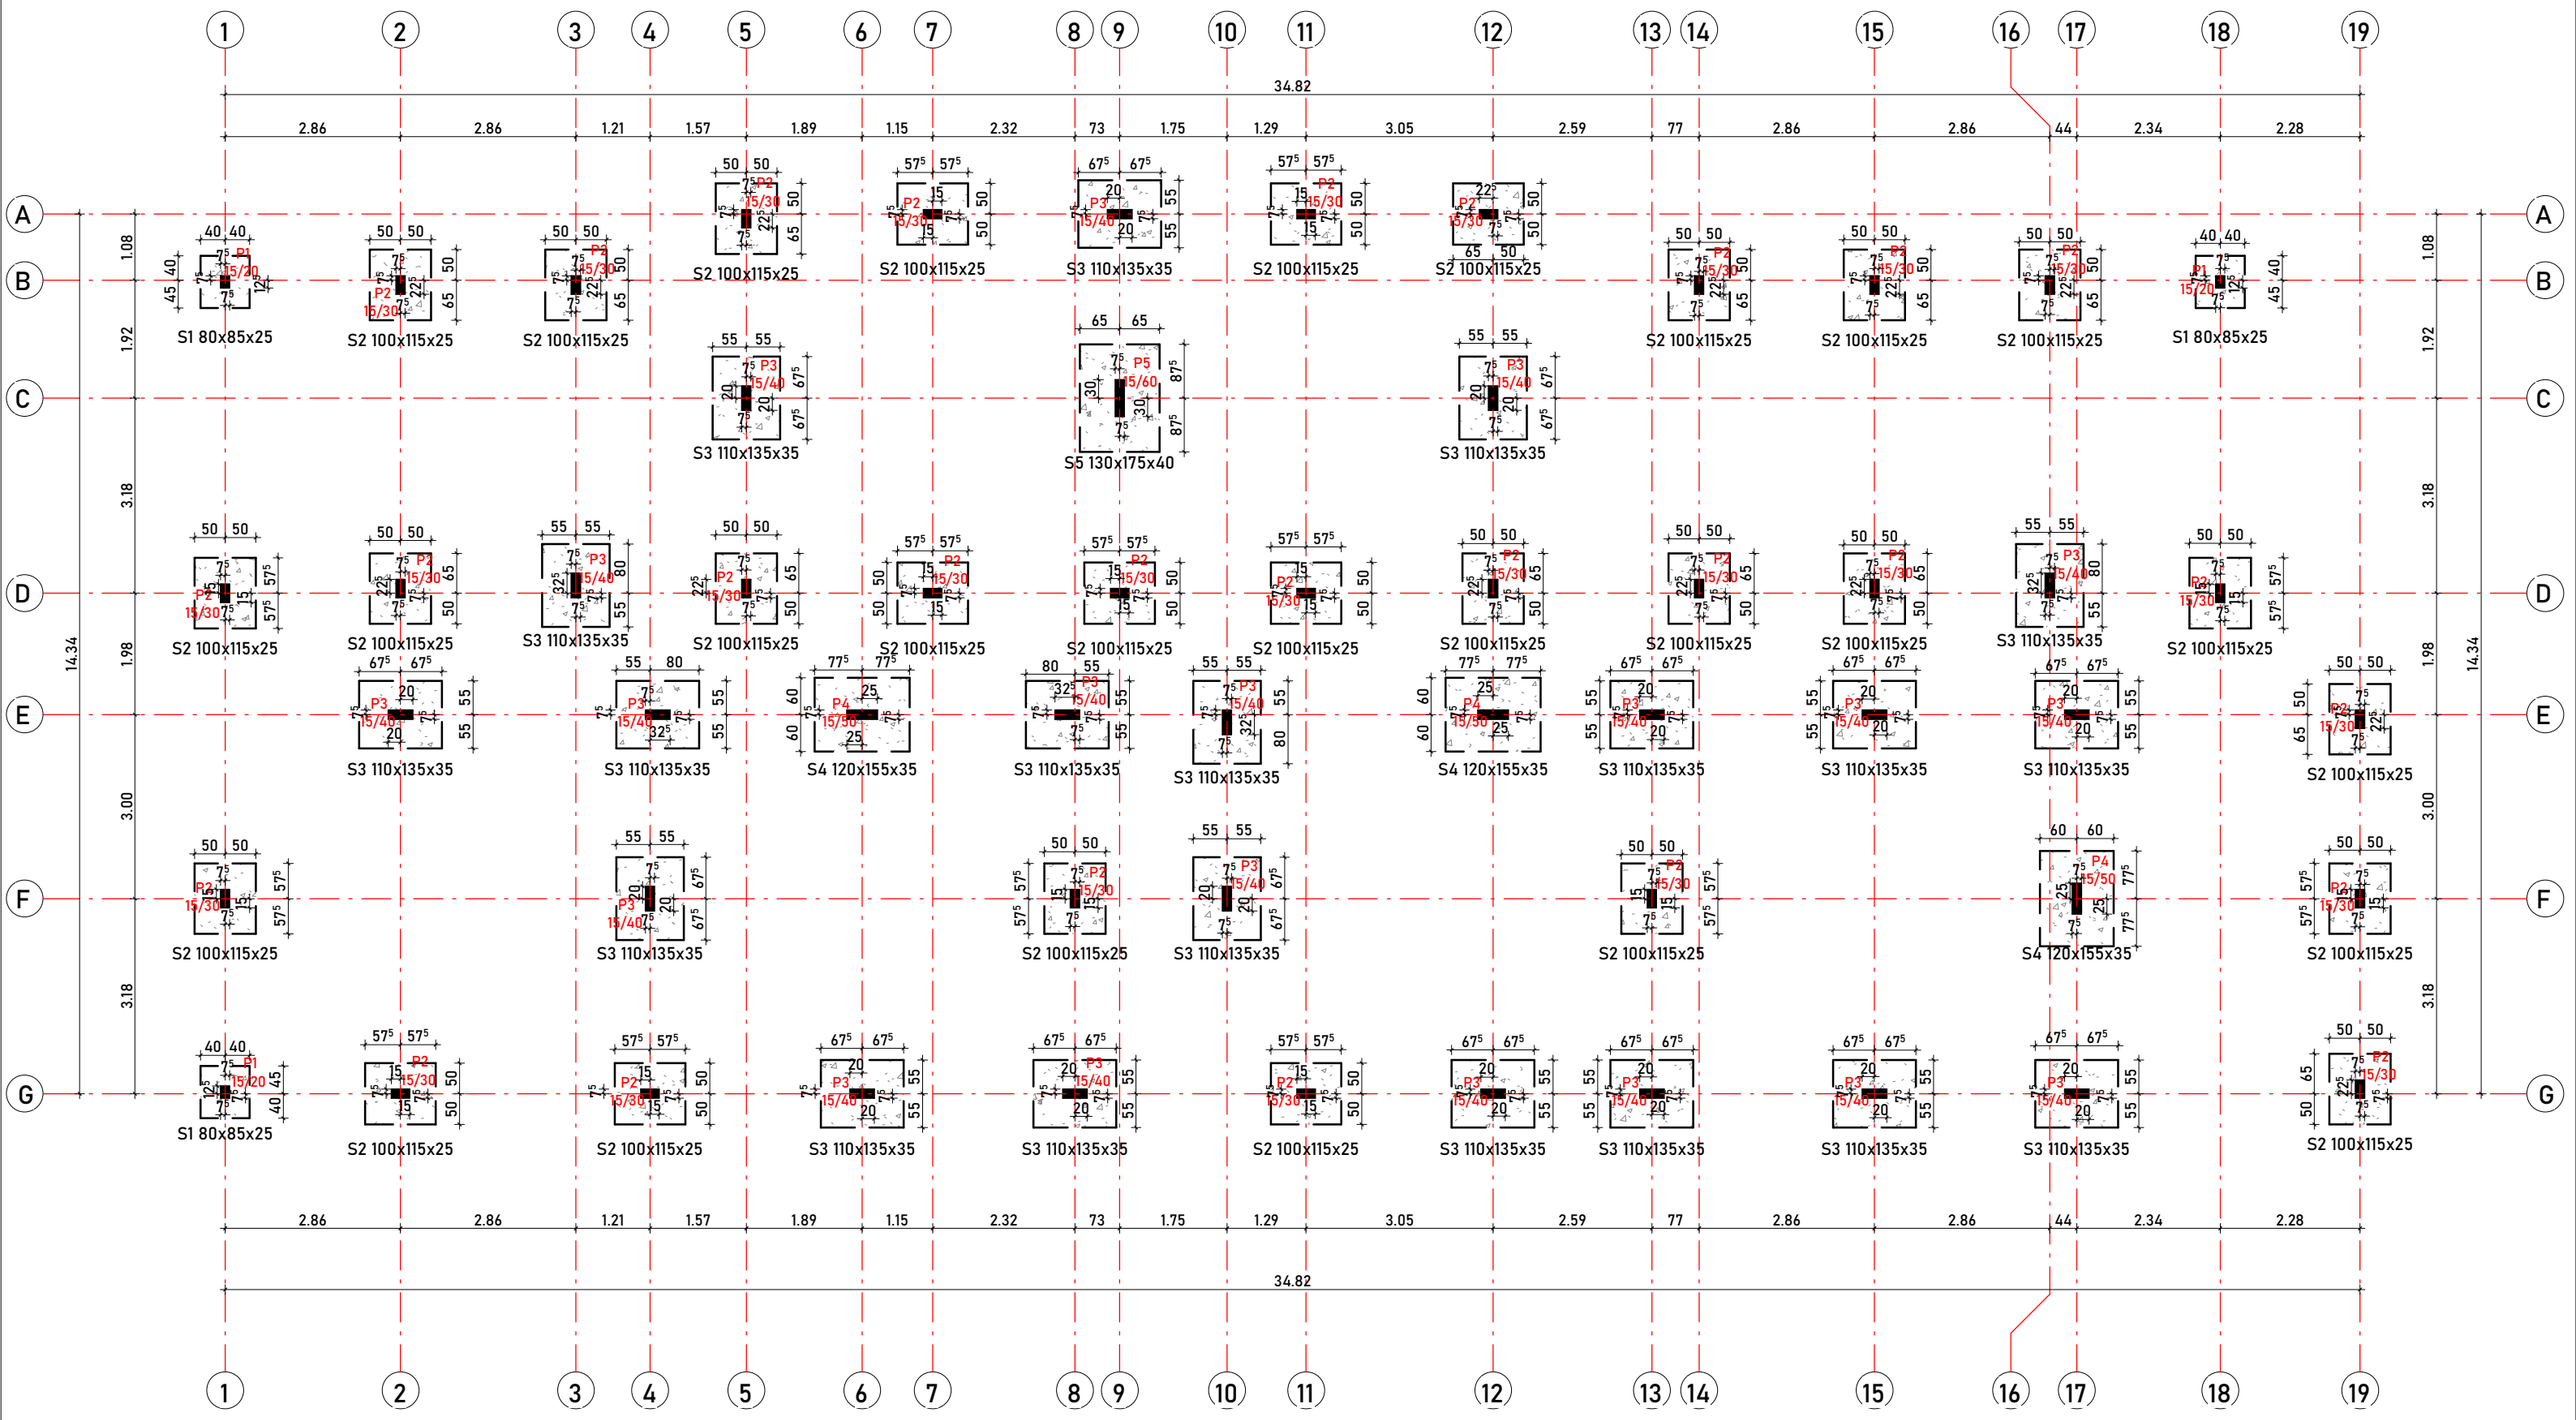

01 Fondations

1 : 100


M. CHEIKH AHMADOU KABA	PLAN D'IMPLANTATIONS DES SEMELLES Echelle: 1 : 100	PROJET R+3 A INTERNAT AS-SALAM TAMBA_ MISSIRAH	01

Ing.Moussa CISSÉ
TEL:+221 77 231 96 53
mail: polyconceptgroup@gmail.com

PHASE : A.P.D

Date : 12/08/2026 01:44:58

N

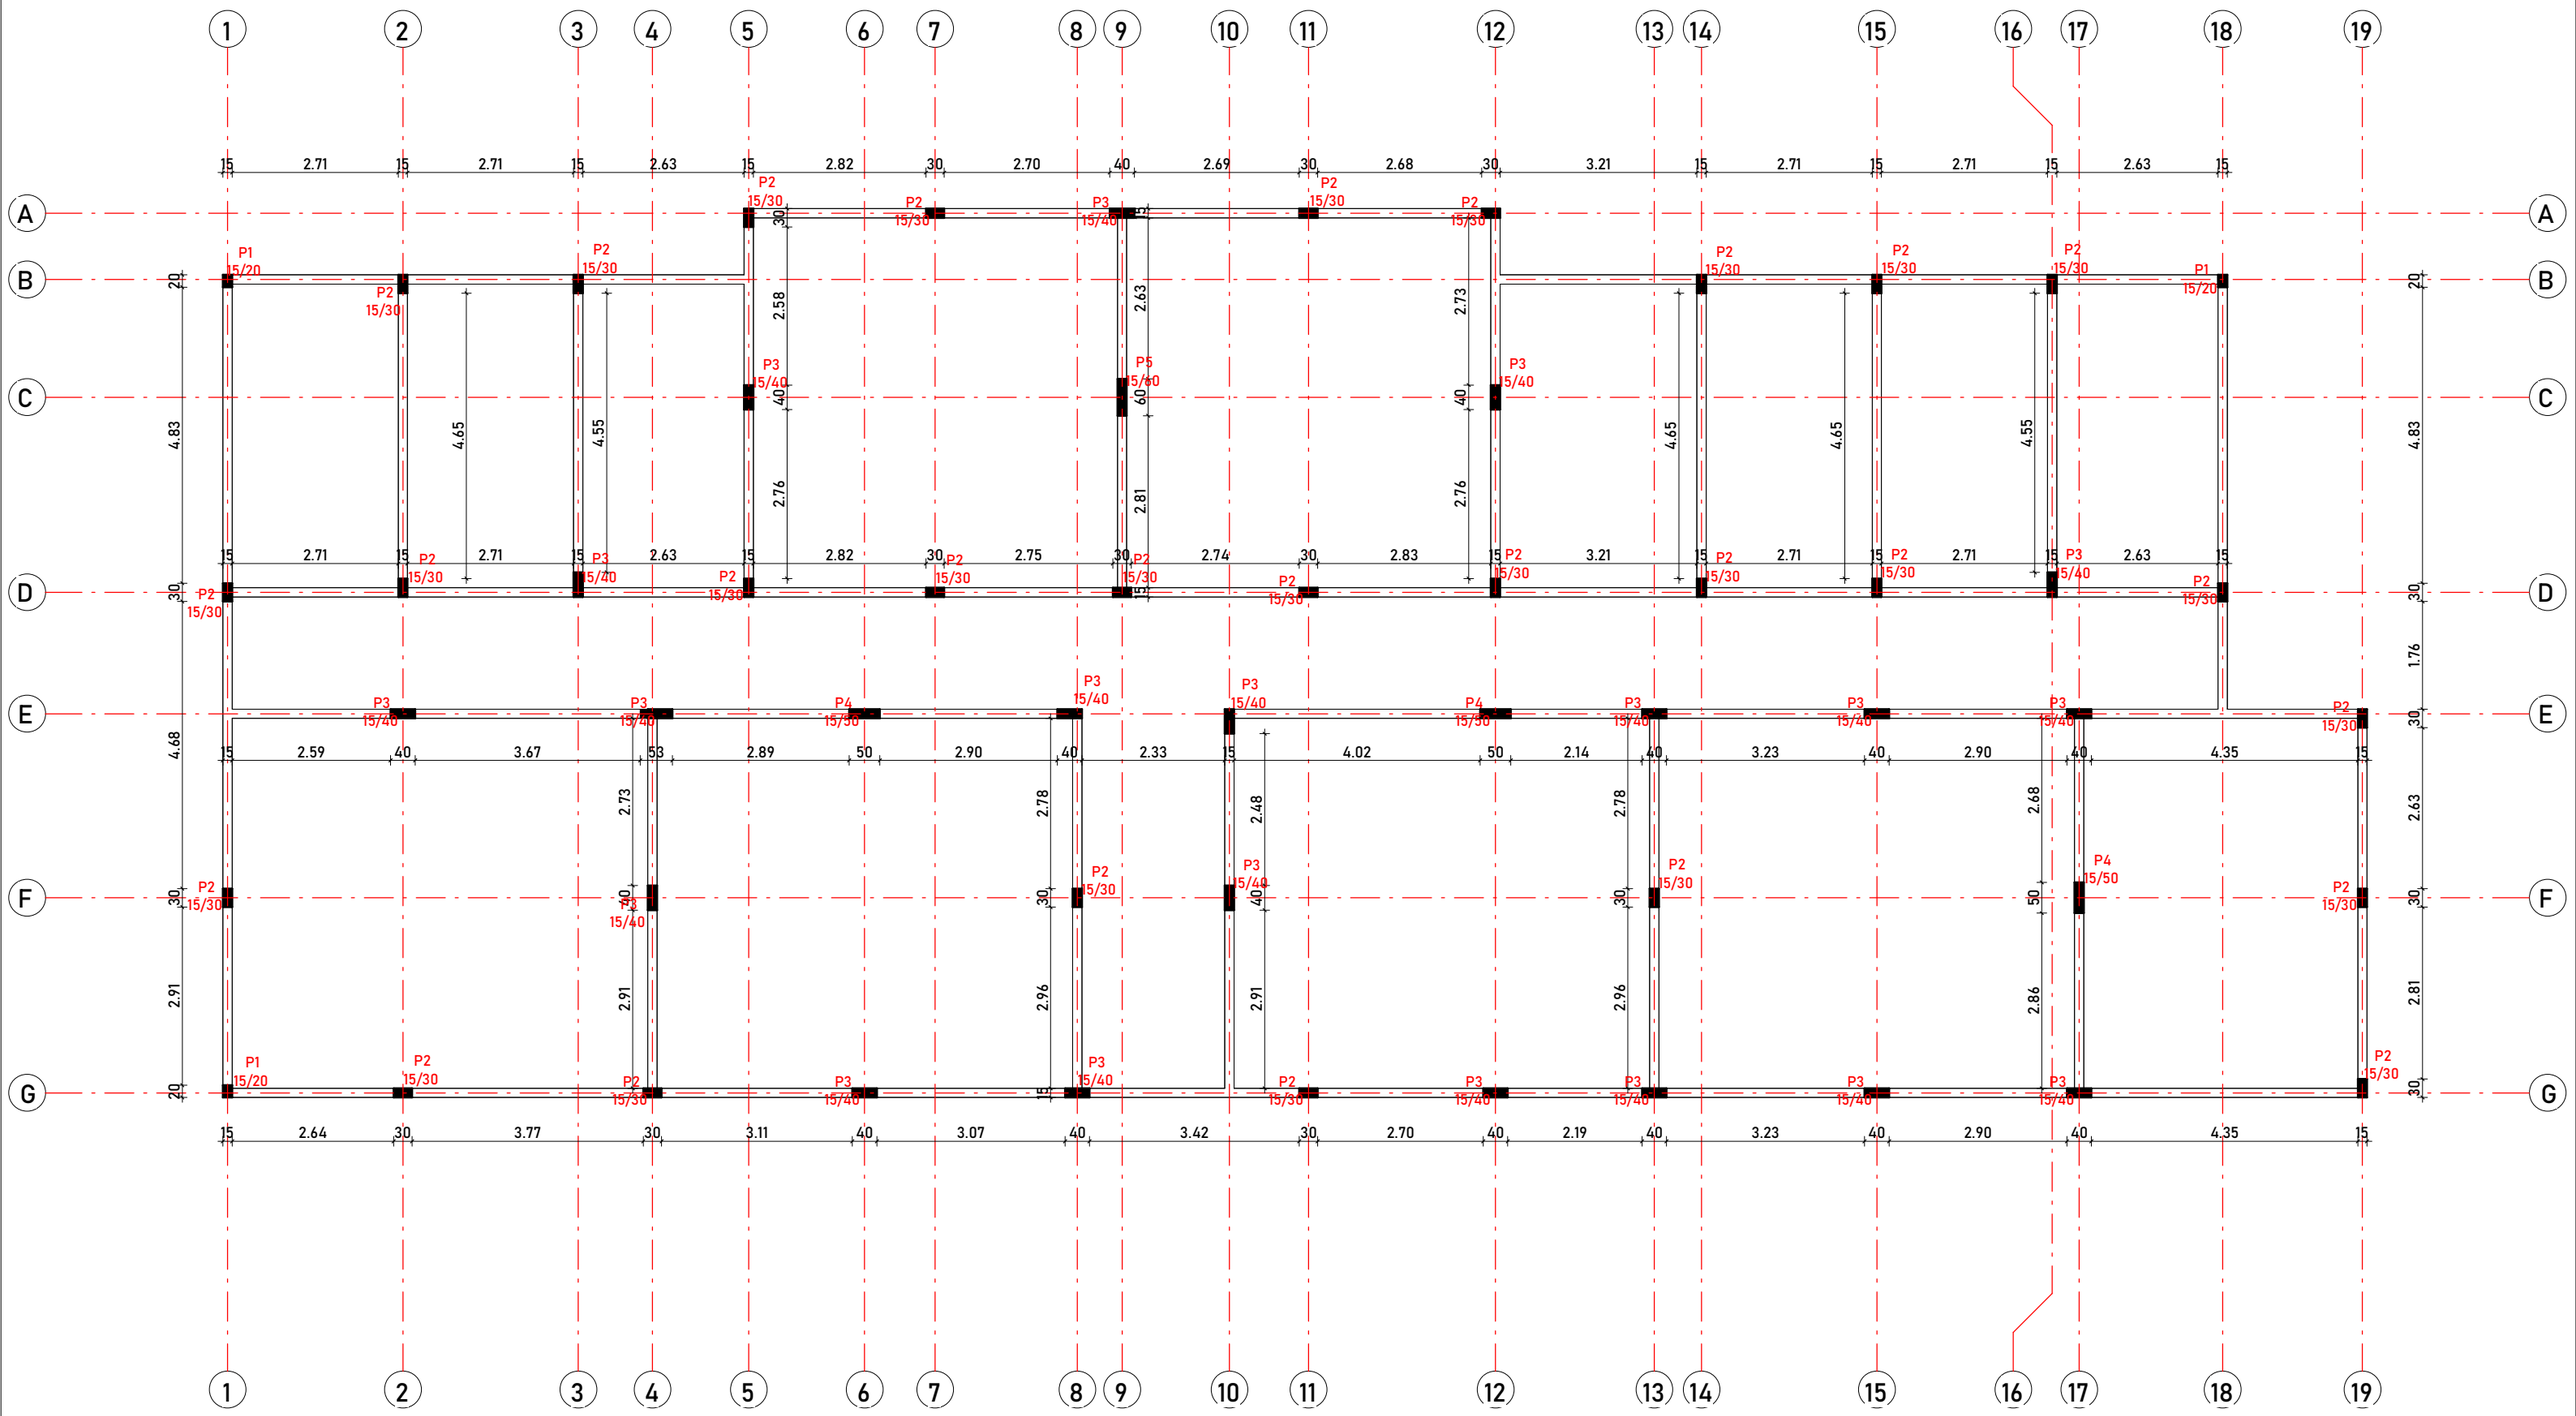

MURS DE SOUBASSEMENT

Echelle: 1 : 100

M. CHEIKH AHMADOU KABA


PROJET R+3 A INTERNAT AS-SALAM


TAMBA_ MISSIRAH

02

Ing.Moussa CISSÉ
TEL:+221 77 231 96 53
mail: polyconceptgroup@gmail.com


Pos.	Armature		Code	Forme	Acier
16	5HA12	l=1.08	00	8 70	HA 500
17	5HA12	l=1.13	00	8 75	HA 500

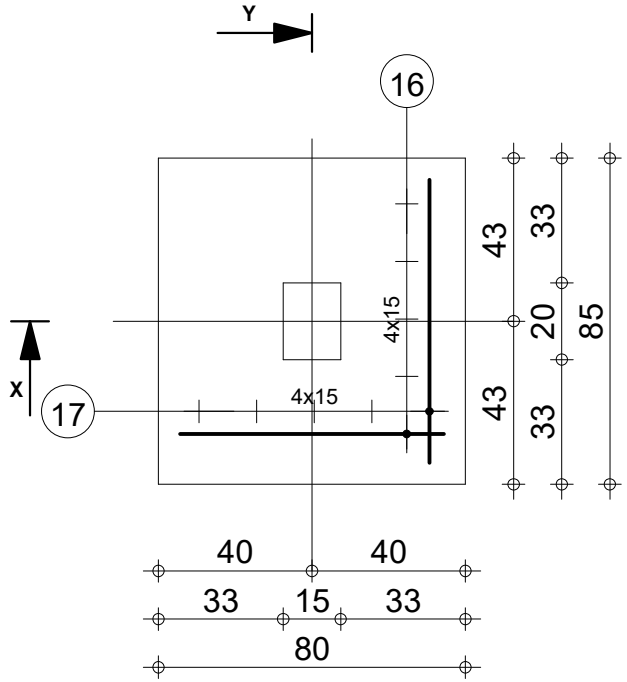

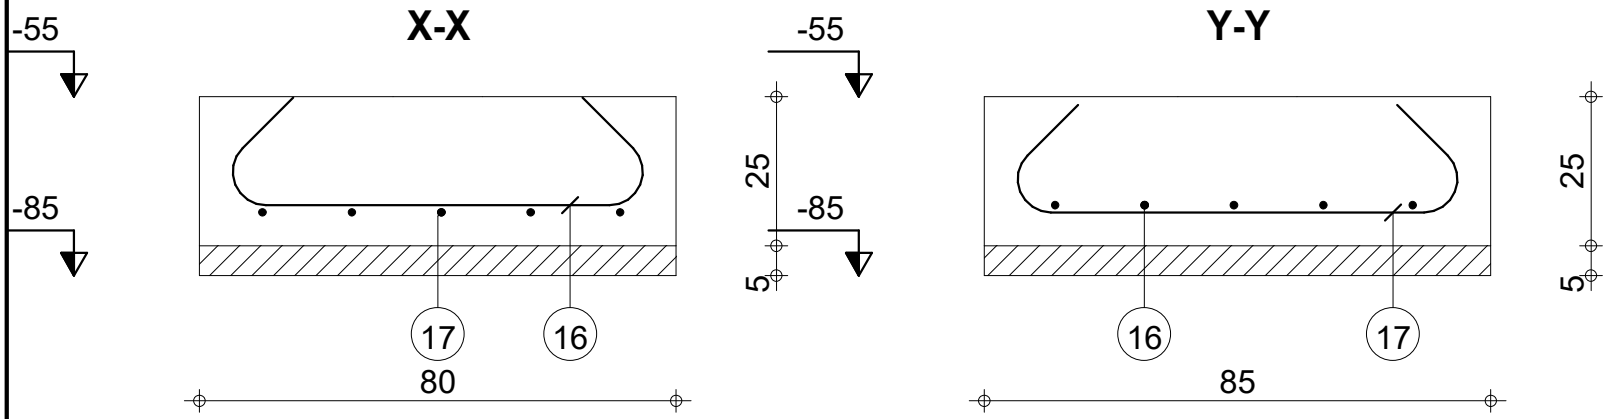

Polyconcept Group	Ing.Moussa CISSÉ	Tél. +221 77 231 96 53	Fax	Acier HA 500 = 9.81 kg
Fissuration préjudiciable			Béton : BETON = 0.17 m3	
FERRAILLAGE DES SEMELLES	**S1**	**Nombre 5**	Surface du coffrage = 0.825 m2 Densité = 57.71 kg/ m3	Enrobage c1 = 5 cm, c2 = 3 cm
R+3 INTERNAT AS-SALAM MISSIRAH				Echelle pour la vue 5.09cm/m Echelle pour la section 7.9cm/m

Pos.	Armature		Code	Forme	Acier
14	7HA12	l=1.28	00	8 90	HA 500
15	6HA12	l=1.43	00	8 1.05	HA 500

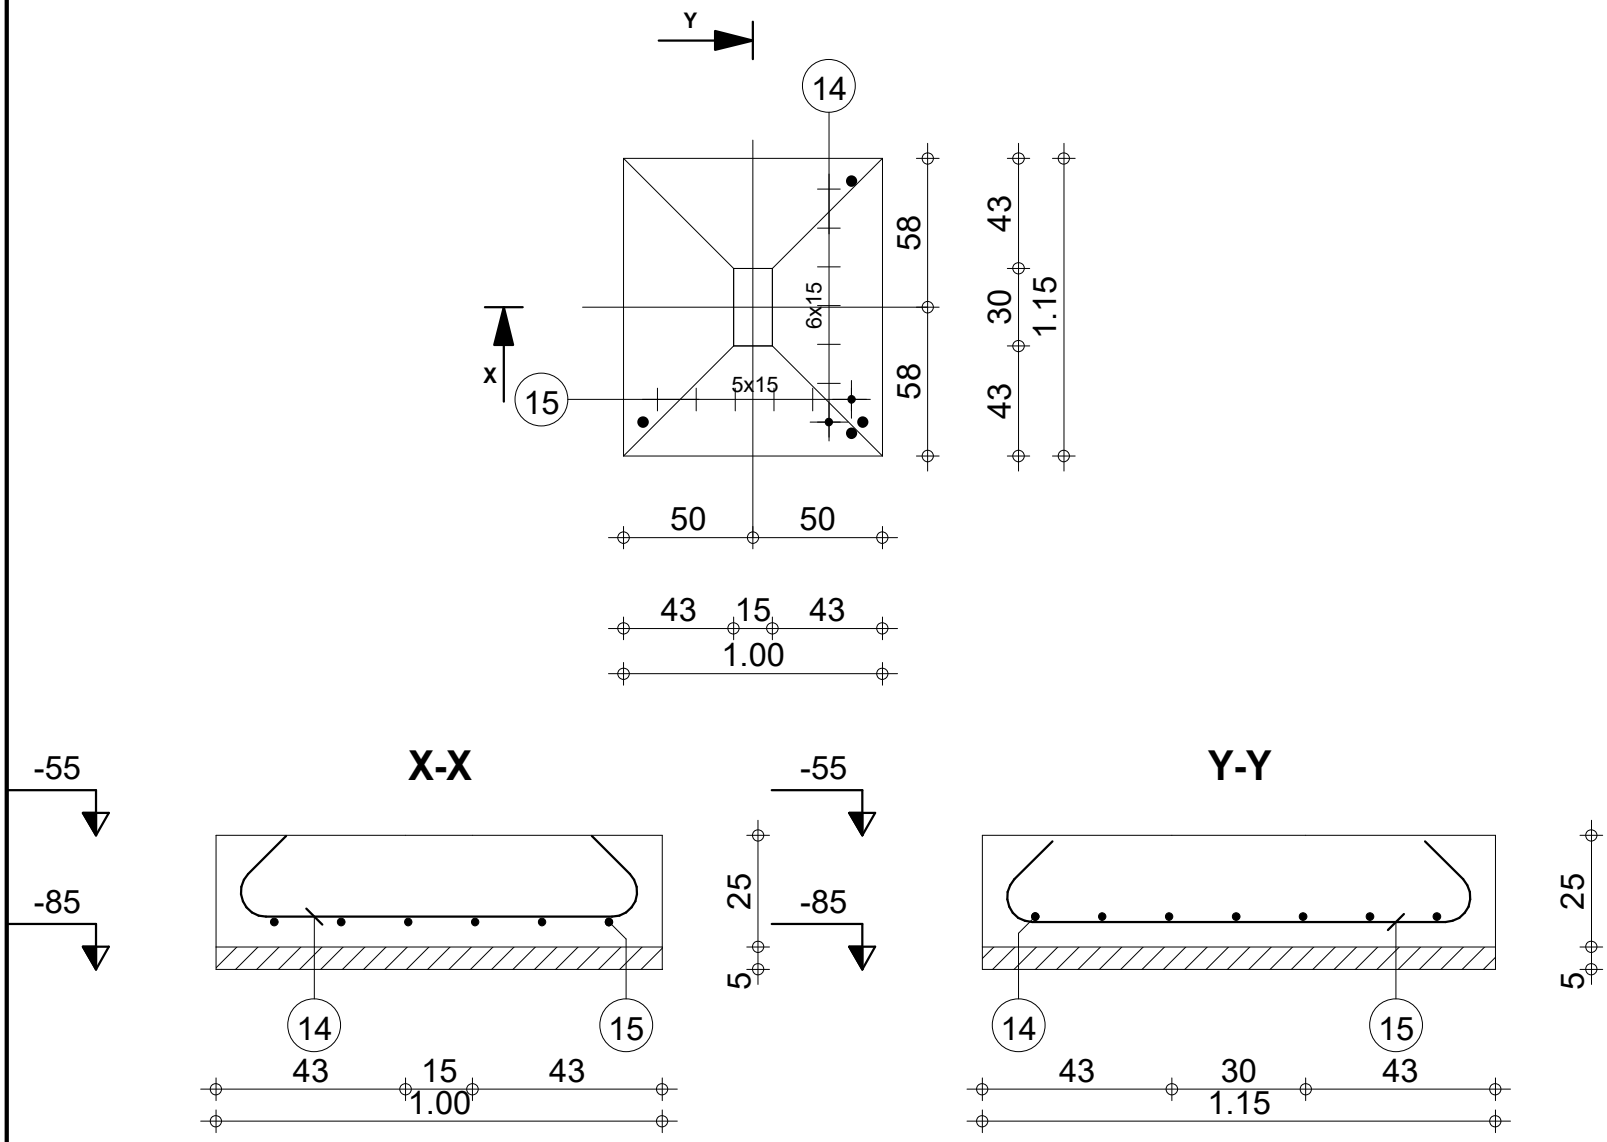

Polyconcept Group	Ing.Moussa CISSÉ	Tél. +221 77 231 96 53	Fax	
Fissuration préjudiciable				
FERRAILLAGE DES SEMELLES	**S2**	**Nombre 21**		
R+3 INTERNAT AS-SALAM MISSIRAH				

Béton : BETON = 0.287 m3

Surface du coffrage = 2.18 m2

Densité = 54.36 kg/ m3


Acier HA 500 = 15.6 kg


Enrobage c1 = 5 cm, c2 = 3 cm


Echelle pour la vue 3.43cm/m

Echelle pour la section 5.91cm/m

Pos.	Armature		Code	Forme	Acier
12	8HA12	l=1.38	00	1.00	HA 500
13	7HA12	l=1.63	00	1.25	HA 500

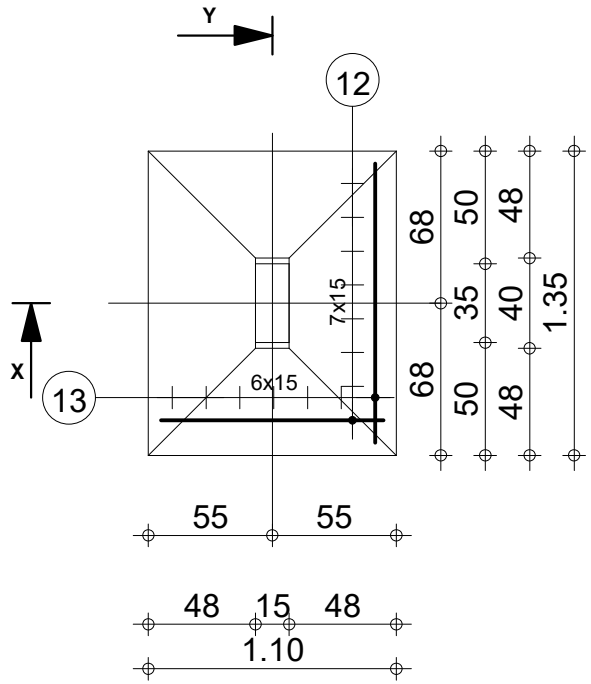


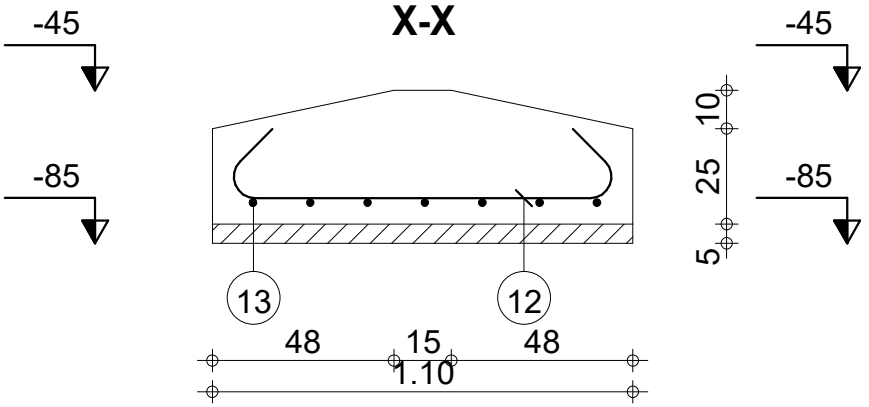


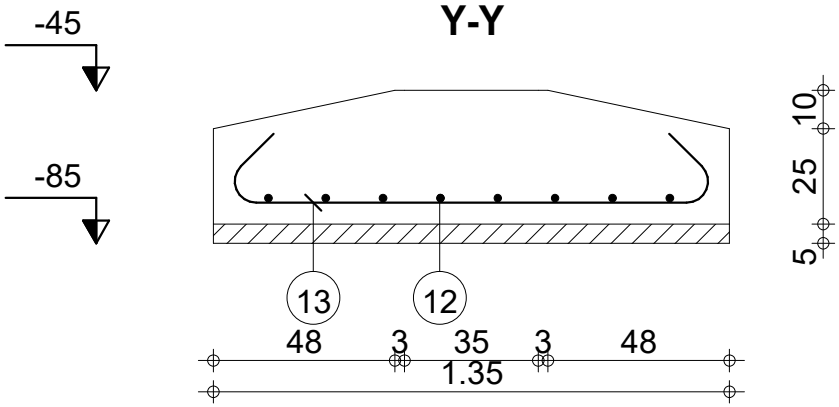

Polyconcept Group	Ing.Moussa CISSÉ	Tél. +221 77 231 96 53	Fax	Acier HA 500 = 19.9 kg
Fissuration préjudiciable			Béton : BETON = 0.46 m3	
FERRAILLAGE DES SEMELLES	**S3**	**Nombre 14**	Surface du coffrage = 2.68 m2 Densité = 43.26 kg/ m3	Enrobage c1 = 5 cm, c2 = 3 cm
R+3 INTERNAT AS-SALAM MISSIRAH				Echelle pour la vue 2.99cm/m Echelle pour la section 5.07cm/m


Pos.	Armature		Code	Forme	Acier
10	10HA12	l=1.48	00	1.10	HA 500
11	10HA12	l=1.83	00	1.45	HA 500

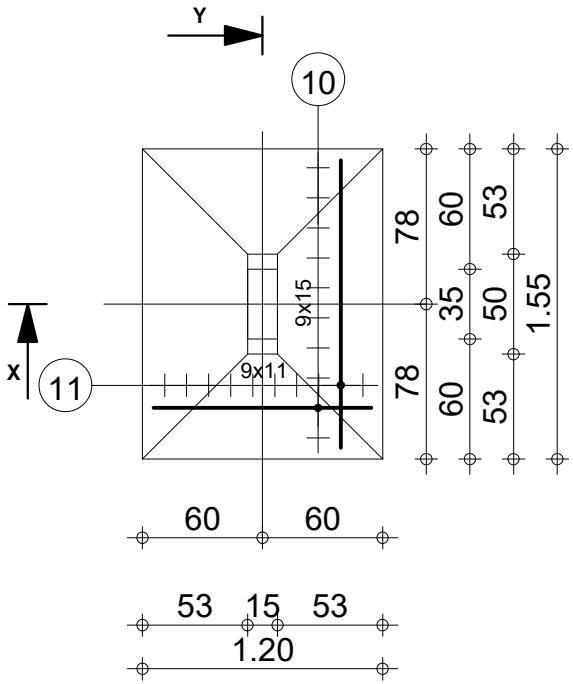


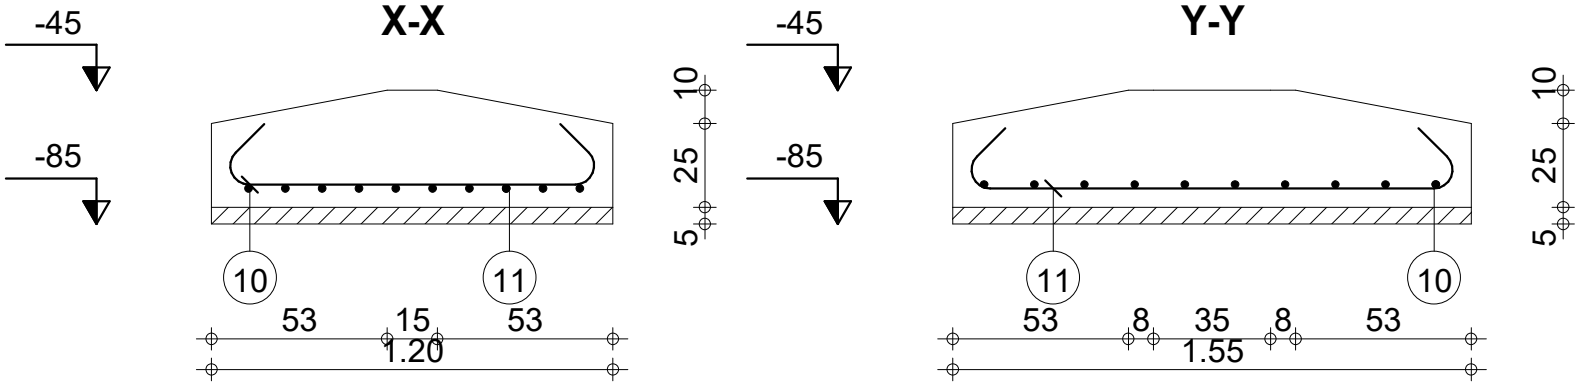

Polyconcept Group	Ing.Moussa CISSÉ	Tél. +221 77 231 96 53	Fax	
Fissuration préjudiciable			Béton : BETON = 0.578 m3	Acier HA 500 = 29.4 kg
FERRAILLAGE DES SEMELLES	**S4**	**Nombre 3**	Surface du coffrage = 3.19 m2 Densité = 50.87 kg/ m3	Enrobage c1 = 5 cm, c2 = 3 cm
R+3 INTERNAT AS-SALAM MISSIRAH				Echelle pour la vue 2.65cm/m Echelle pour la section 4.43cm/m

Pos.	Armature		Code	Forme	Acier
8	11HA12	l=1.58	00	1.20	HA 500
9	12HA12	l=2.03	00	1.65	HA 500

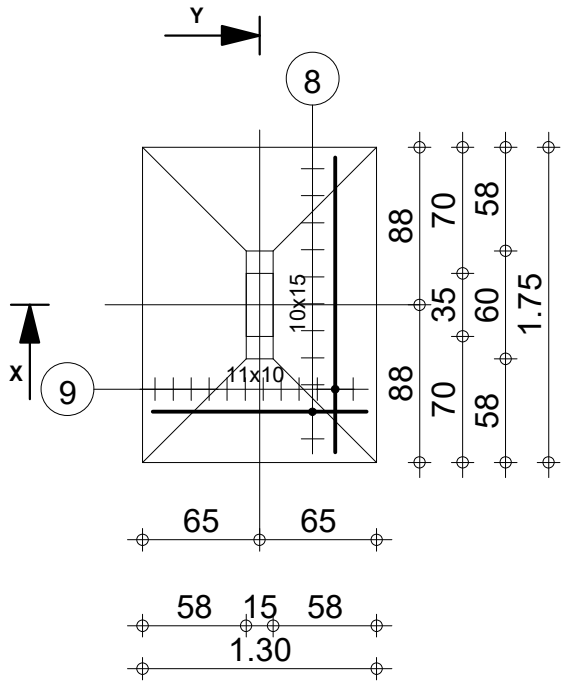

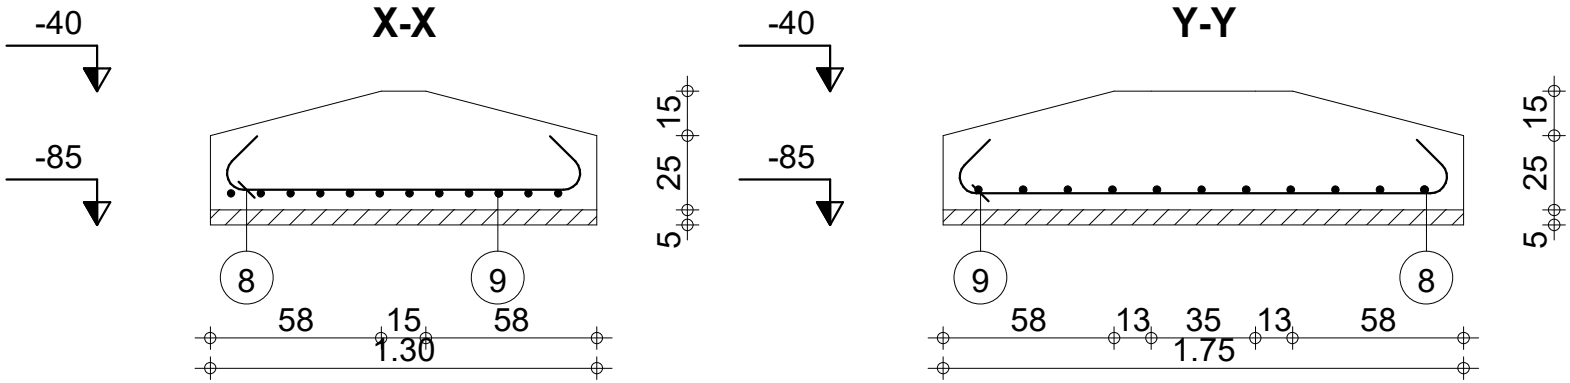

Polyconcept Group	Ing.Moussa CISSÉ	Tél. +221 77 231 96 53	Fax	
Fissuration préjudiciable				
FERRAILLAGE DES SEMELLES	**S5**	**Nombre 1**		
R+3 INTERNAT AS-SALAM MISSIRAH				

Béton : BETON = 0.778 m3

Surface du coffrage = 3.78 m2

Densité = 47.69 kg/ m3


Acier HA 500 = 37.1 kg

Enrobage c1 = 5 cm, c2 = 3 cm


Echelle pour la vue 2.39cm/m

Echelle pour la section 3.94cm/m

Pos.	Armature		Code	Forme	Acier
1	4HA12	l=3.73	00	3.73	HA 500
7	21HA6	l=58	31	9 14 8	HA 500

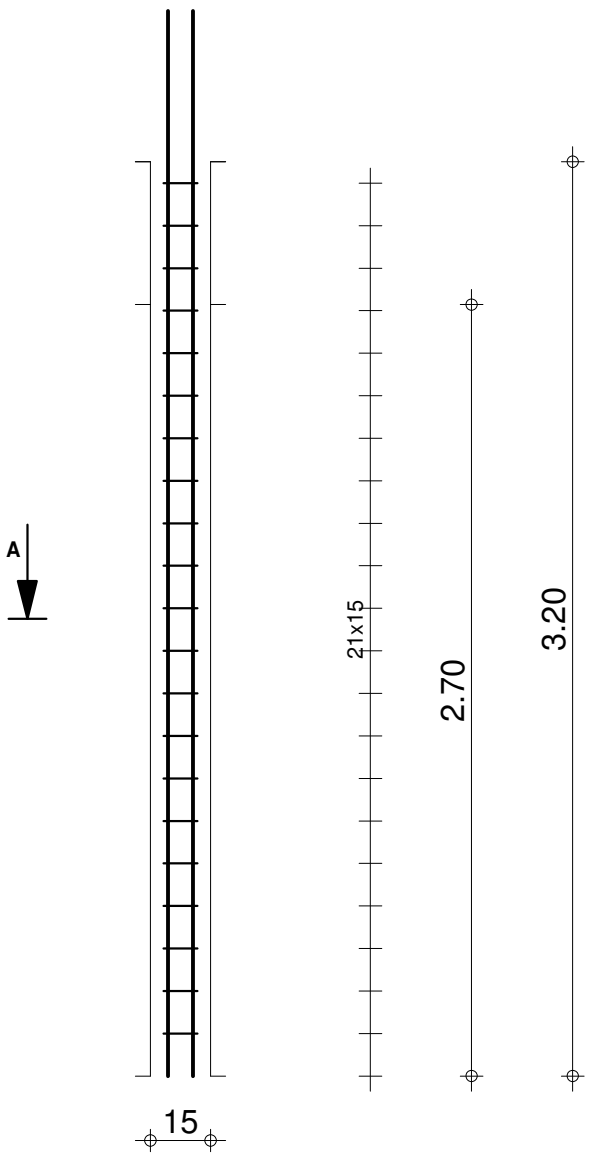

A-A

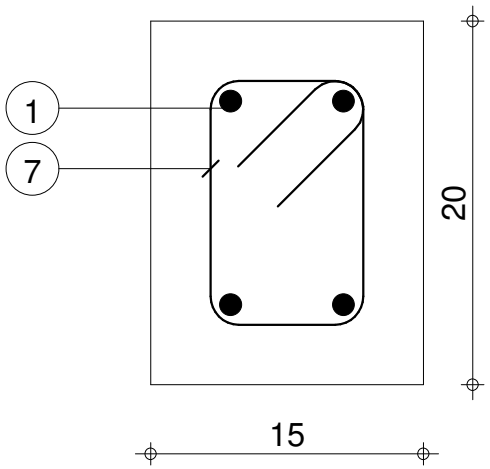

Polyconcept Group Ing.Moussa CISSÉ Tél. +221 77 231 96 53 Fax

FERRAILLAGE DES POTEAUX

R+3 INTERNAT AS-SALAM MISSIRAH


P1

Section 15x20

Acier HA 500 = 13.2 kg
Acier HA 500 = 2.69 kg
Béton : BETON25 = 0.081 m3
Surface du coffrage = 1.89 m2
Enrobage 3 cm

Echelle pour la vue 5.31cm/m x 3.79cm/m
Echelle pour la section 24.1cm/m

Pos.	Armature		Code	Forme	Acier
1	4HA12	l=3.73	00	3.73	HA 500
6	21HA6	l=78	31	9 24 8	HA 500

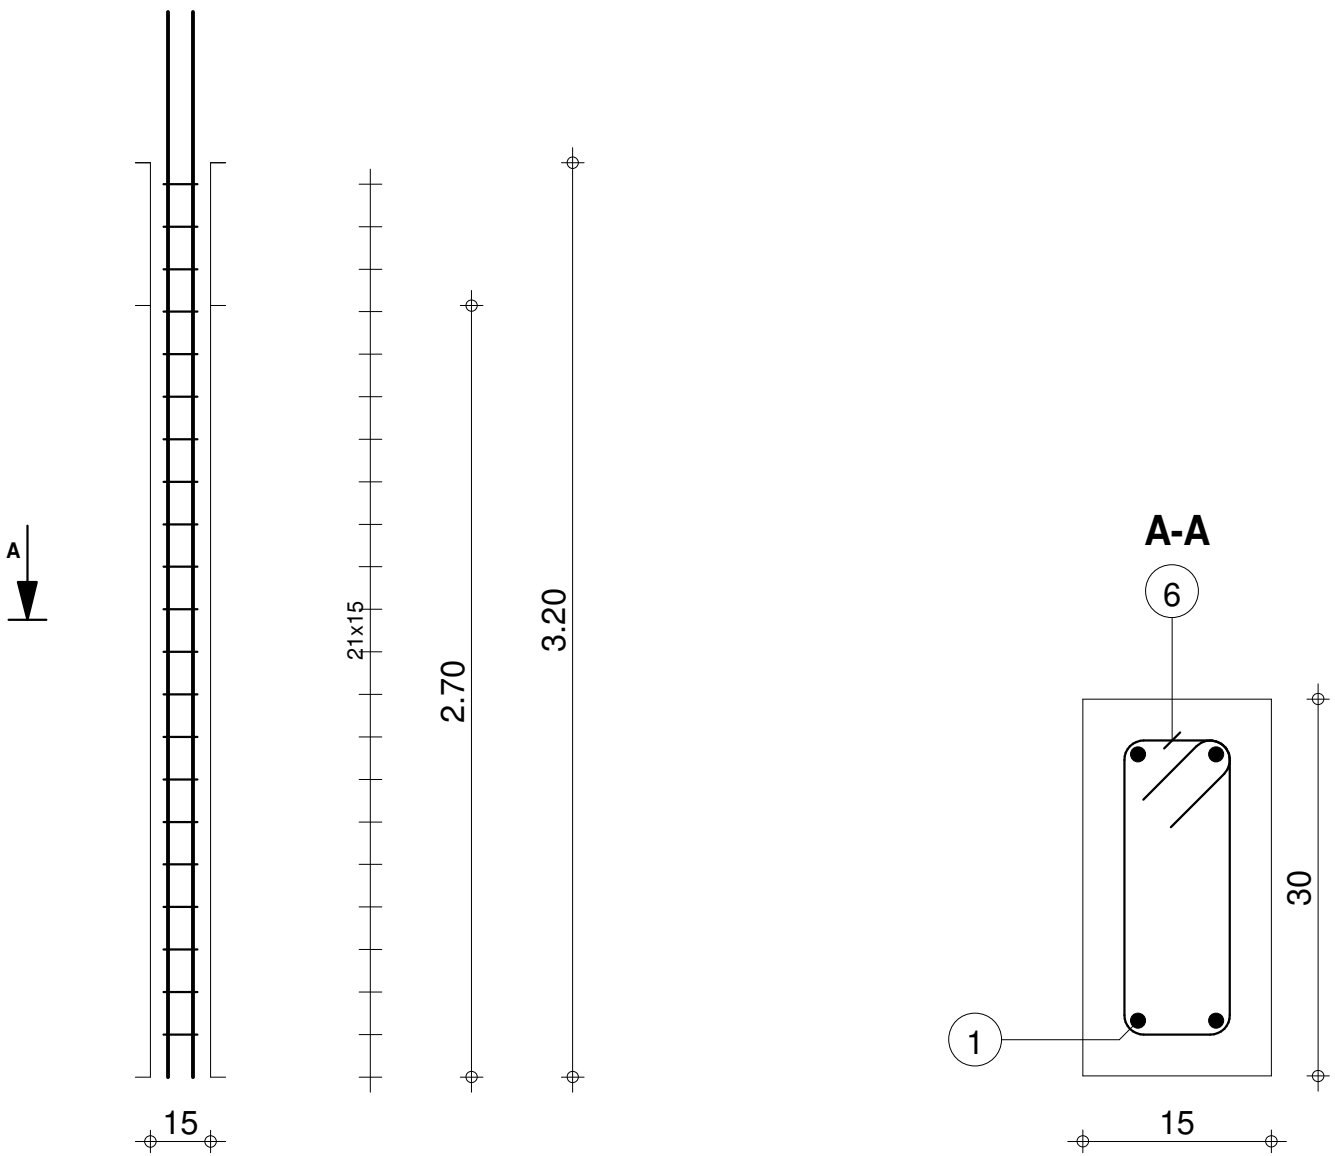

Polyconcept Group Ing.Moussa CISSÉ Tél. +221 77 231 96 53 Fax

FERRAILLAGE DES POTEAUX

R+3 INTERNAT AS-SALAM MISSIRAH


P2


Section 15x30

Acier HA 500 = 13.2 kg
Acier HA 500 = 3.63 kg
Béton : BETON25 = 0.121 m3
Surface du coffrage = 2.43 m2
Enrobage 3 cm

Echelle pour la vue 5.31cm/m x 3.79cm/m
Echelle pour la section 16.7cm/m

Pos.	Armature		Code	Forme	Acier
1	6HA12	l=3.73	00	3.73	HA 500
3	21HA6	l=21	00	5 9	HA 500
5	21HA6	l=98	31	9 34 8	HA 500

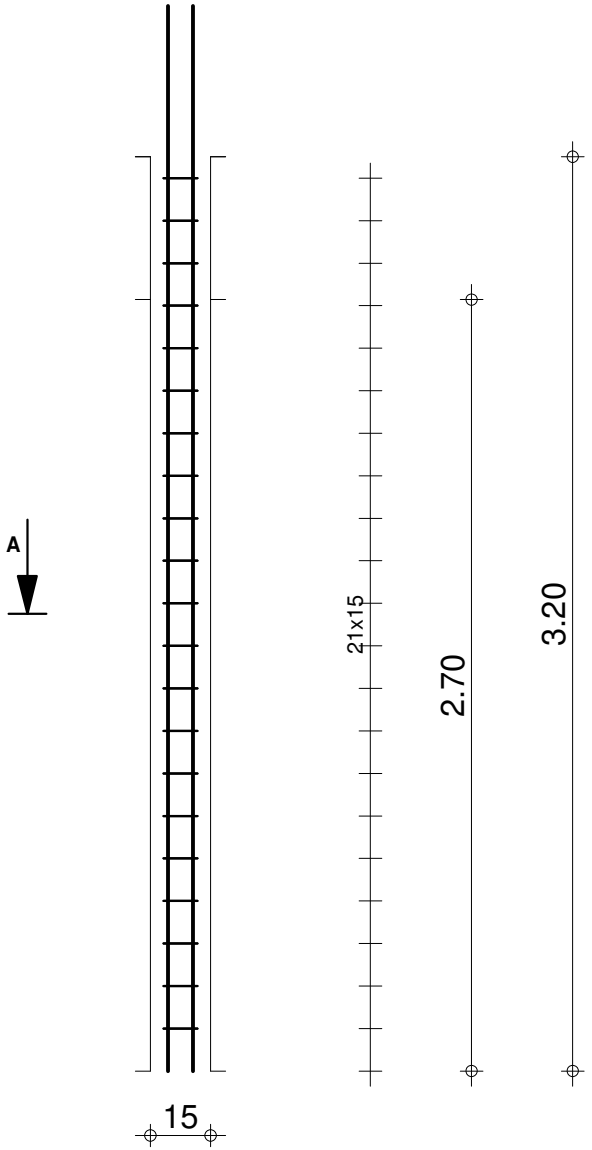

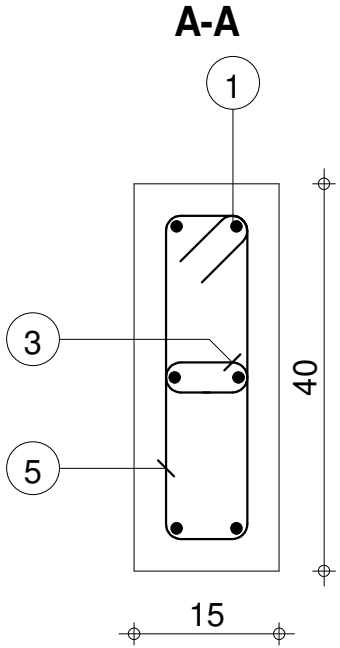

Polyconcept Group Ing.Moussa CISSÉ Tél. +221 77 231 96 53 Fax

FERRAILLAGE DES POTEAUX

R+3 INTERNAT AS-SALAM MISSIRAH


P3

Section 15x40


Acier HA 500 = 19.9 kg
Acier HA 500 = 5.54 kg
Béton : BETON25 = 0.162 m3
Surface du coffrage = 2.97 m2
Enrobage 3 cm

Echelle pour la vue 5.31cm/m x 3.79cm/m
Echelle pour la section 12.8cm/m

Pos.	Armature		Code	Forme	Acier
1	8HA12	l=3.73	00	3.73	HA 500
3	42HA6	l=21	00	5 9	HA 500
4	21HA6	l=1.18	31	9 44 8	HA 500

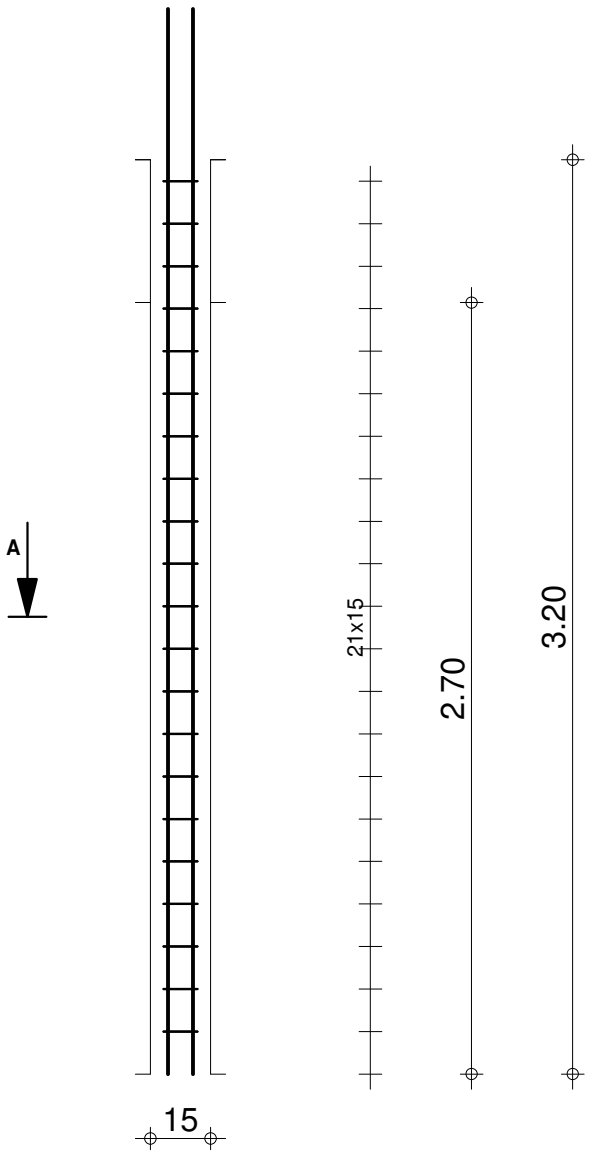

A-A

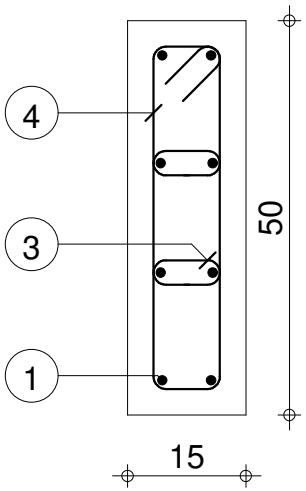

Polyconcept Group Ing.Moussa CISSÉ Tél. +221 77 231 96 53 Fax

FERRAILLAGE DES POTEAUX

R+3 INTERNAT AS-SALAM MISSIRAH


P4


Section 15x50

Acier HA 500 = 26.5 kg
Acier HA 500 = 7.45 kg
Béton : BETON25 = 0.203 m3
Surface du coffrage = 3.51 m2
Enrobage 3 cm

Echelle pour la vue 5.31cm/m x 3.79cm/m
Echelle pour la section 10.5cm/m

Pos.	Armature		Code	Forme	Acier
1	10HA12	l=3.73	00	3.73	HA 500
2	18HA6	l=1.38	31	9 5 8	HA 500
3	54HA6	l=21	00	5 9	HA 500

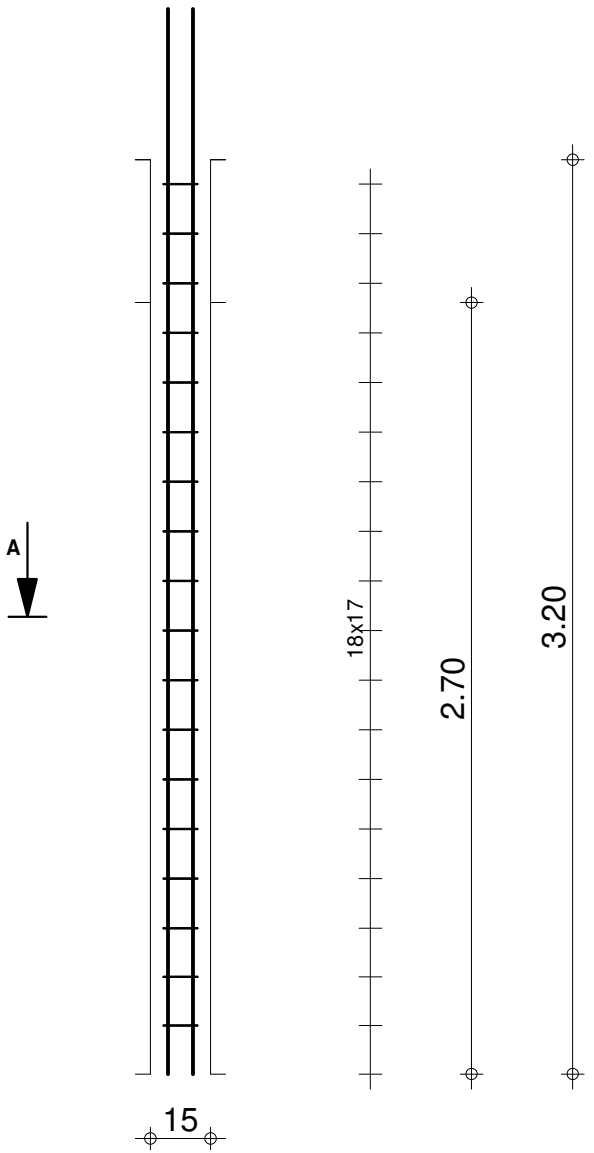

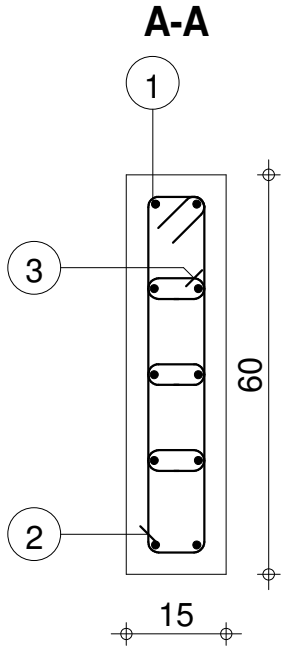

Polyconcept Group Ing.Moussa CISSÉ Tél. +221 77 231 96 53 Fax

FERRAILLAGE DES POTEAUX

R+3 INTERNAT AS-SALAM MISSIRAH

P5

Section 15x60

Acier HA 500 = 33.1 kg
Acier HA 500 = 8.03 kg
Béton : BETON25 = 0.243 m3
Surface du coffrage = 4.05 m2
Enrobage 3 cm
Echelle pour la vue 5.31cm/m x 3.79cm/m
Echelle pour la section 8.83cm/m