

Maitre d'Ouvrage : M.RAMAU

Maitre d'Oeuvre : M.Moussa CISSÉ

VUE 1

Echelle:

PROJET: LIFE STYLE


00_16

_ SS + 8 ETAGES _

DAKAR_ Sénégal

Date

13/04/2026 06:22:07

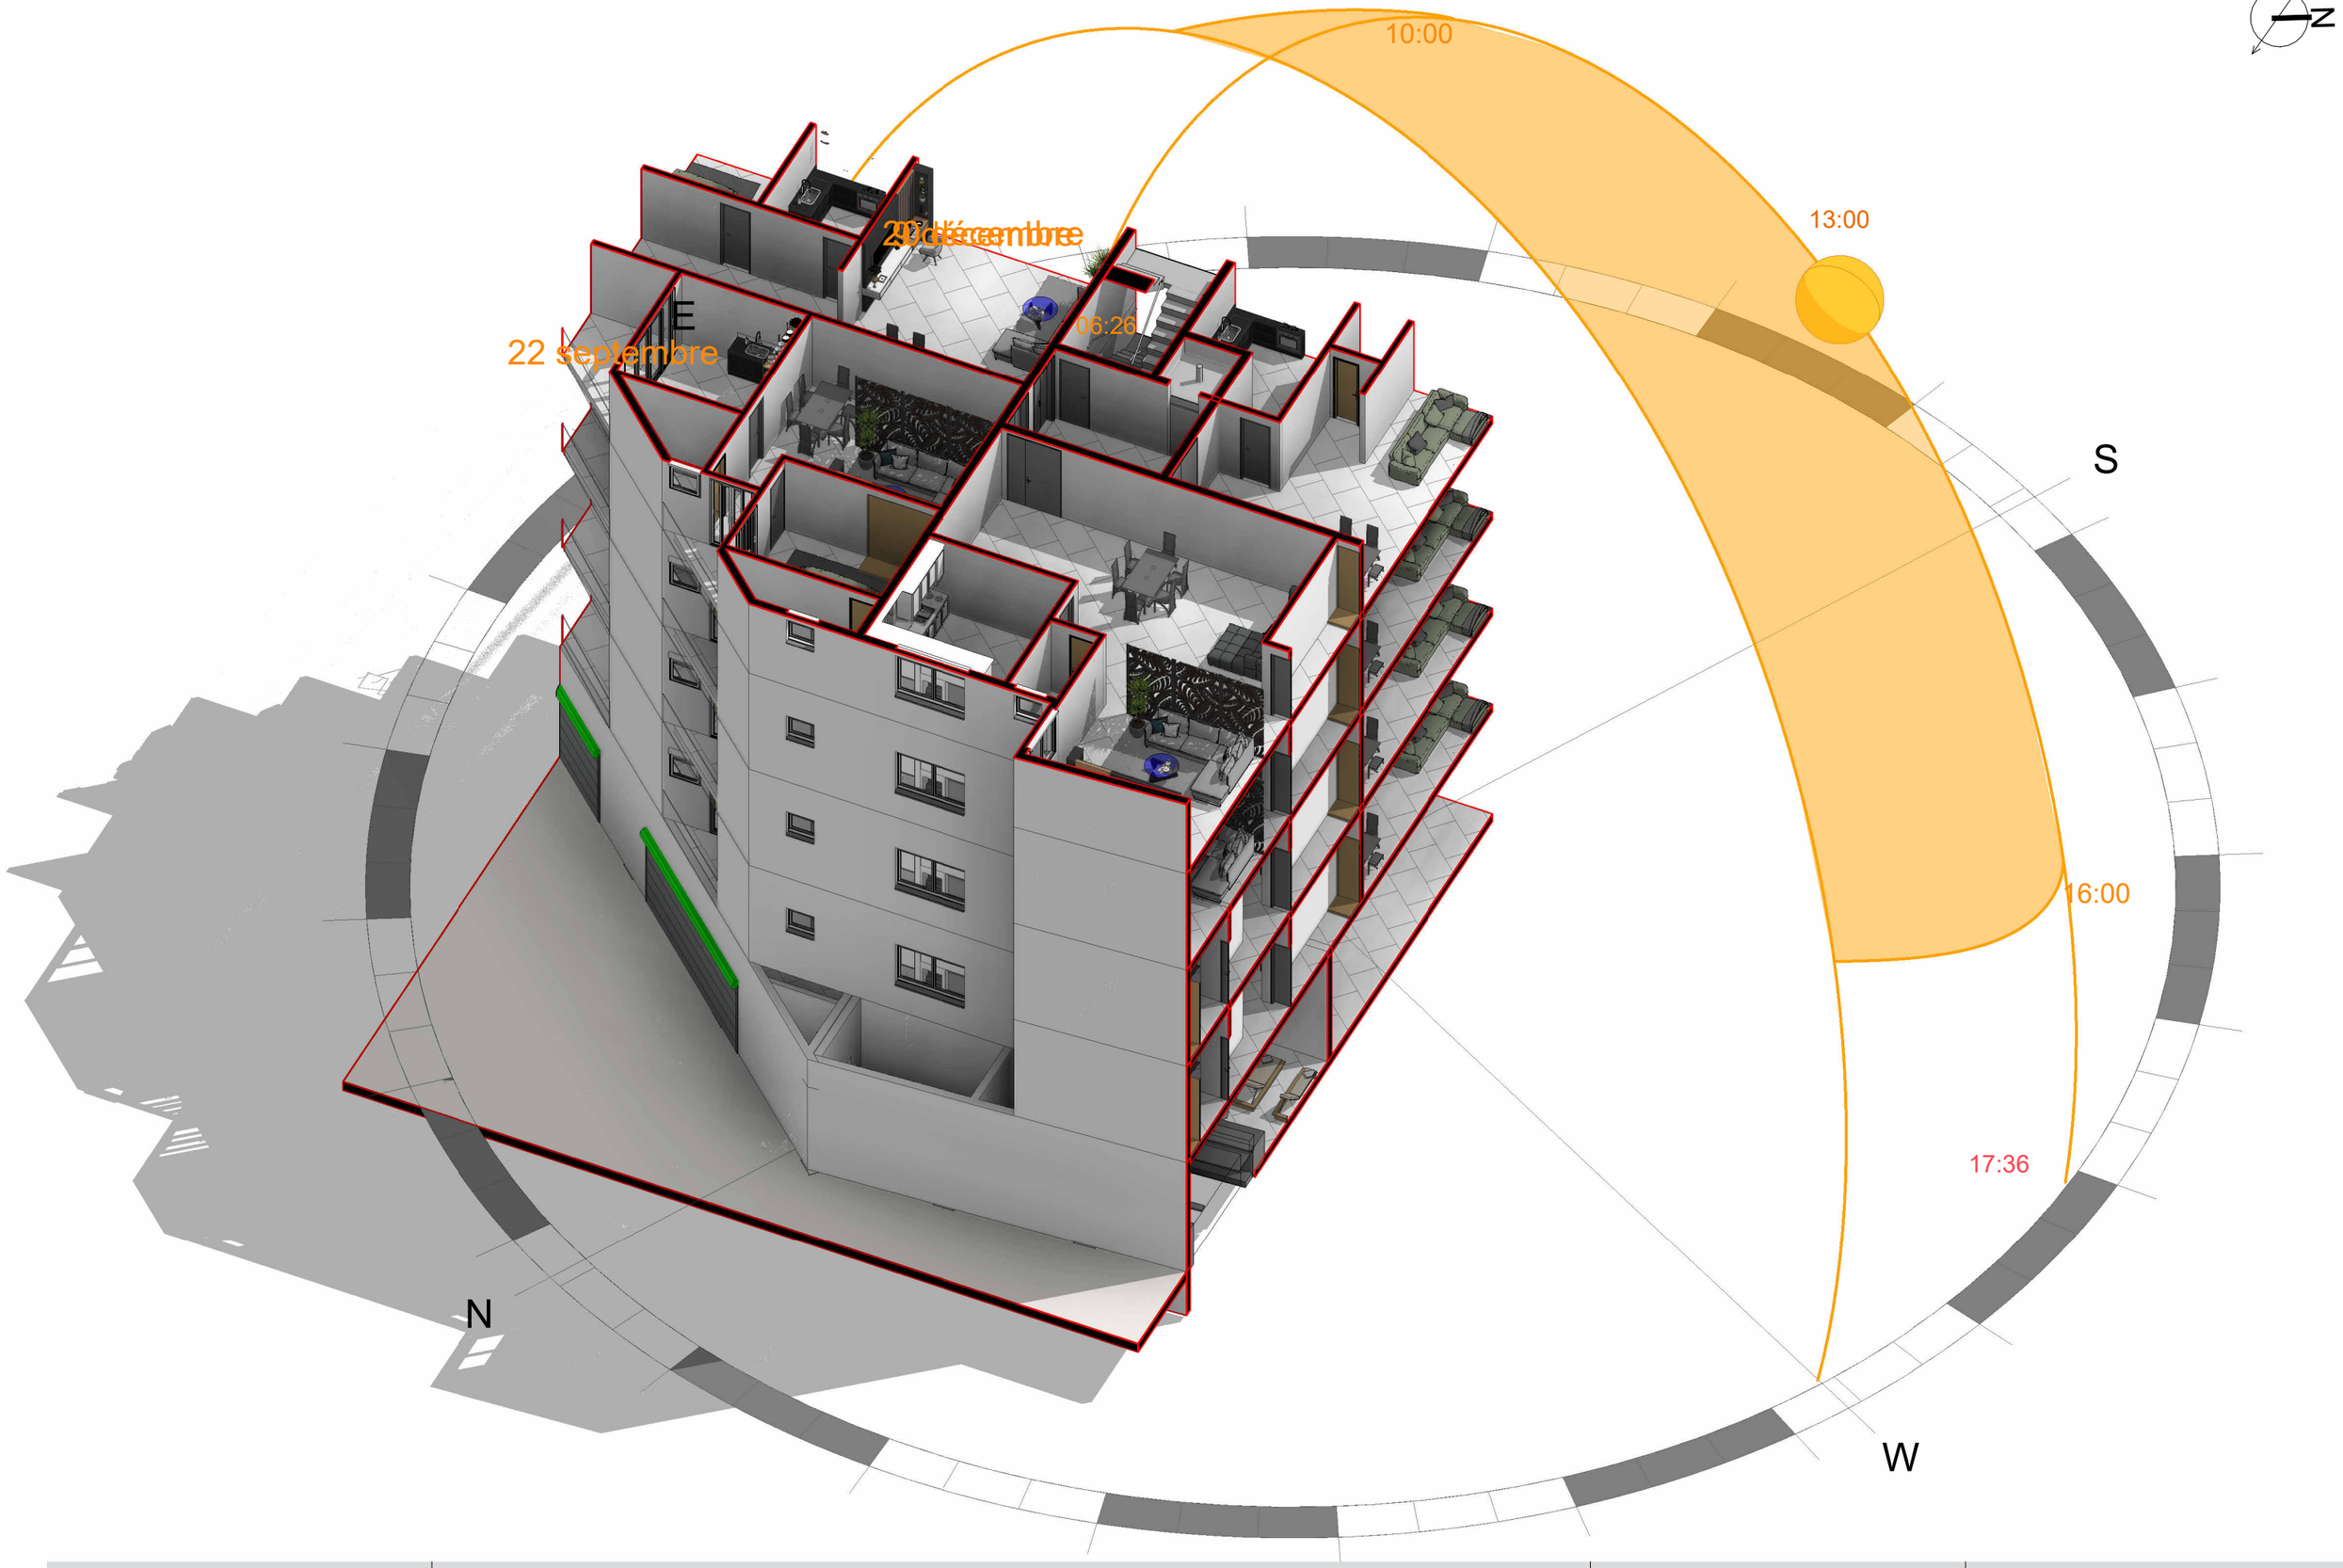

Maitre d'Ouvrage : M.RAMAU

Maitre d'Oeuvre : M.Moussa CISSÉ

Etude D'ensoleillement_AUTOMNE-13H

Echelle:

PROJET: LIFE STYLE


A-070

_ SS + 8 ETAGES _


DAKAR_ Sénégal

Date

13/04/2026 06:24:11

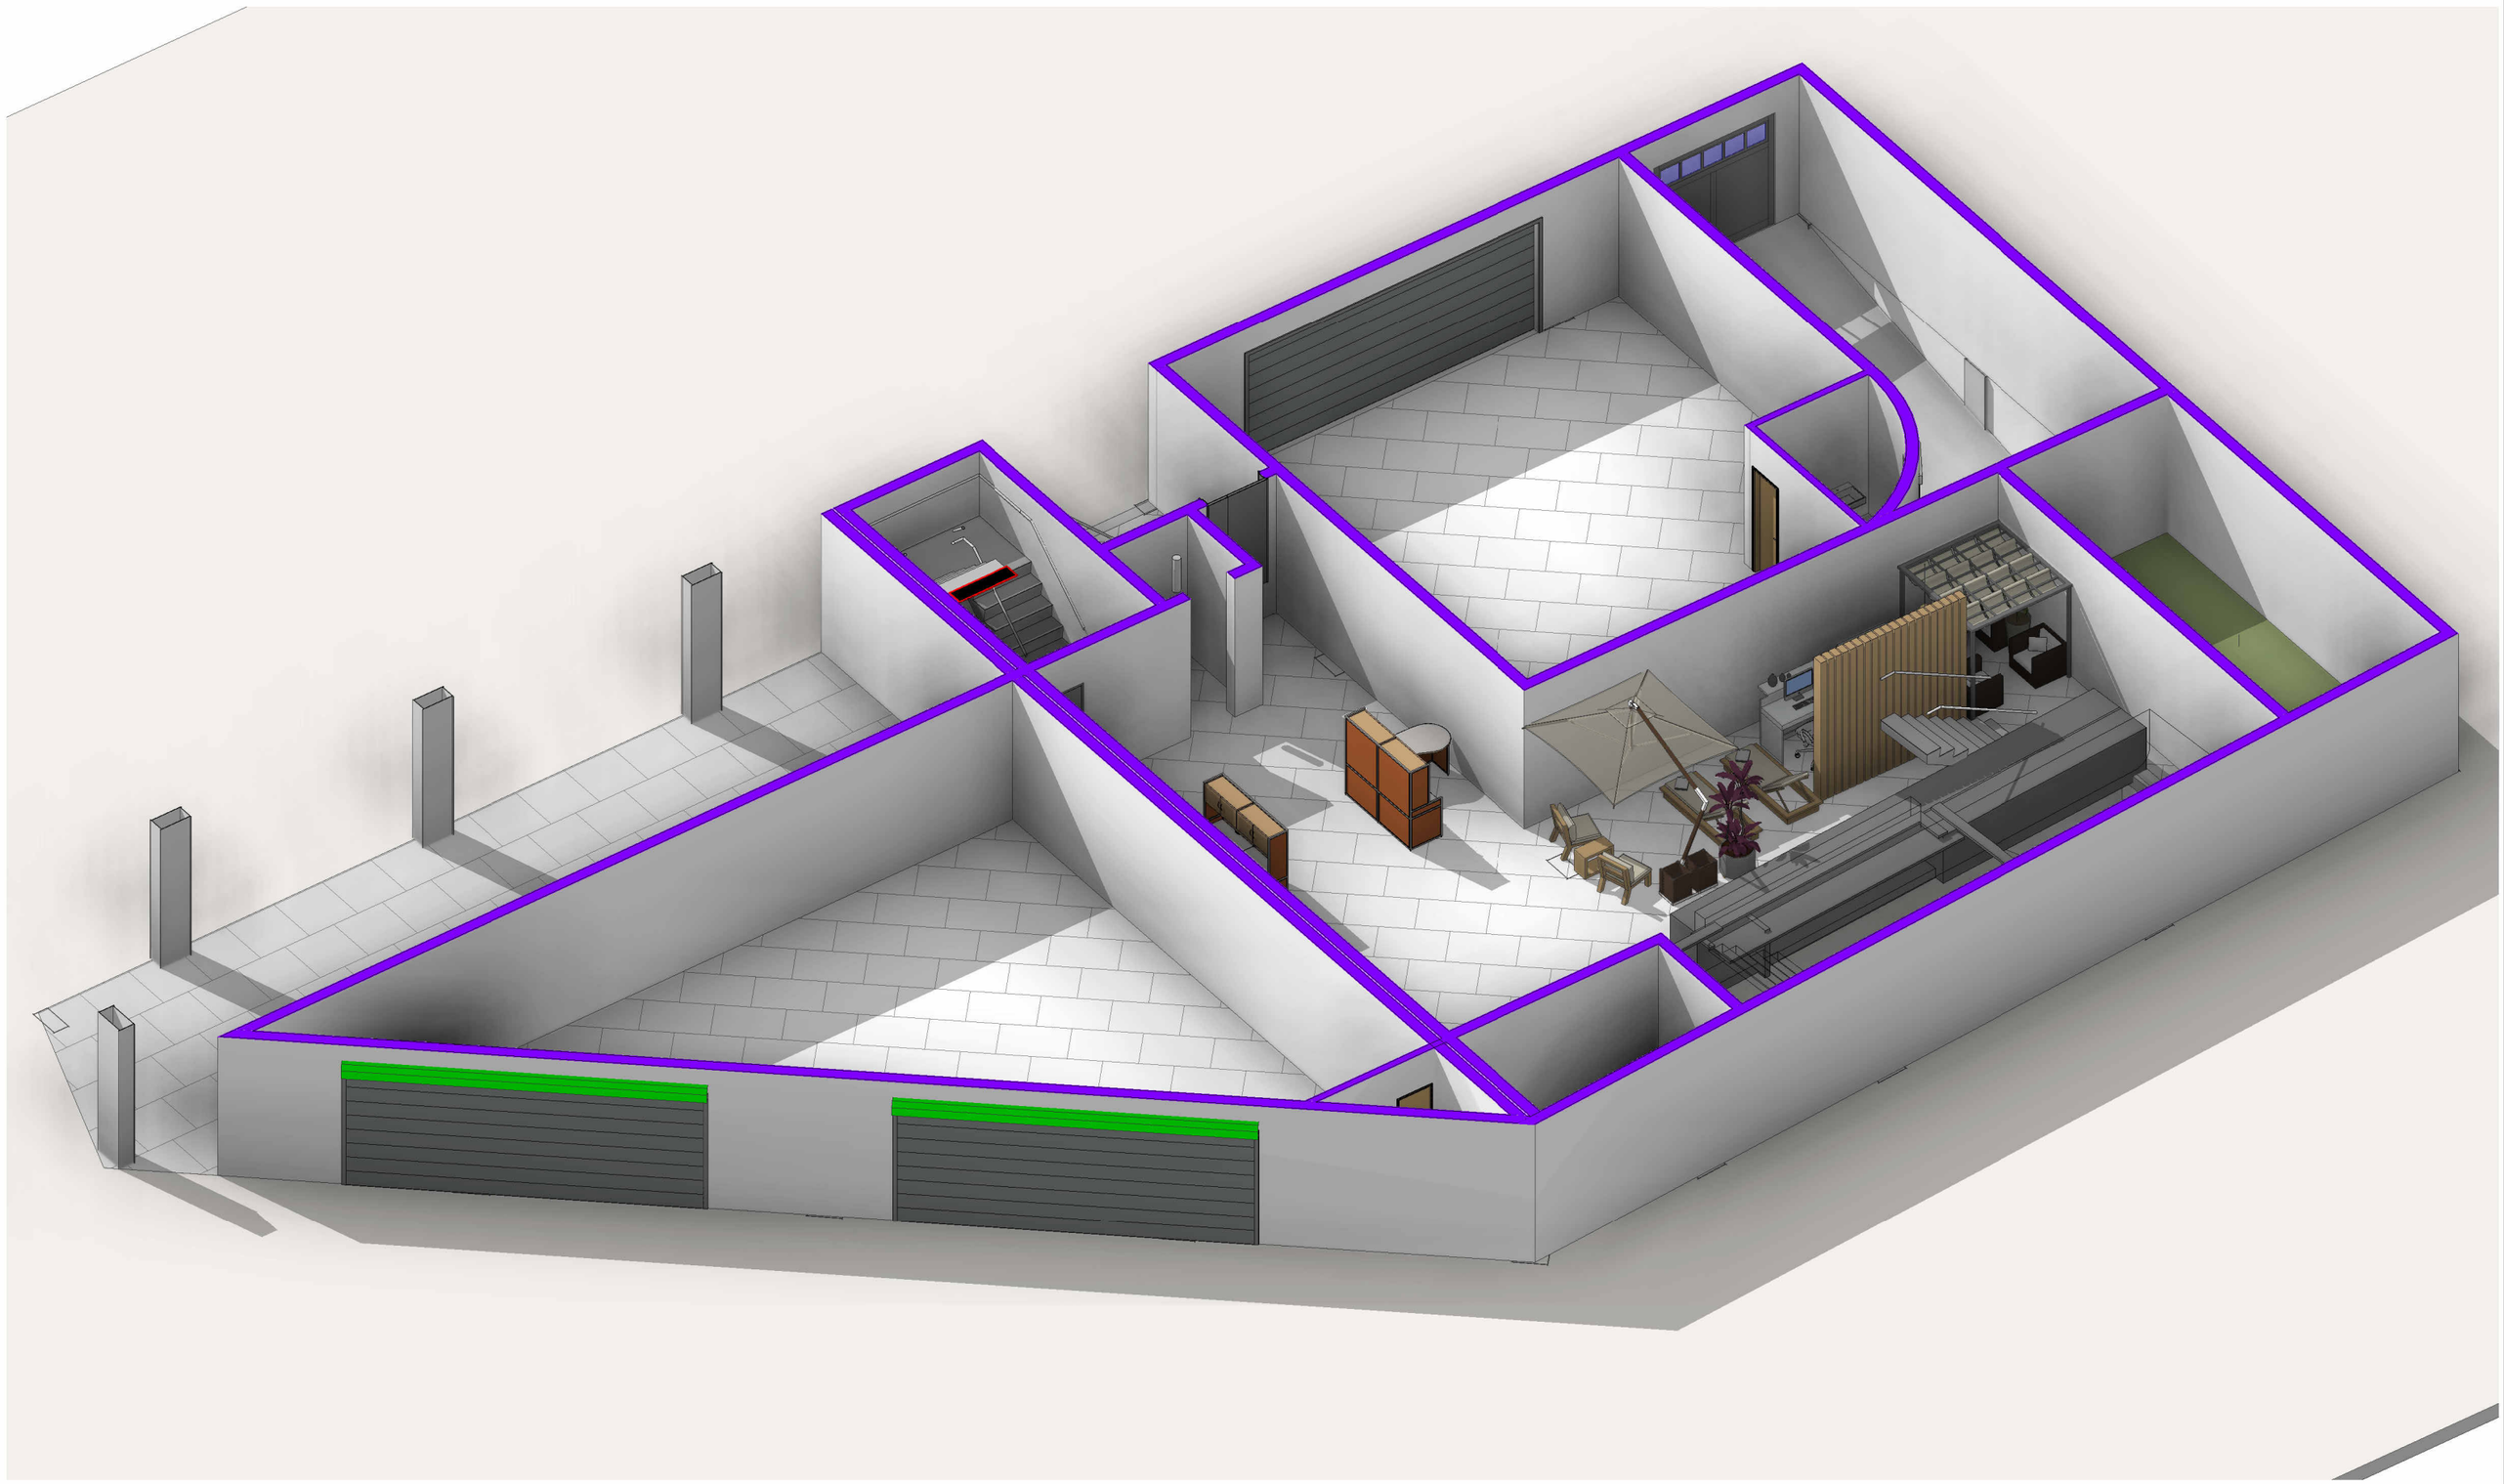

Maitre d'Ouvrage : M.RAMAU Maitre d'Oeuvre : M.Moussa CISSÉ	AXO RDC Echelle:	PROJET: LIFE STYLE	**00_15**	**_ SS + 8 ETAGES _** **DAKAR**_ Sénégal	**Date** 13/04/2026 06:24:15

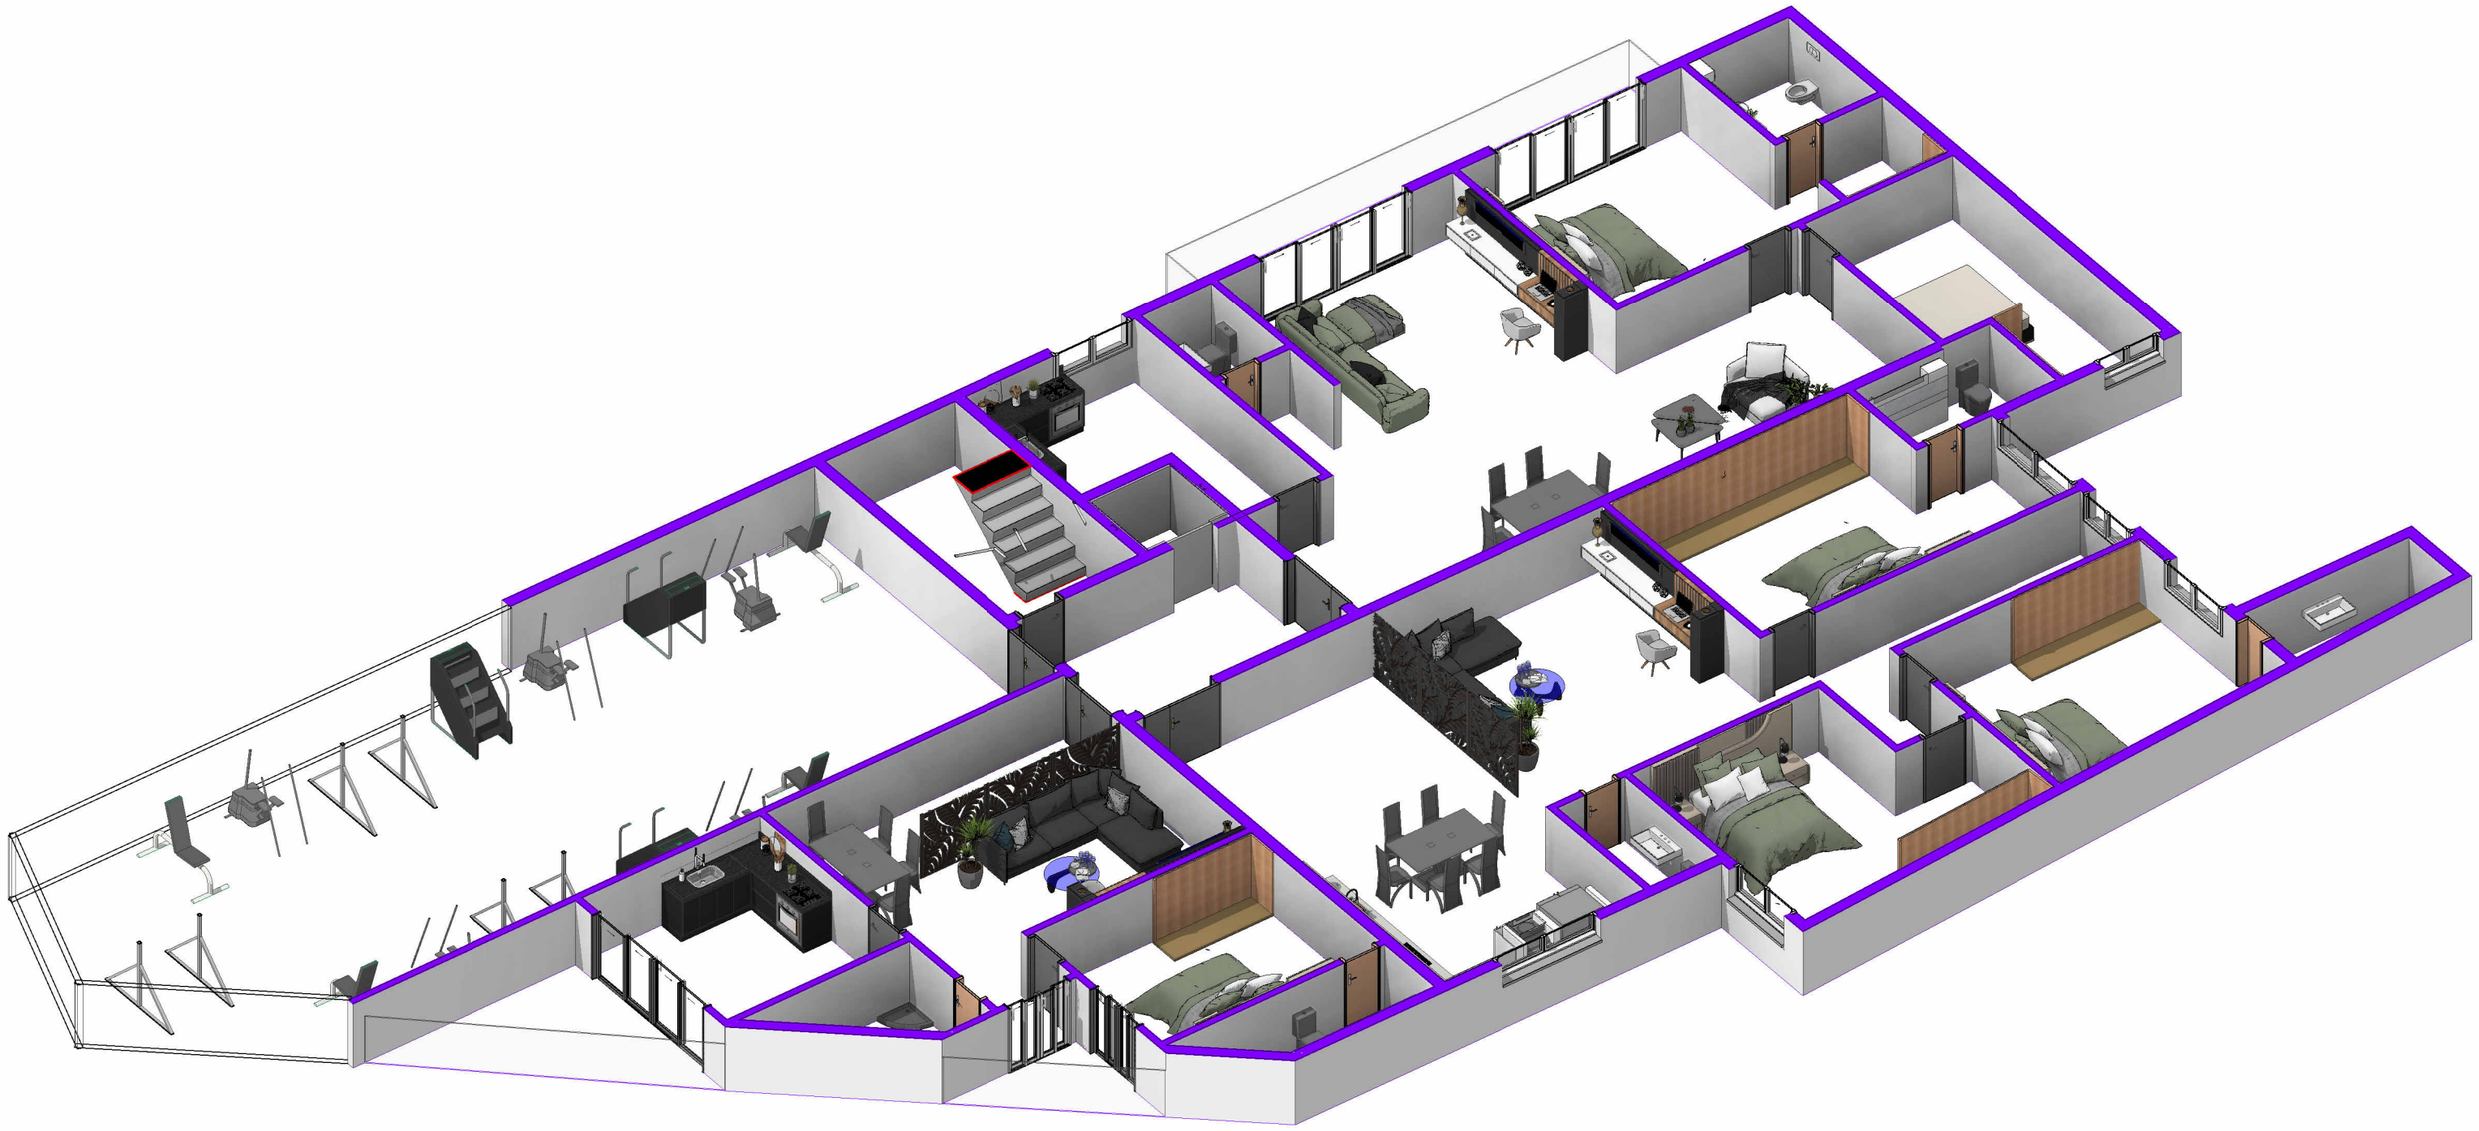

Maitre d'Ouvrage : M.RAMAU

Maitre d'Oeuvre : M.Moussa CISSÉ

AXO ETAGE 2

Echelle:

PROJET: LIFE STYLE


00_15 -

_ SS + 8 ETAGES _

DAKAR_ Sénégal

Date

13/04/2026 06:24:22

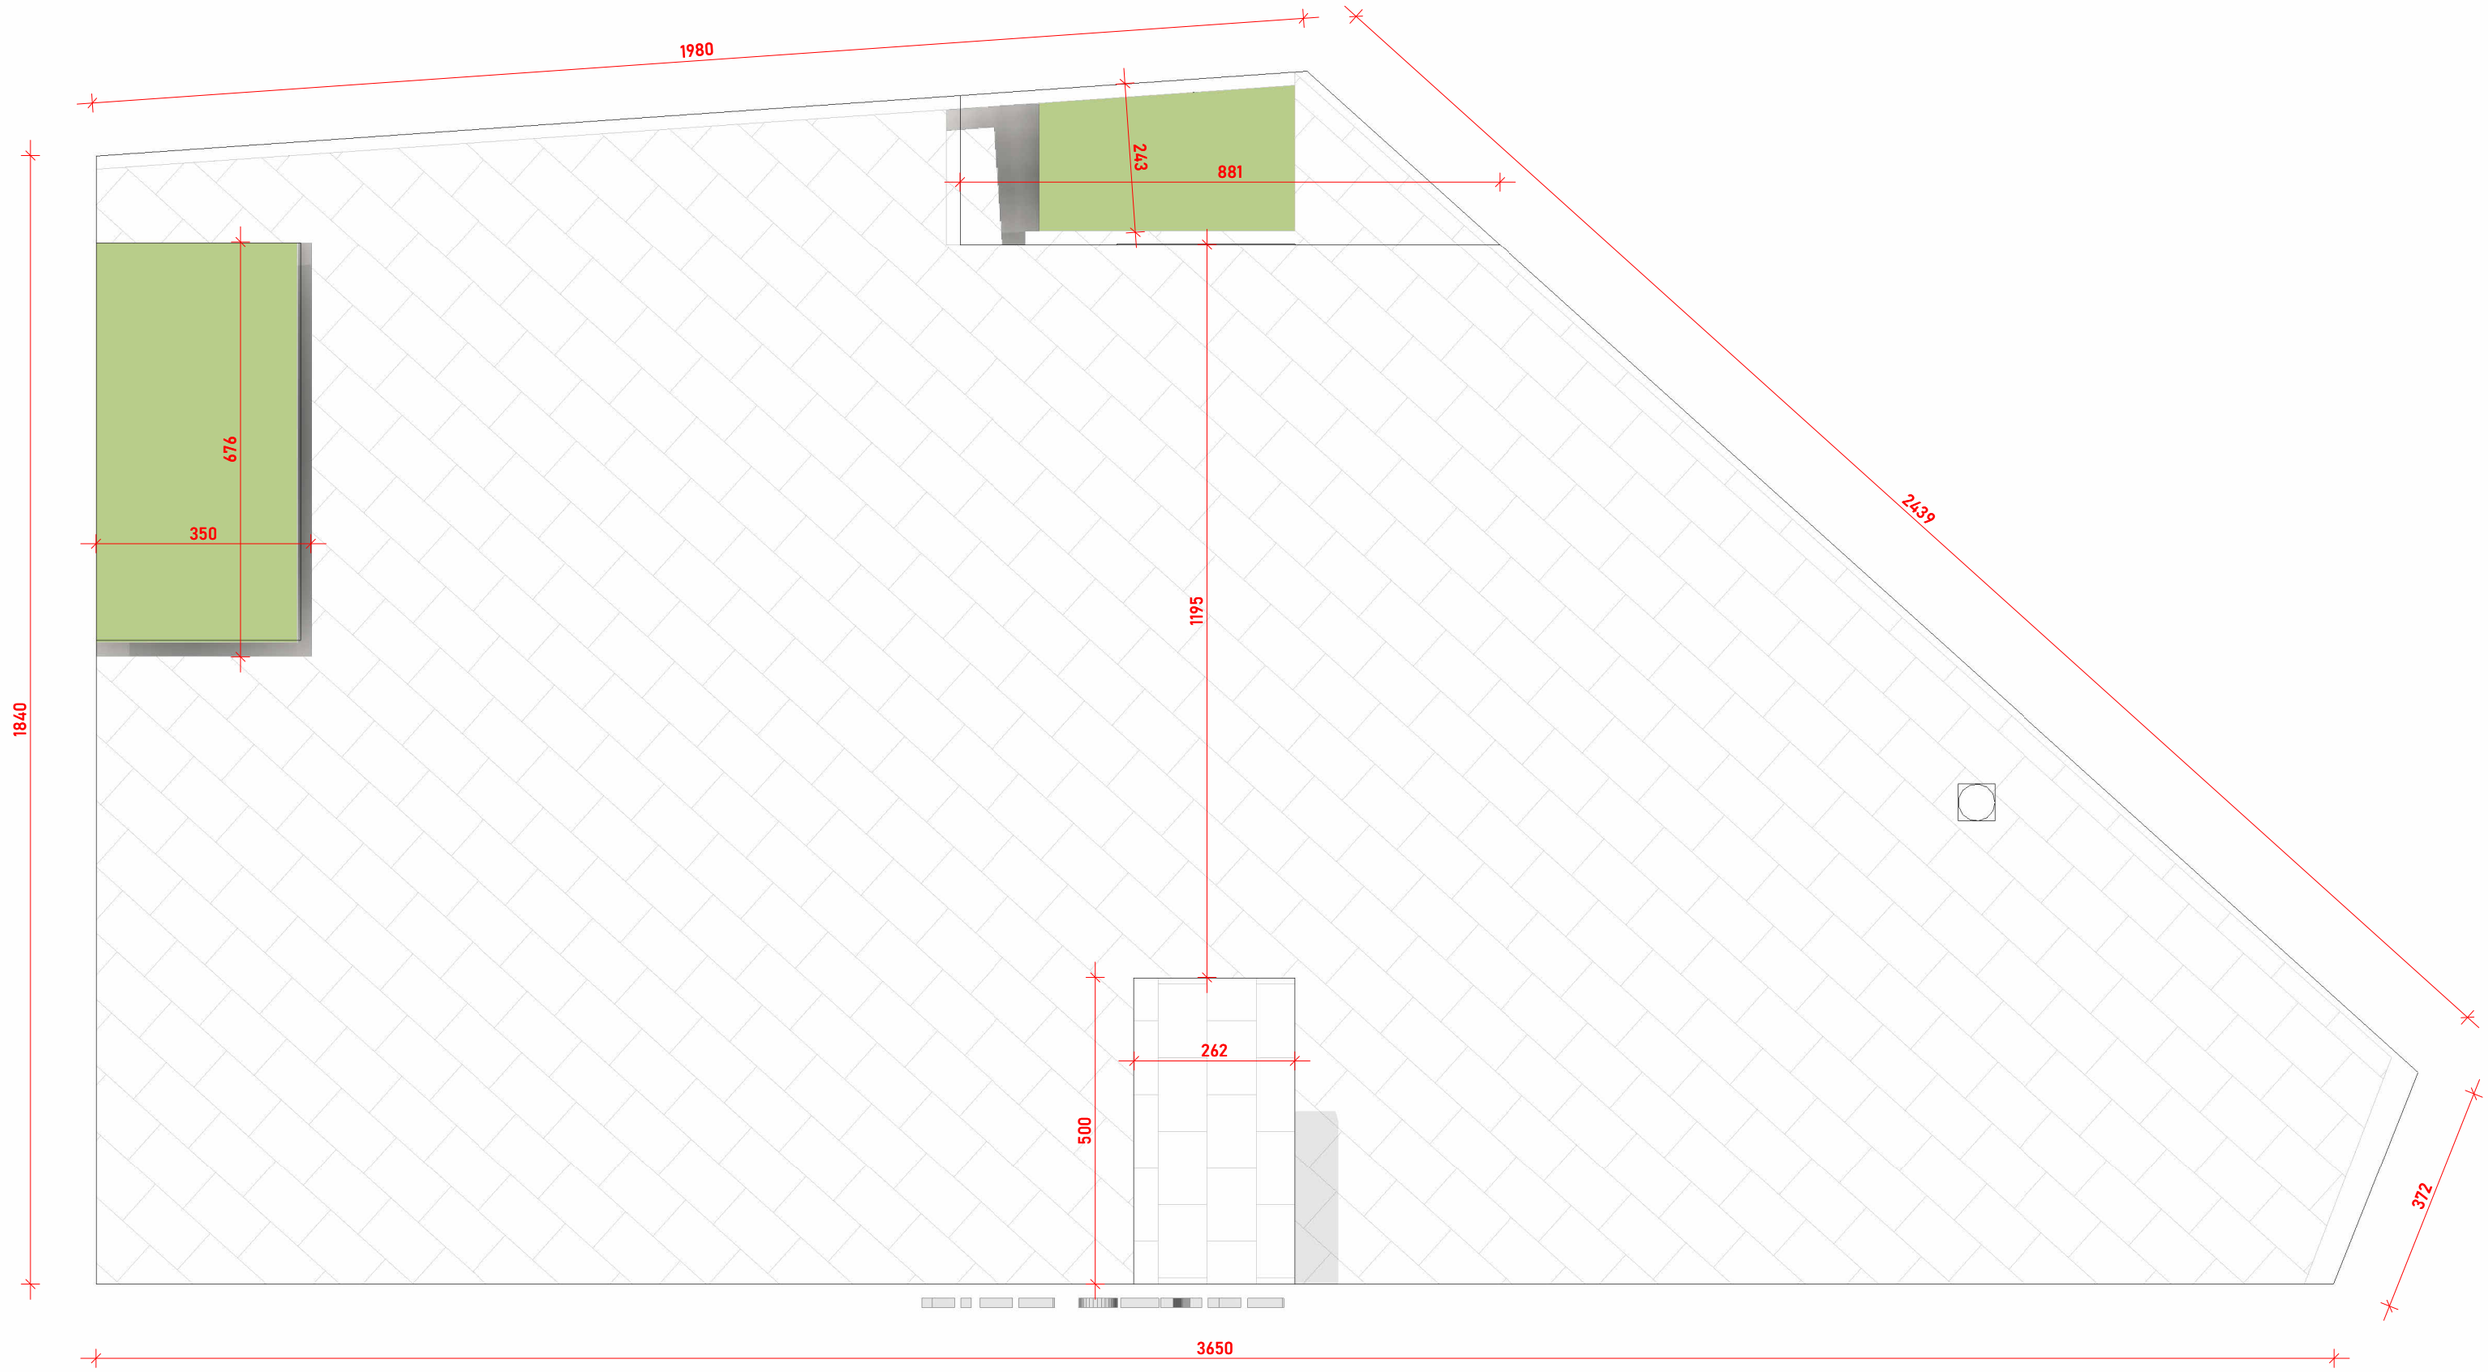

Maitre d'Ouvrage : M.RAMAU

Maitre d'Oeuvre : M.Moussa CISSÉ

PLAN DE MASSE

Echelle: **1 : 100**

PROJET: LIFE STYLE


00_01

_ SS + 8 ETAGES _

DAKAR_ Sénégal

Date

13/04/2026 06:24:26

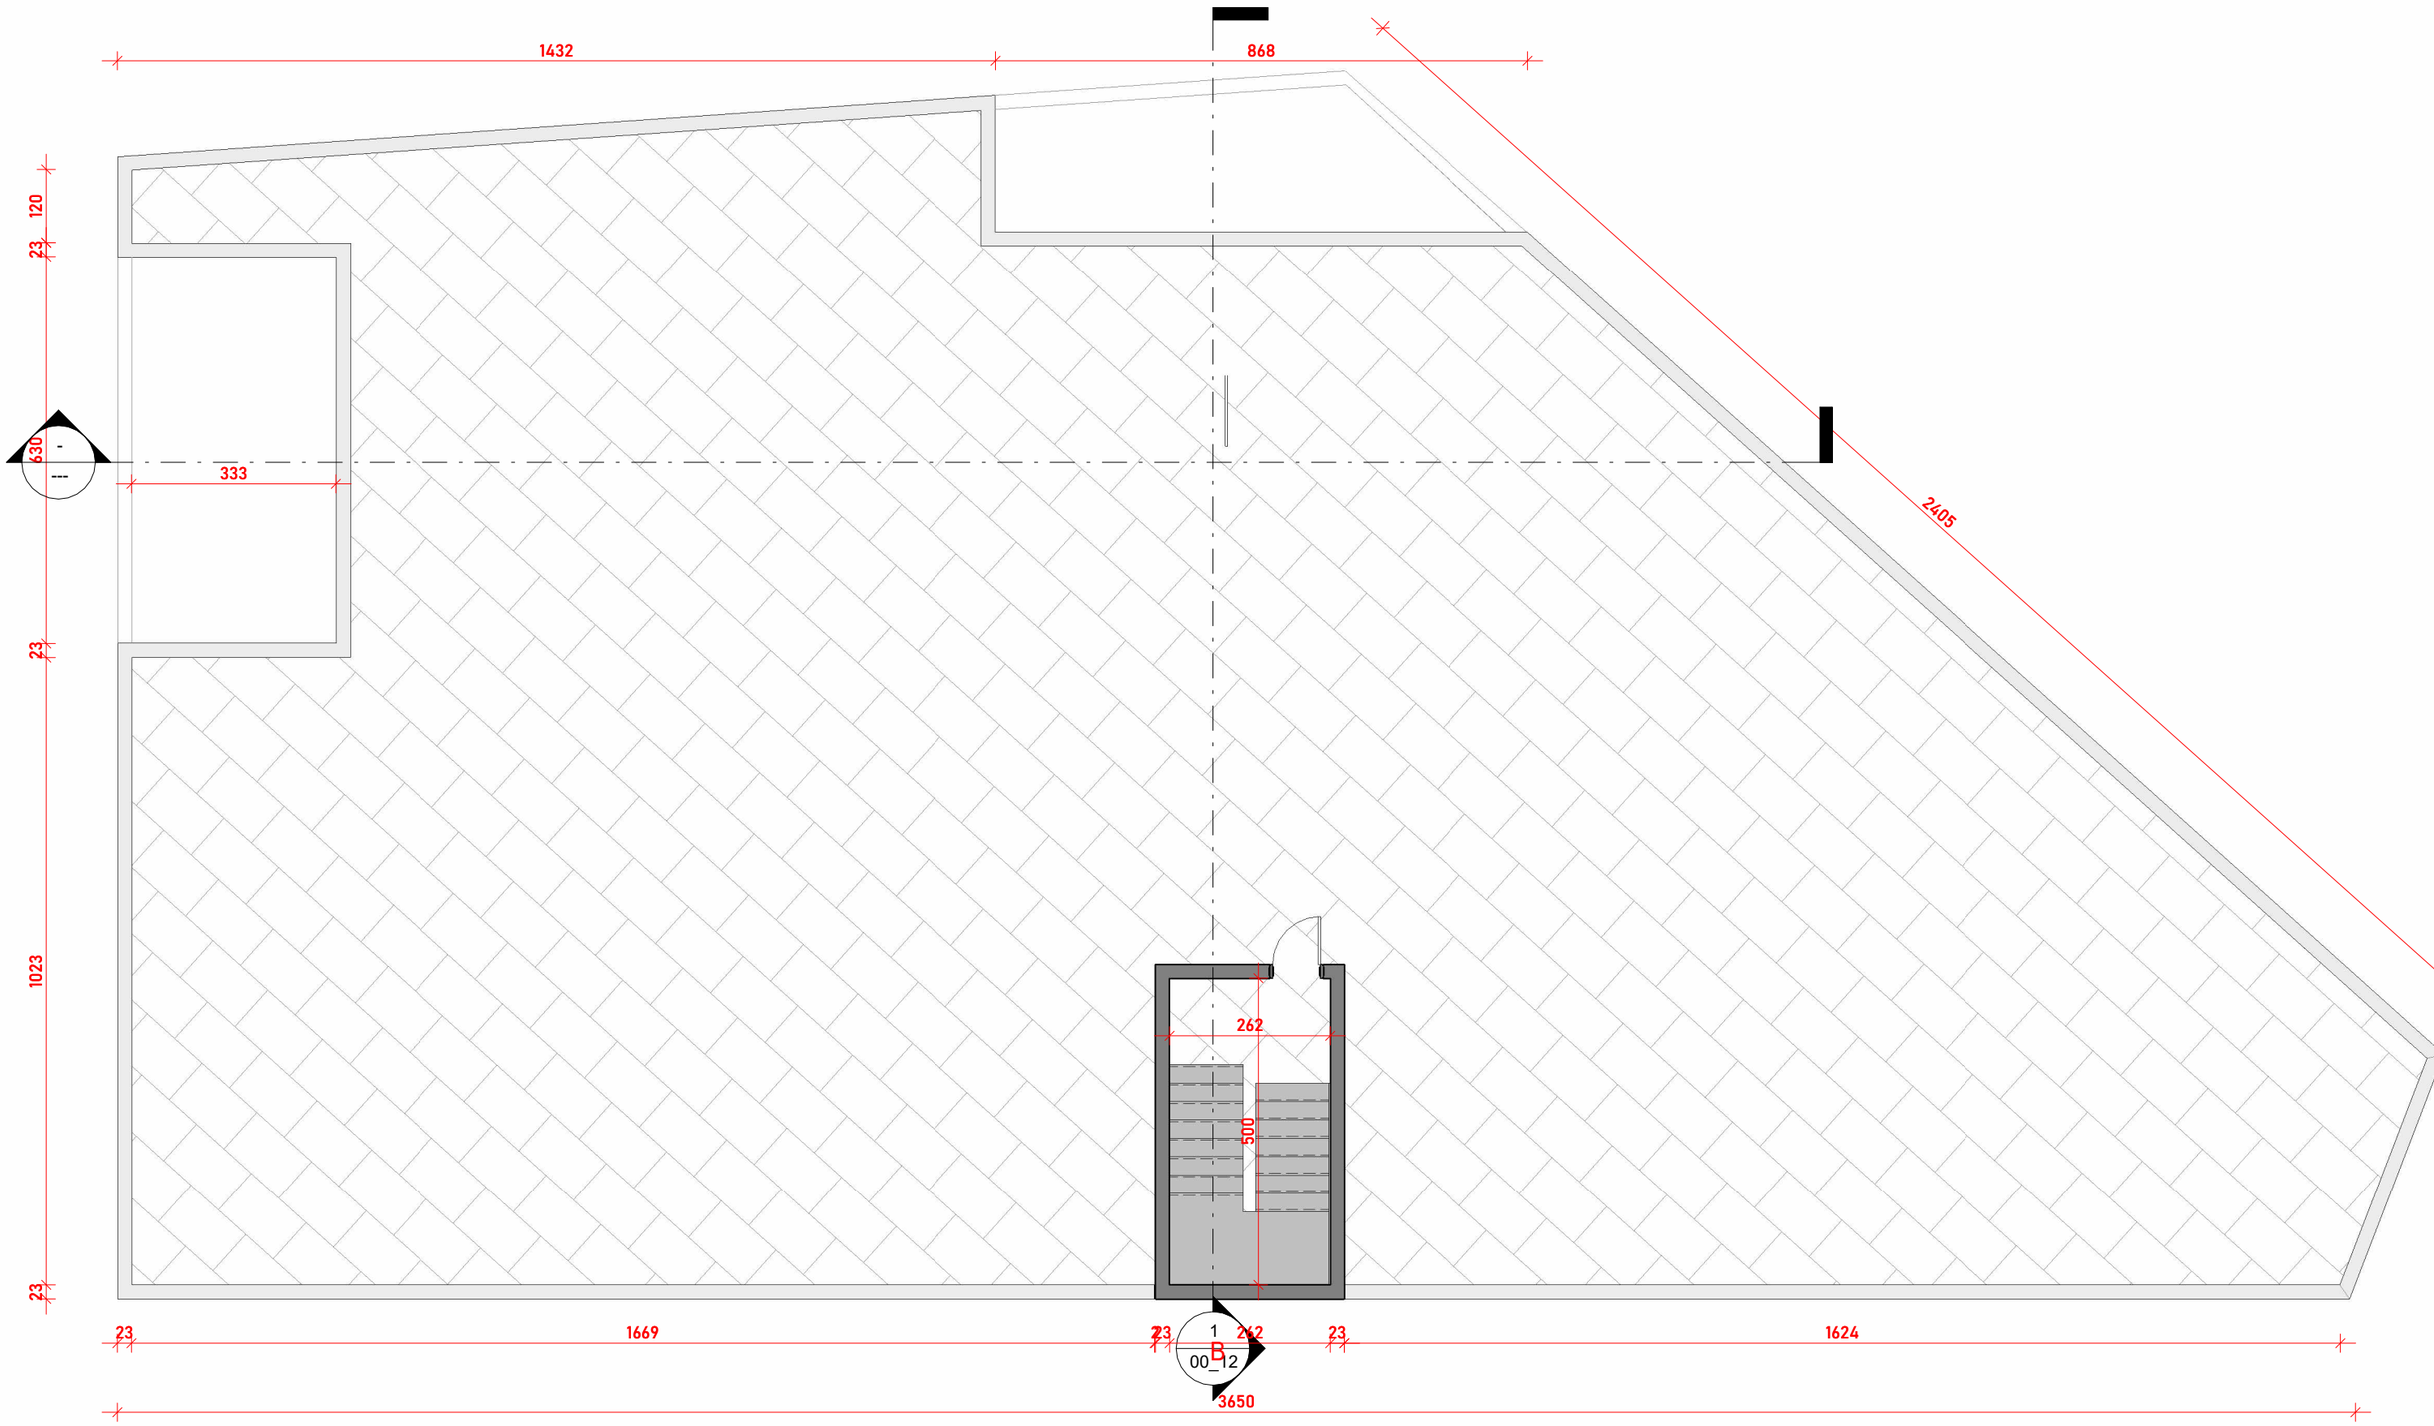

Maitre d'Ouvrage : M.RAMAU

Maitre d'Oeuvre : M.Moussa CISSÉ

TERRASSE ACCESSIBLE

Echelle: **1 : 100**

PROJET: LIFE STYLE


00_10

_ SS + 8 ETAGES _

DAKAR_ Sénégal

Date

13/04/2026 06:24:28

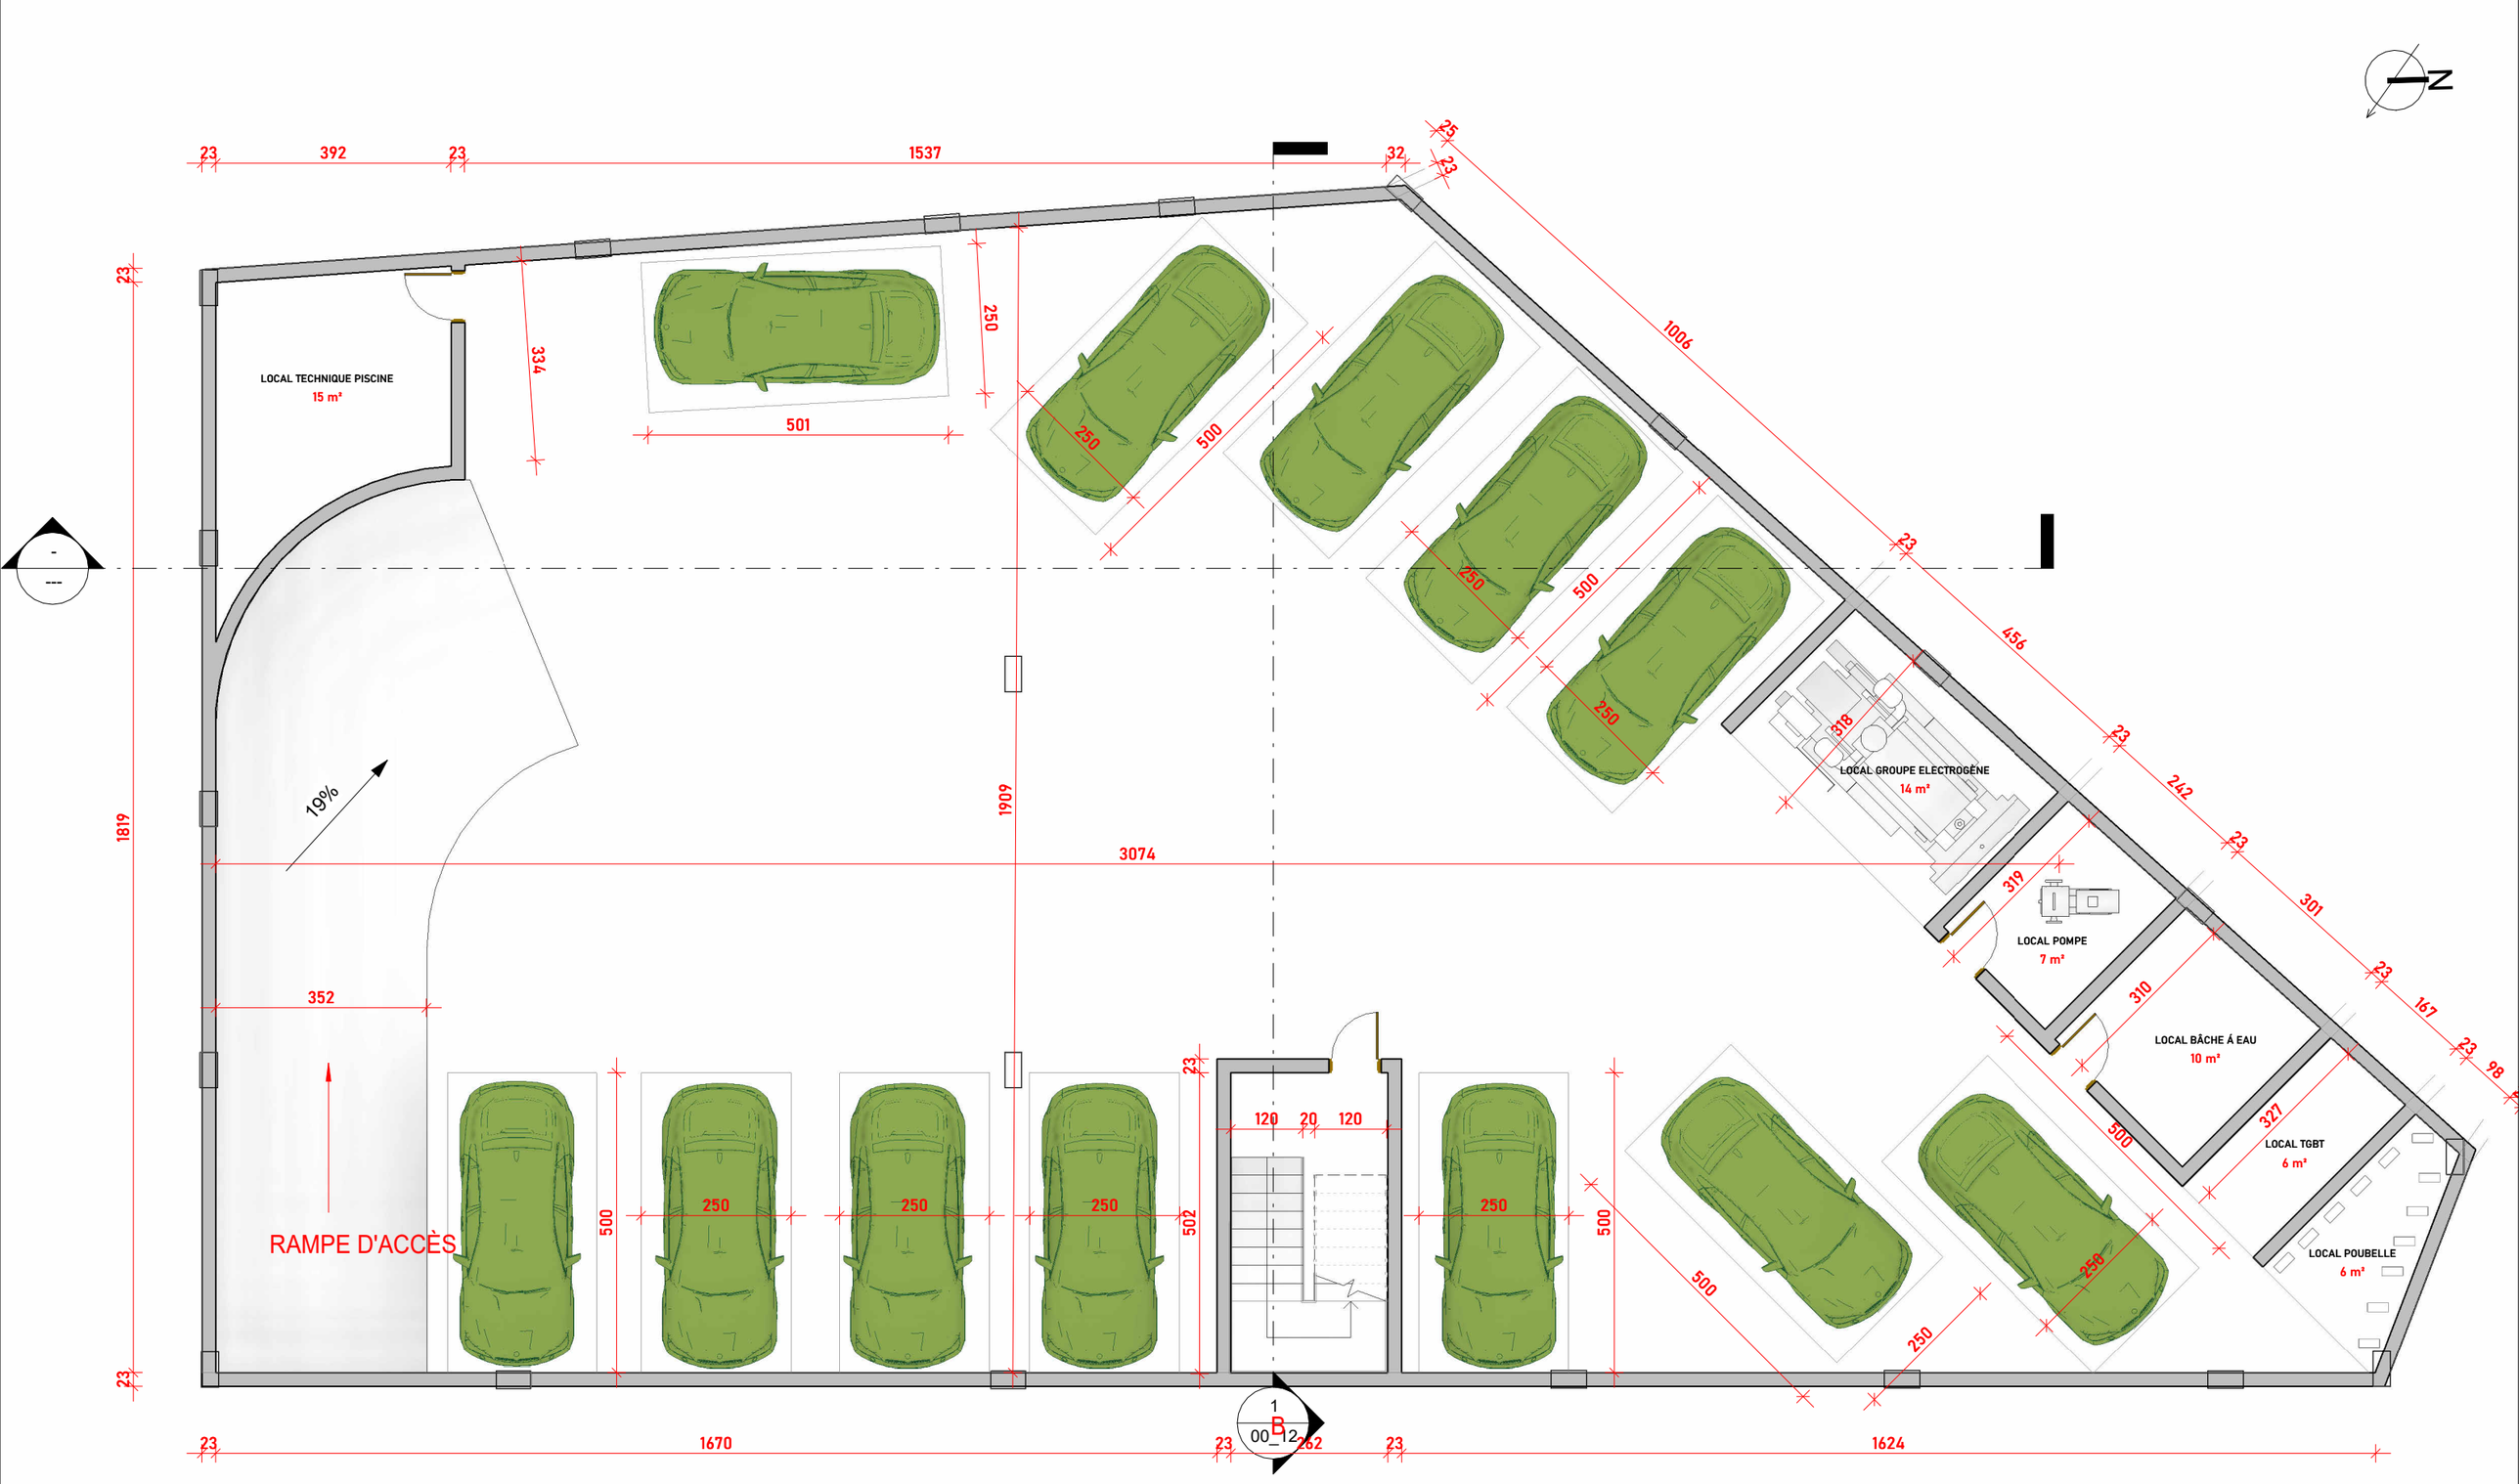

Maitre d'Ouvrage : M.RAMAU Maitre d'Oeuvre : M.Moussa CISSÉ	SOUS SOL Echelle: **1 : 100**	PROJET: LIFE STYLE	**00_02**	**_ SS + 8 ETAGES _** **DAKAR**_ Sénégal	**Date** 13/04/2026 06:24:30

PISCINE
27 m²

PATIO
9 m²

WC
3 m²

COUR
26 m²

PLAGE AMÉNAGÉE
99 m²

COMMERCE 1
107 m²

COMMERCE 2
87 m²

WC
3 m²

HALL D'ACCUEIL+ESPACE
CONCIERGE
38 m²

BAS

ENTRÉE PARKING-SOUS SOL

ACCÈS PMR

1
00_11

1
B
00_12

Maitre d'Ouvrage : M.RAMAU Maitre d'Oeuvre : M.Moussa CISSÉ	REZ DE CHAUSSEE Echelle: **1 : 100**	PROJET: LIFE STYLE	**00_03**	**_ SS + 8 ETAGES _** **DAKAR**_ Sénégal	**Date** 13/04/2026 06:24:33

SALLE D'EAU
3 m²
CHAMBRE 2
20 m²
CHAMBRE 3
21 m²
VIDE
18 m²
SALLE D'EAU
5 m²
CUISINE AMÉRICAINE
16 m²
VIDE SUR COUR
21 m²
DÉGAGEMENT
12 m²
CHAMBRE
15 m²
LOGGIA
3 m²
SALLE D'EAU
5 m²
SÉJOUR
49 m²
CHAMBRE PRINCIPALE
24 m²
SALLE DE BAIN
5 m²
SÉJOUR
32 m²
CUISINE
14 m²
LOGGIA
9 m²
F4
F2
F3
HALL
16 m²
CHAMBRE 2
15 m²
SÉOUR
68 m²
DRESSING
4 m²
CHAMBRE 1
20 m²
SALLE D'EAU
5 m²
SALLE D'EAU
3 m²
CUISINE
14 m²
TERRASSE
115 m²
BALCON
11 m²
1
B
00_12

Maitre d'Ouvrage : M.RAMAU

Maitre d'Oeuvre : M.Moussa CISSÉ

ETAGE 1

Echelle: **1 : 100**

PROJET: LIFE STYLE


00_04

_ SS + 8 ETAGES _

DAKAR_ Sénégal

Date

13/04/2026 06:24:55

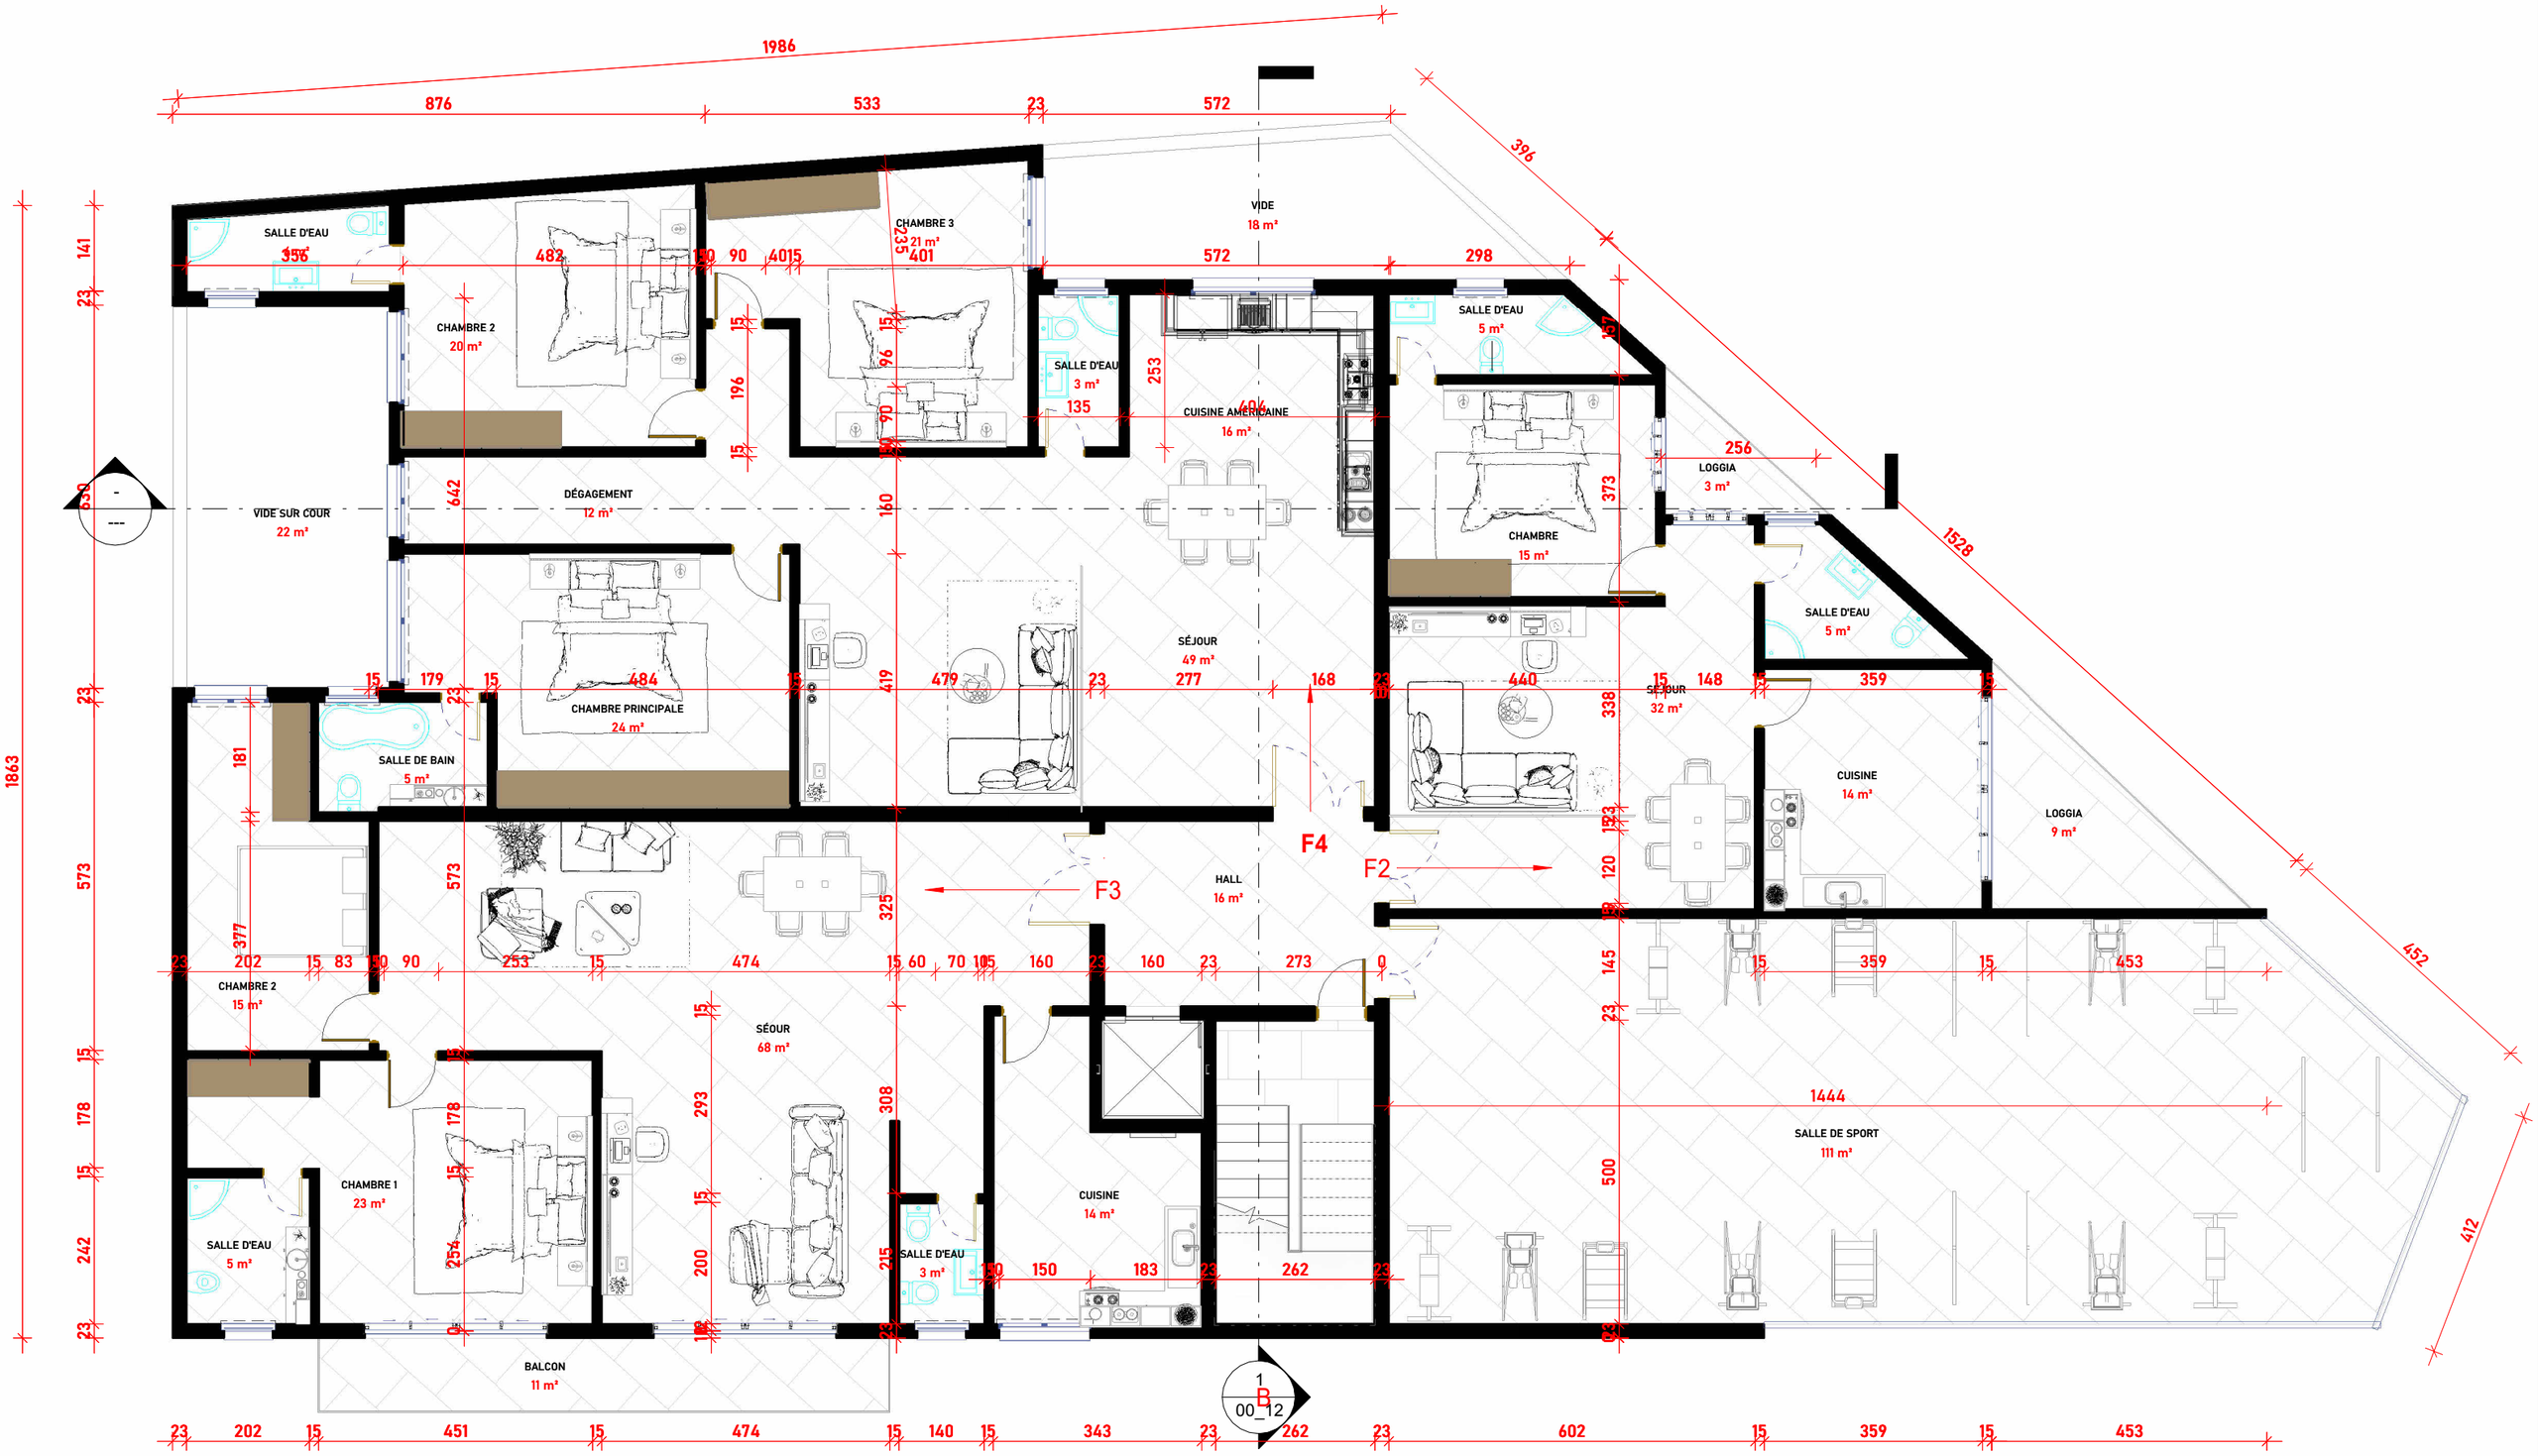

Maitre d'Ouvrage : M.RAMAU

Maitre d'Oeuvre : M.Moussa CISSÉ

ETAGE 2

Echelle: **1 : 100**

PROJET: LIFE STYLE

00_05

_ SS + 8 ETAGES _

DAKAR_ Sénégal

Date

13/04/2026 06:25:16

SALLE D'EAU
3 m²
CHAMBRE 2
20 m²
VIDE
18 m²
SALLE D'EAU
3 m²
CUISINE
16 m²
SALLE D'EAU
5 m²
LOGGIA
3 m²
VIDE SUR COUR
22 m²
DÉGAGEMENT
7 m²
SÉJOUR
76 m²
CHAMBRE
15 m²
SALLE D'EAU
5 m²
CHAMBRE PRINCIPALE
24 m²
SALLE DE BAIN
5 m²
SÉJOUR
32 m²
CUISINE
14 m²
LOGGIA
9 m²
F3
F2
HALL
16 m²
CHAMBRE 2
15 m²
SÉJOUR
68 m²
CUISINE
14 m²
SALLE D'EAU
3 m²
SÉJOUR
65 m²
CUISINE
10 m²
CHAMBRE
18 m²
SALLE D'EAU
3 m²
321
DRESSING
4 m²
CHAMBRE 1
23 m²
SALLE D'EAU
5 m²
SALLE D'EAU
5 m²
BALCON
11 m²
BALCON
7 m²
BALCON
6 m²
1
B
00_12

1986 350 29 482 548 23 572 396 223 368 355 601 459 380
141 23 630 23 573 15 178 15 242 23
482 533 135 427 298 256 359 456 279 202 451 474 140 343 262 602 450 200
199 253 642 160 373 691 484 179 419 479 277 168 440 148 338 181 377 325 293 308 254 215 321 500 361 120 145 123

Maitre d'Ouvrage : M.RAMAU
Maitre d'Oeuvre : M.Moussa CISSÉ

ETAGE 3&4
Echelle: **1 : 100**

PROJET: LIFE STYLE

00_06

_ SS + 8 ETAGES _
DAKAR_ Sénégal

Date
13/04/2026 06:25:45

SALLE D'EAU
3 m²
CHAMBRE 2
20 m²
CHAMRE 3
21 m²
VIDE
18 m²
SALLE D'EAU
3 m²
CUISINE
16 m²
SALLE D'EAU
5 m²
VIDE SUR COUR
22 m²
DÉGAGEMENT
7 m²
CHAMBRE
15 m²
LOGGIA
3 m²
SÉJOUR
54 m²
SALLE D'EAU
5 m²
CHAMBRE PRINCIPALE
24 m²
SALLE DE BAIN
5 m²
SÉJOUR
32 m²
CUISINE
14 m²
LOGGIA
9 m²
F4
F2
F3
F2
CHAMBRE 2
15 m²
SÉJOUR
68 m²
SALLE D'EAU
3 m²
SÉJOUR
65 m²
CHAMBRE 1
23 m²
SALLE D'EAU
5 m²
CUISINE
14 m²
SALLE D'EAU
3 m²
CUISINE
10 m²
CHAMBRE
23 m²
SALLE D'EAU
5 m²
BALCON
11 m²
BALCON
7 m²
BALCON
6 m²
1
00_B12

Maitre d'Ouvrage : M.RAMAU Maitre d'Oeuvre : M.Moussa CISSÉ	ETAGE 5&6 Echelle: **1 : 100**	PROJET: LIFE STYLE	**00_07**	**_ SS + 8 ETAGES _** **DAKAR**_ Sénégal	**Date** 13/04/2026 06:26:13

SALLE D'EAU
CHAMBRE AMI
20 m²
BUREAU
24 m²
VIDE
18 m²
VIDE SUR COUR
22 m²
SÉJOUR
93 m²
SALLE D'EAU
5 m²
CHAMBRE AMI
15 m²
LOGGIA
3 m²
SALLE D'EAU
5 m²
CUISINE AMÉRICAINE
15 m²
CUISINE AFRICAINE
14 m²
LOGGIA
9 m²
DUPLEX 2
DUPLEX 1
SÉJOUR
77 m²
SALON INVITÉ
68 m²
CUISINE AMÉRICAINE
21 m²
CUISINE
14 m²
SALLE D'EAU
3 m²
SALON INVITÉ
35 m²
BALCON
11 m²
BALCON
6 m²
1
00_12
B

1986 350 29 482 548 23 572 396 579 353 615 460 405 187
1863 1023 141 23 20 23 23
199 253 482 533 0 157 0 435 298 253 134 350 463 330 359 172 120 232 691 500 262 308 215 451 500 71 15
23 67 200 67 23 312 15 474 15 60 70 105 160 23 160 23 273 0 15 359 15 668 15 474 15 140 15 343 23 262 23 602 15 359 15 457

Maitre d'Ouvrage : M.RAMAU
Maitre d'Oeuvre : M.Moussa CISSÉ

ETAGE 7
Echelle: **1 : 100**

PROJET: LIFE STYLE


00_08

_ SS + 8 ETAGES _
DAKAR_ Sénégal

Date
13/04/2026 06:26:38

SALLE D'EAU
3 m²
CHAMBRE 2
20 m²
CHAMRE 3
21 m²
VIDE
18 m²
VIDE SUR COUR
22 m²
CHAMRE PRINCIPALE
40 m²
SALLE DE BAN
10 m²
LOGGIA
3 m²
CHAMBRE PRINCIPALE
43 m²
SALLE D'EAU
5 m²
CHAMBRE 1
14 m²
LOGGIA
9 m²
SALLE DE BAIN
15 m²
TERRASSE
120 m²
DUPLEX 2
DUPLEX 1
ESPACE FAFILIAL
51 m²
CHAMBRE 2
14 m²
SALLE D'EAU
3 m²
TERRASSE
42 m²
1
00_12
R+2

Maitre d'Ouvrage : M.RAMAU Maitre d'Oeuvre : M.Moussa CISSÉ	ETAGE 8 Echelle: **1 : 100**	PROJET: LIFE STYLE	**00_09**	**_ SS + 8 ETAGES _** **DAKAR**_ Sénégal	**Date** 13/04/2026 06:26:42

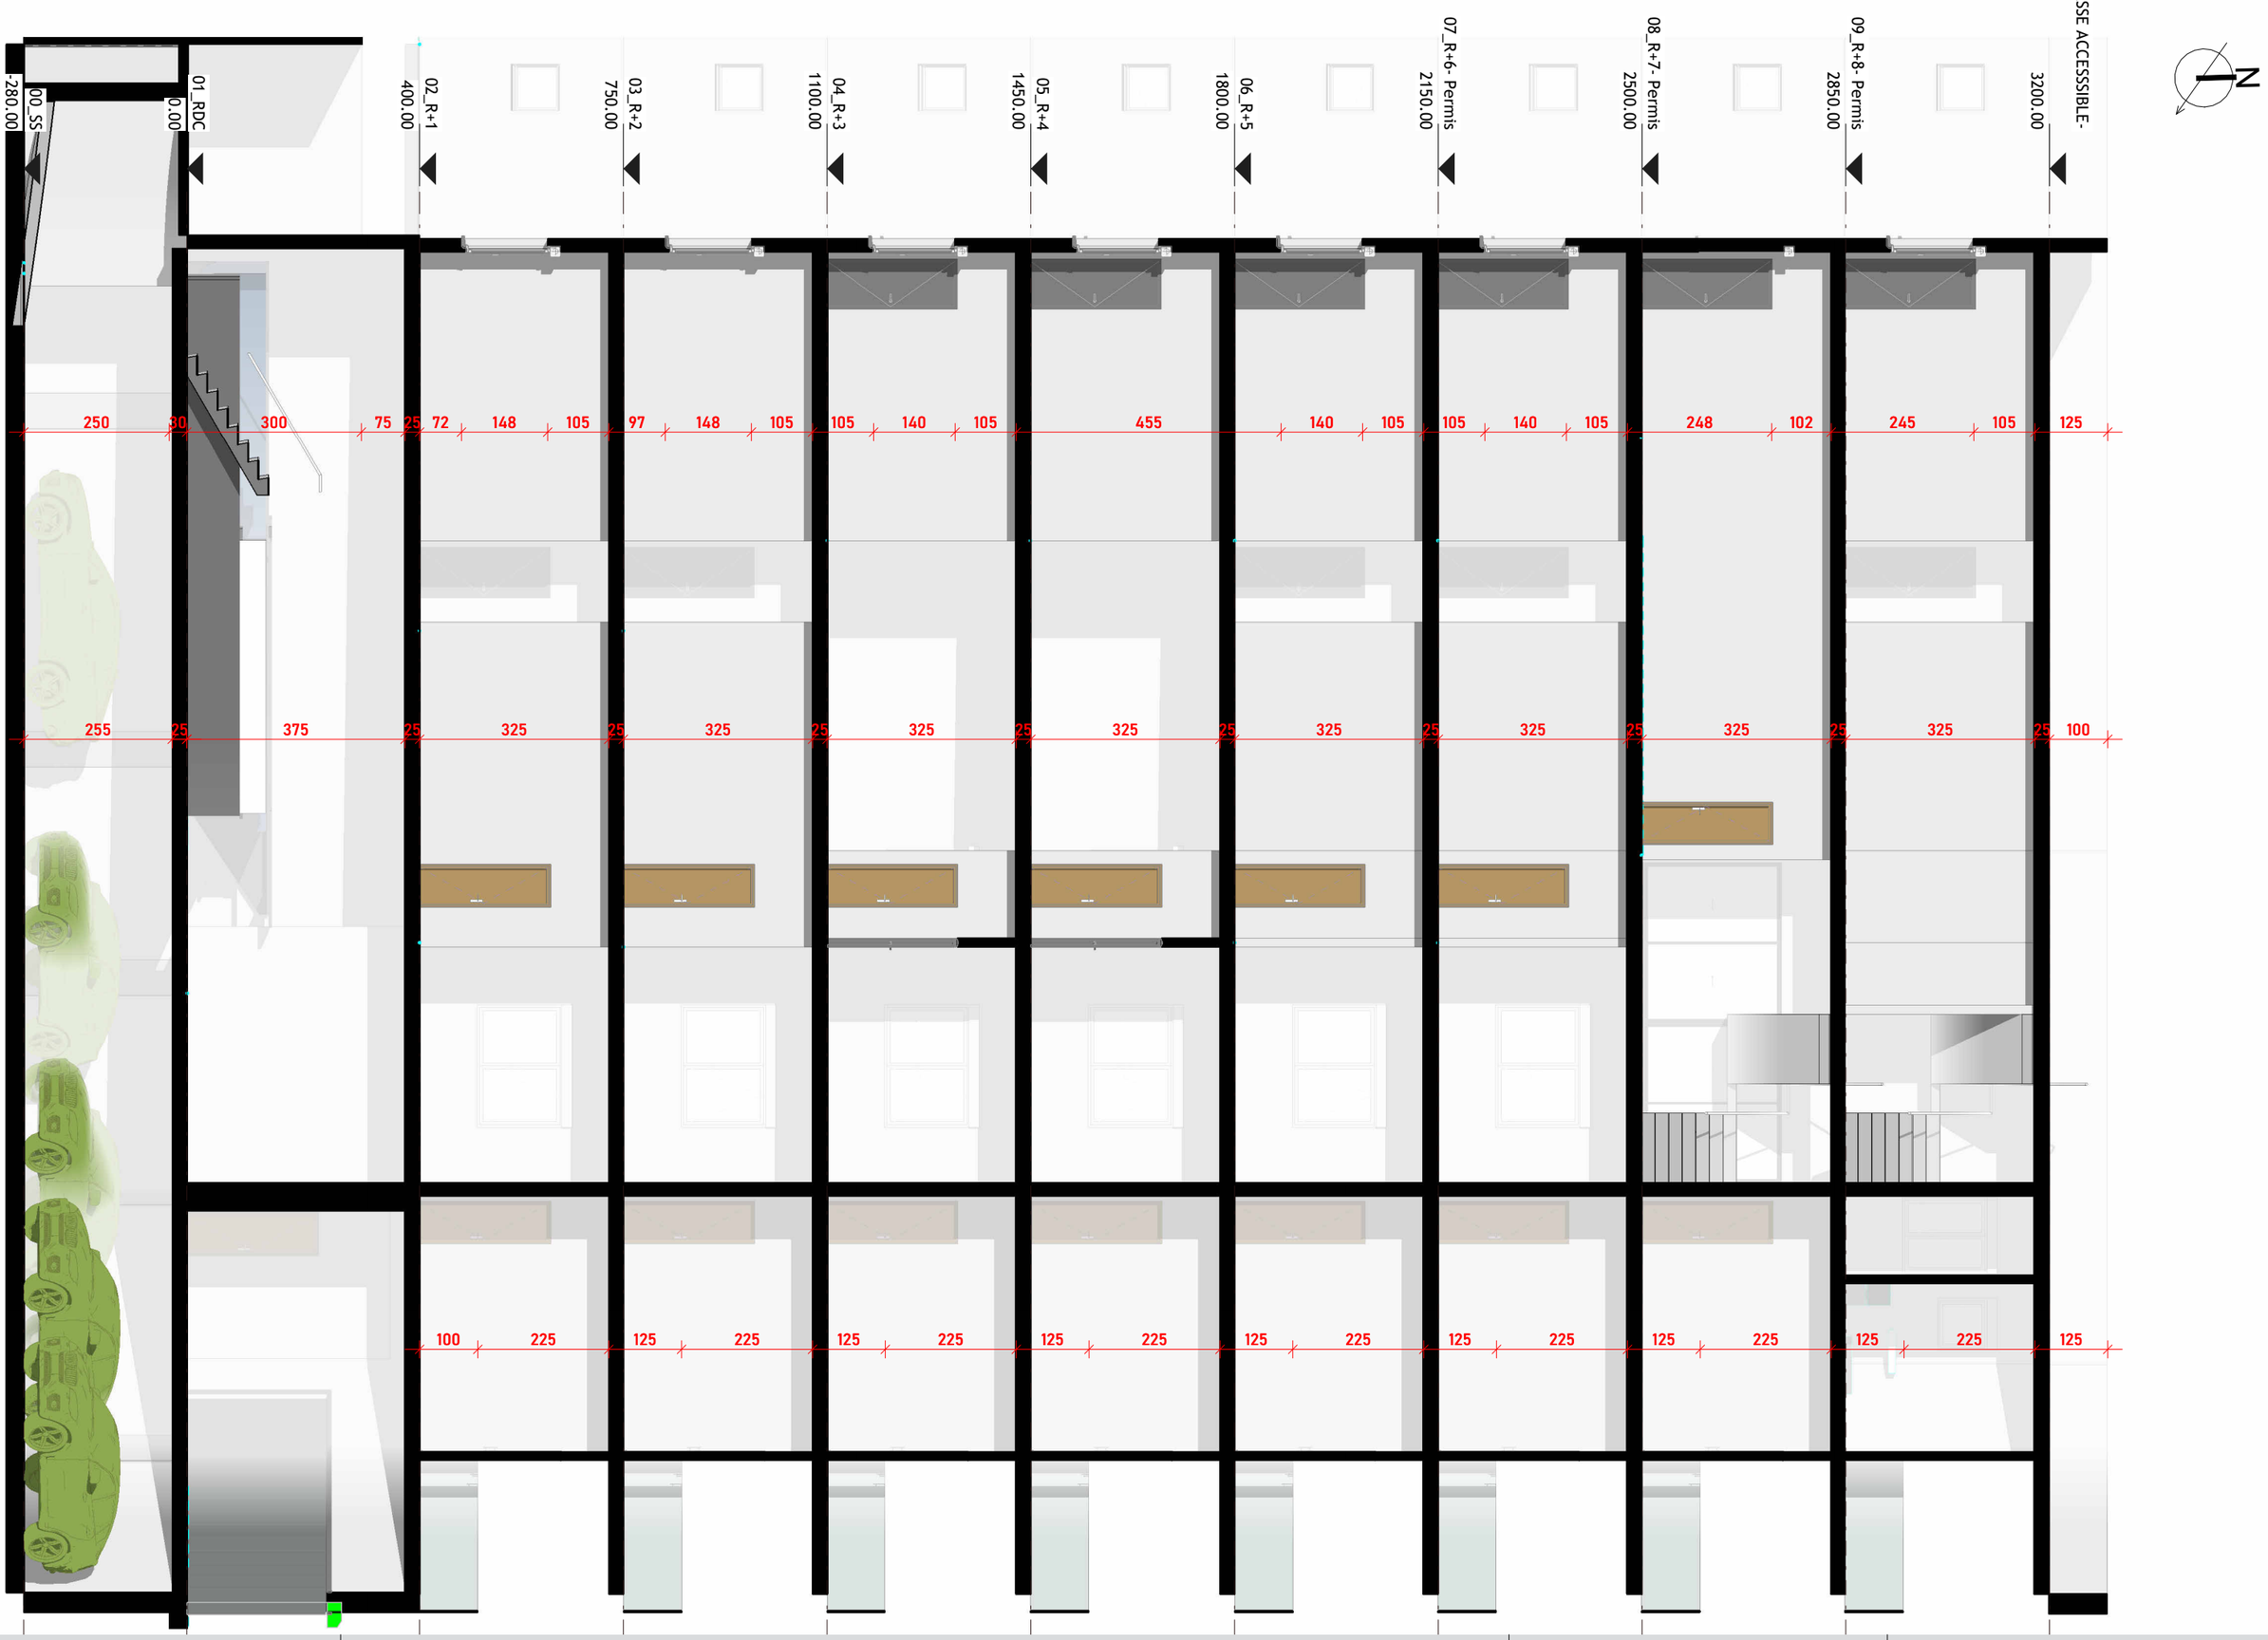

Maitre d'Ouvrage : M.RAMAU

Maitre d'Oeuvre : M.Moussa CISSÉ

COUPE A-A

Echelle: **1 : 100**

PROJET: LIFE STYLE


00_11

_ SS + 8 ETAGES _

DAKAR_ Sénégal

Date

13/04/2026 06:26:45

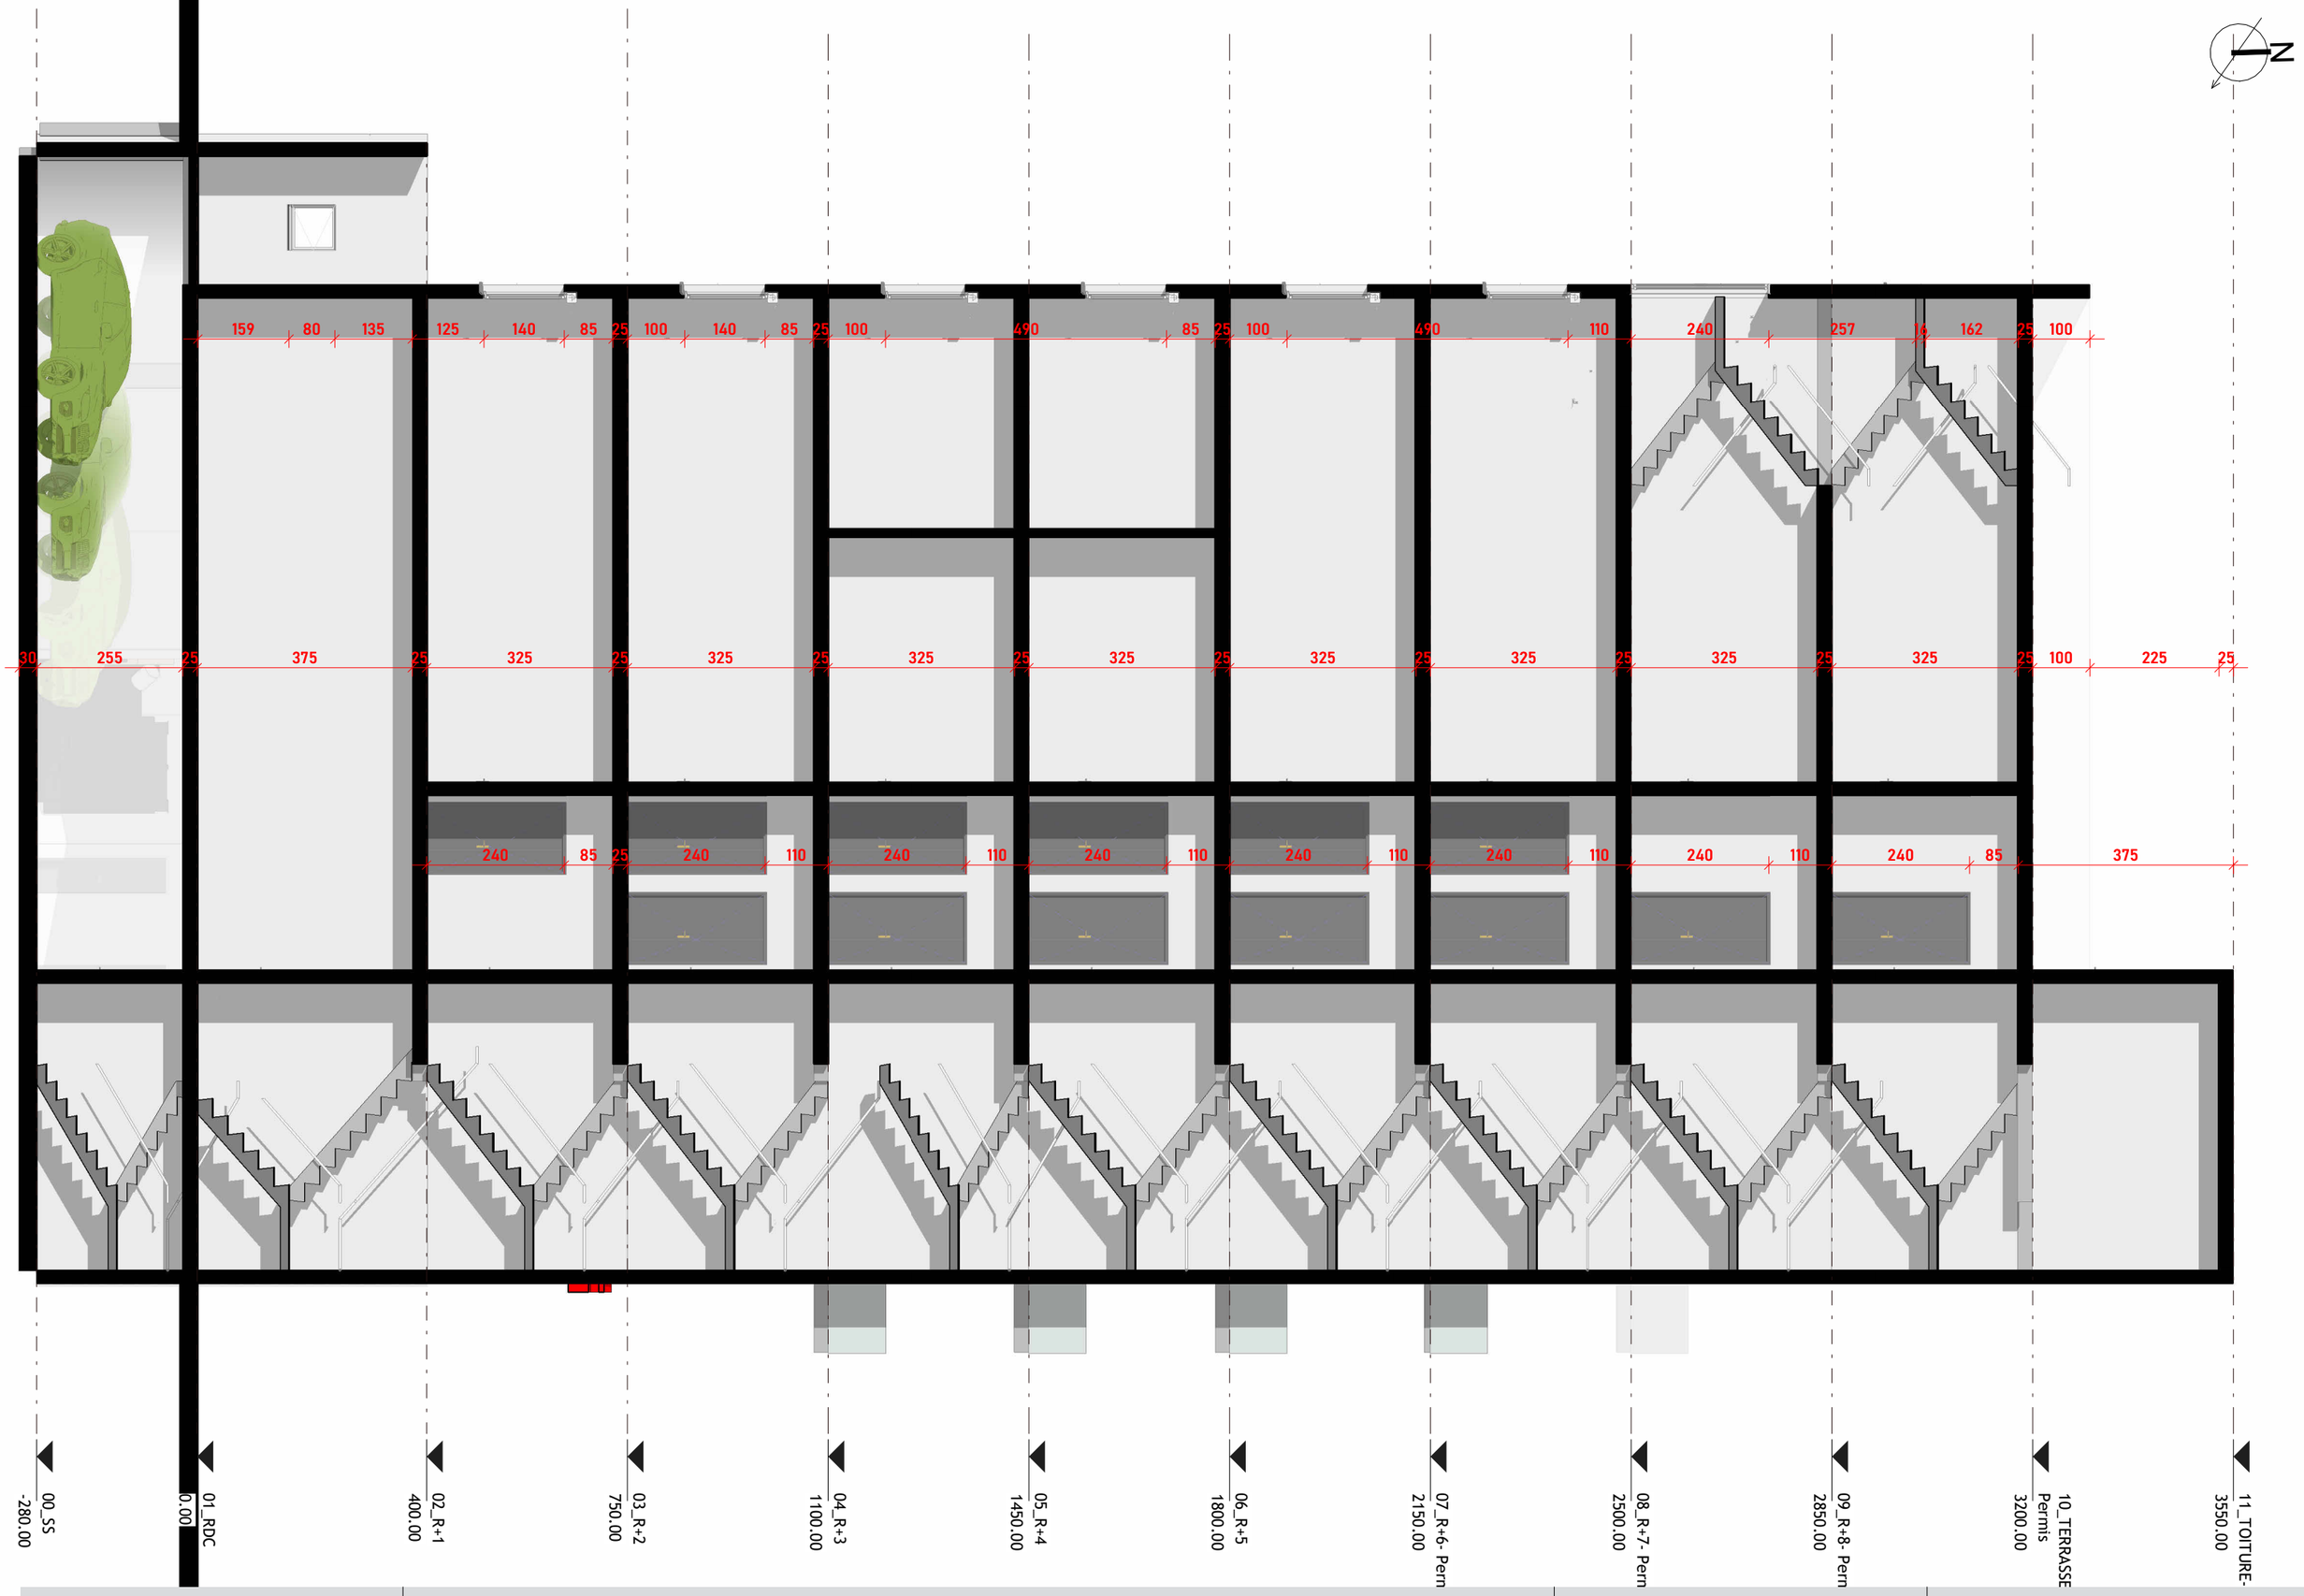

Maitre d'Ouvrage : M.RAMAU

Maitre d'Oeuvre : M.Moussa CISSÉ

COUPE B-B

Echelle: **1 : 100**

PROJET: LIFE STYLE

00_12

_ SS + 8 ETAGES _

DAKAR_ Sénégal

Date

13/04/2026 06:26:51



Maitre d'Ouvrage : M.RAMAU

Maitre d'Oeuvre : M.Moussa CISSÉ

FAÇADE PRINCIPALE

Echelle: **1 : 150**

PROJET: LIFE STYLE


00_13

_ SS + 8 ETAGES _

DAKAR_ Sénégal

Date

13/04/2026 06:27:44

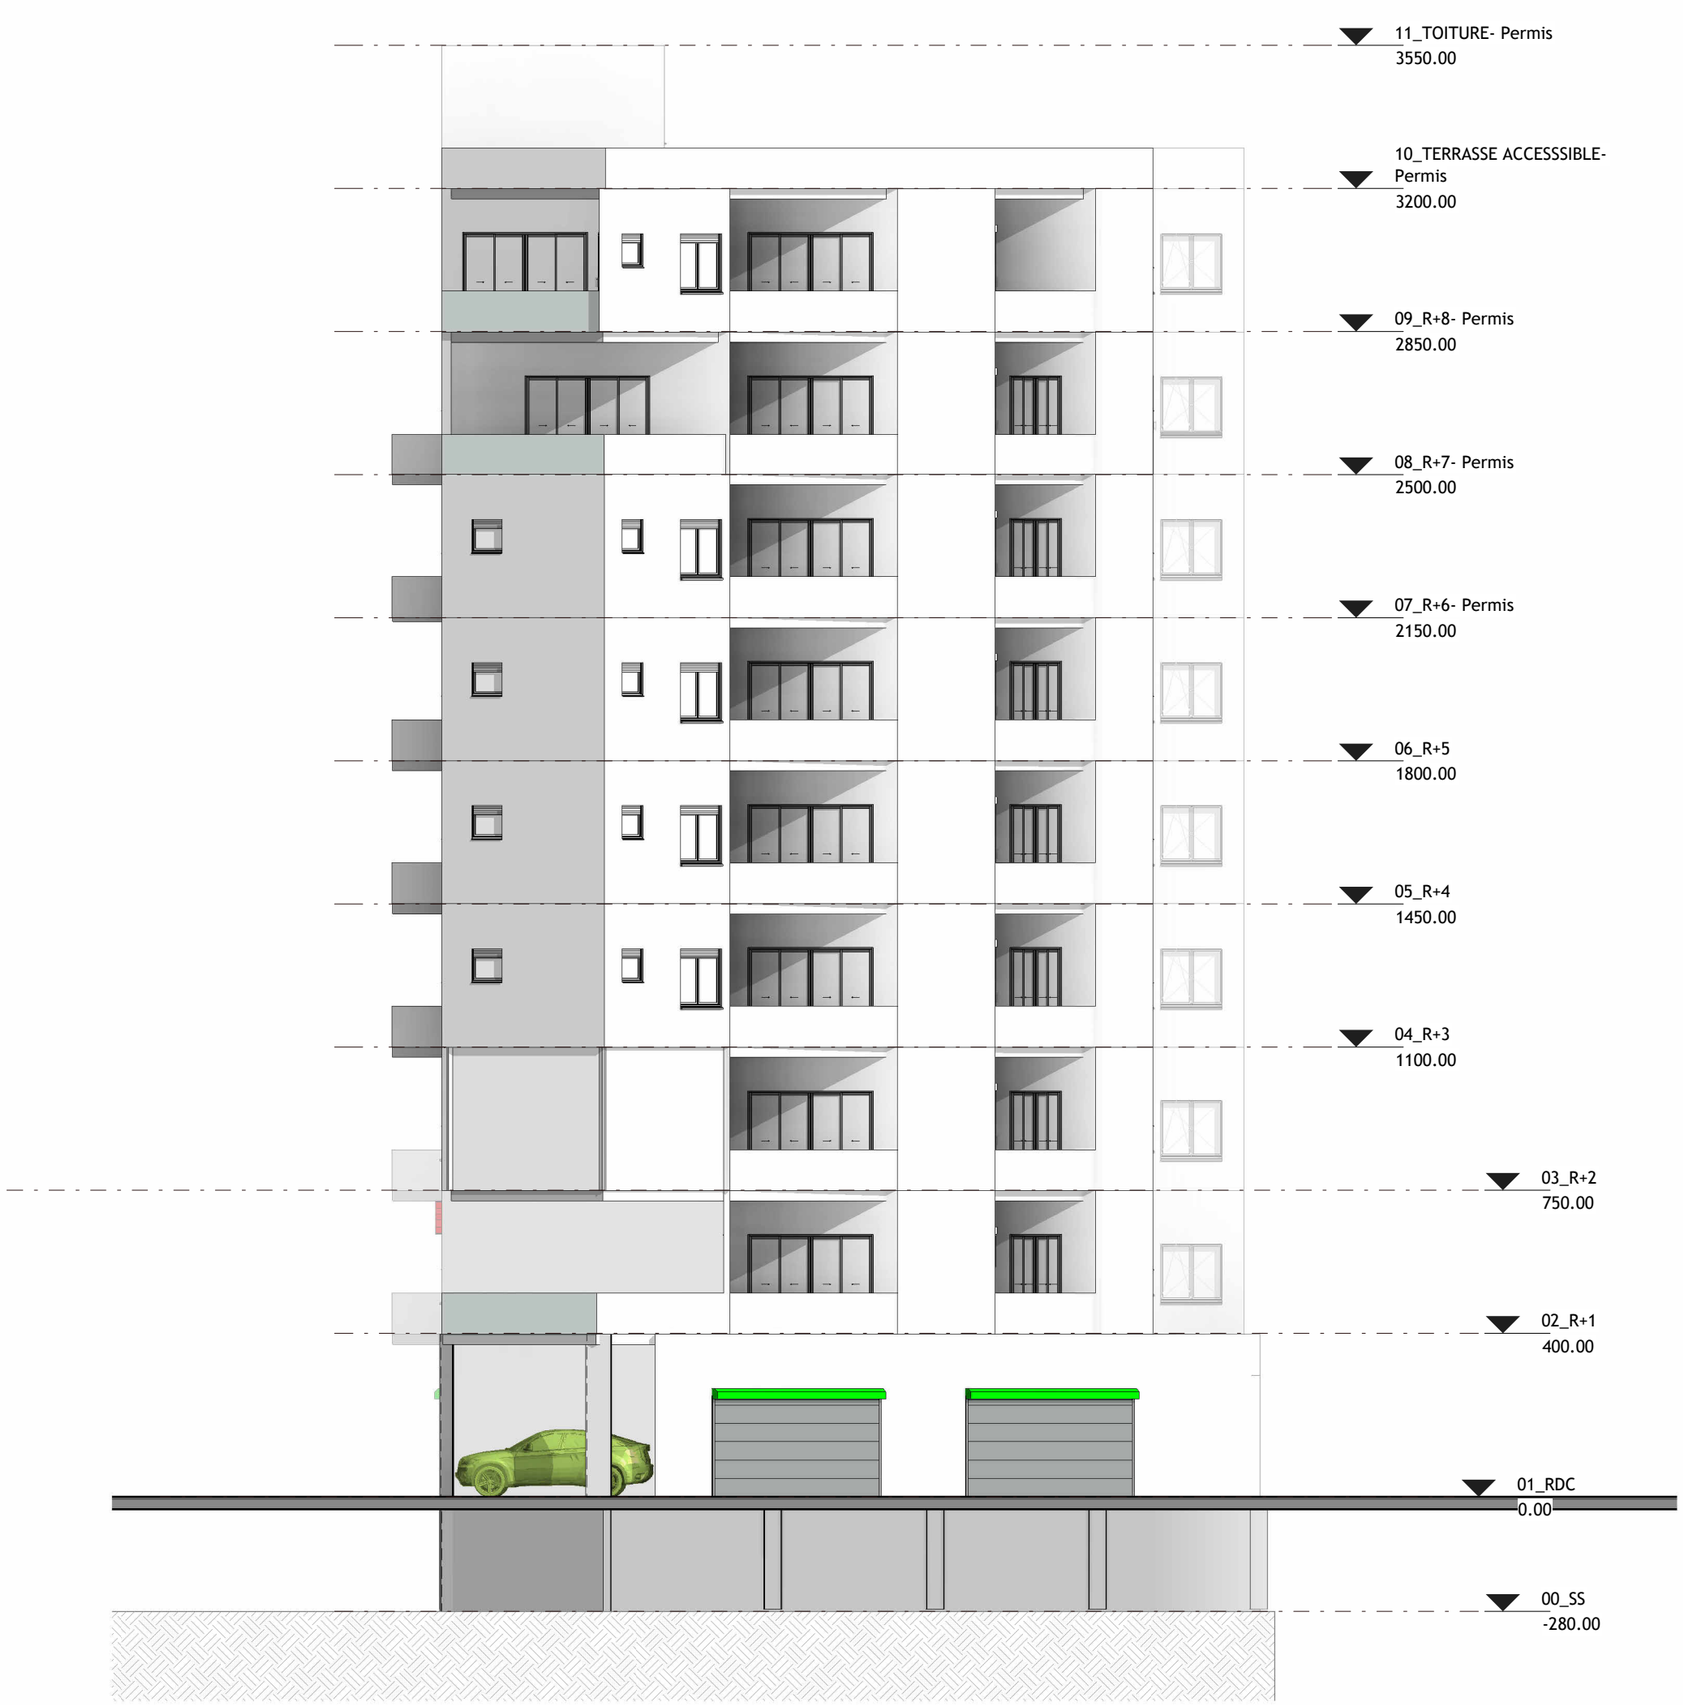

Maitre d'Ouvrage : M.RAMAU

Maitre d'Oeuvre : M.Moussa CISSÉ

FAÇADE OUEST

Echelle: **1 : 150**

PROJET: LIFE STYLE

00_14

_ SS + 8 ETAGES _

DAKAR_ Sénégal

Date

13/04/2026 06:28:34