PHASE : A.P.S

Date : 09/06/2026 20:32:11

POLYCONCEPT GROUP







Mr CHEIKH AHMADOU BAMBA DJIKINE

VUE 1

Echelle:

_ RDC + 1 ETAGES + TERRASSE

DAKAR_ TIVAOUNE PEULH

11

Ing.Moussa CISSÉ
TEL:+221 77 231 96 53
mail: moussac1994.21@gmail.com

PHASE : A.P.S

Date : 09/06/2026 20:32:11

POLYCONCEPT GROUP



Mr CHEIKH AHMADOU BAMBA DJIKINE

VUE 2

Echelle:

_ RDC + 1 ETAGES + TERRASSE

DAKAR_ TIVAOUNE PEULH

12

Ing.Moussa CISSÉ
TEL:+221 77 231 96 53
mail: moussac1994.21@gmail.com

PHASE : A.P.S

Date : 09/06/2026 20:32:12

POLYCONCEPT GROUP



Mr CHEIKH AHMADOU BAMBA DJIKINE	VUE 3 Echelle:	**_ RDC + 1 ETAGES + TERRASSE** **DAKAR**_ TIVAOUNE PEULH	**13**

Ing.Moussa CISSÉ
TEL.:+221 77 231 96 53
mail: moussac1994.21@gmail.com

PHASE : A.P.S

Date : 09/06/2026 20:32:40

POLYCONCEPT GROUP

N

PATIO
6.25 m²

WC
3.13 m²

CHAMBRE
PARENTALE
16.17 m²

SDB
3.30 m²

COUR ARRIÈRE
5.25 m²

HALL D'ENTRÉE
4.88 m²

SÉOUR
45.03 m²

CHAMBRE 2
14.43 m²

PATIO
5.63 m²

SDB
3.25 m²

CUISINE
10.55 m²

MAGASIN
15.00 m²

Mr CHEIKH AHMADOU BAMBA DJIKINE	VUE EN PLAN REZ-DE-CHAUSSÉE Echelle: **1 : 50**	**_ RDC + 1 ETAGES + TERRASSE** **DAKAR**_ TIVAOUNE PEULH	**01**

Ing.Moussa CISSÉ
TEL:+221 77 231 96 53
mail: moussac1994.21@gmail.com

PHASE : A.P.S

Date : 09/06/2026 20:33:05

POLYCONCEPT GROUP

N

VIDE SUR PATIO
6.25 m²

WC
3.13 m²

CHAMBRE 1
PARENTALE
16.17 m²

SDB 1
3.30 m²

VIDE SUR COUR
ARRIÈRE
5.25 m²

BALCON
4.93 m²

SÉJOUR
44.52 m²

BALCON
1.18 m²

CHAMBRE 3
12.00 m²

CHAMBRE 2
14.43 m²

VIDE SUR PATIO
5.63 m²

CHAMBRE 4
10.55 m²

SDB 3
2.68 m²

SDB 2
3.25 m²


Mr CHEIKH AHMADOU BAMBA DJIKINE	VUE EN PLAN ETAGE 1 Echelle: **1 : 50**	**_ RDC + 1 ETAGES + TERRASSE** **DAKAR**_ TIVAOUNE PEULH	**02**

Ing.Moussa CISSÉ
TEL:+221 77 231 96 53
mail: moussac1994.21@gmail.com

PHASE : A.P.S

Date : 09/06/2026 20:33:05

POLYCONCEPT GROUP

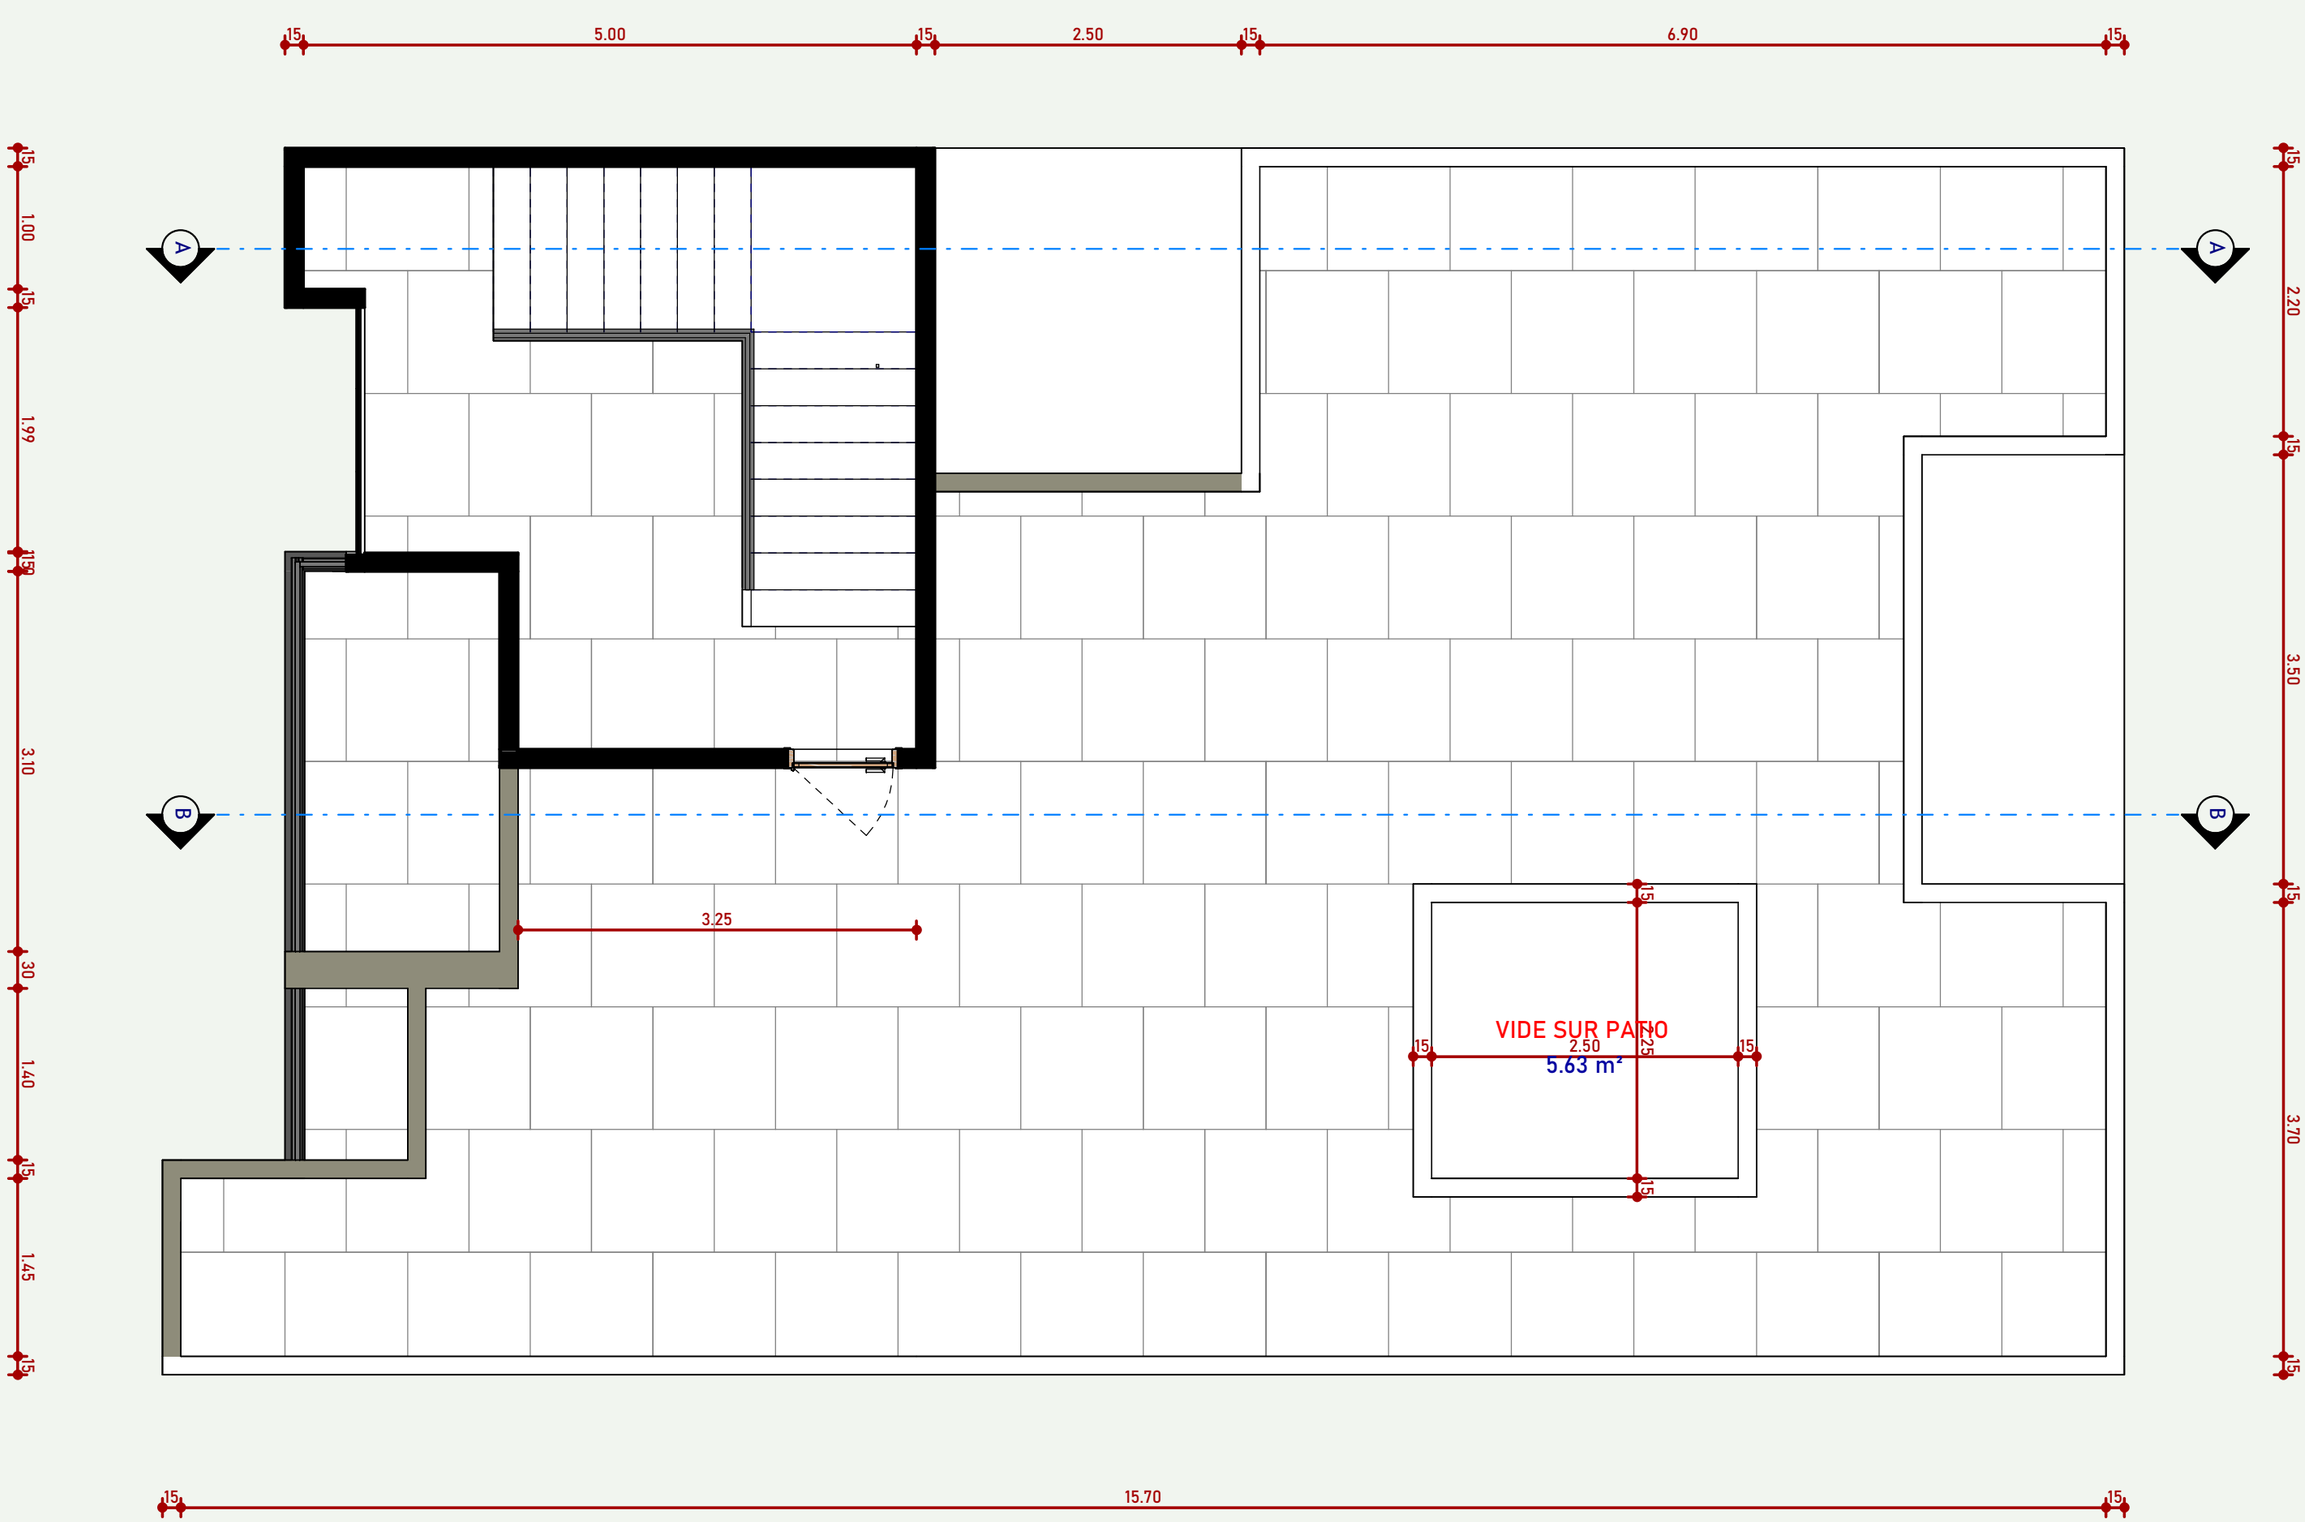


Mr CHEIKH AHMADOU BAMBA DJIKINE	VUE EN PLAN TÉRRASSE Echelle: **1 : 50**	**_ RDC + 1 ETAGES + TERRASSE** **DAKAR**_ TIVAOUNE PEULH	**03**

Ing.Moussa CISSÉ
TEL:+221 77 231 96 53
mail: moussac1994.21@gmail.com

PHASE : A.P.S

Date : 09/06/2026 20:33:10

POLYCONCEPT GROUP

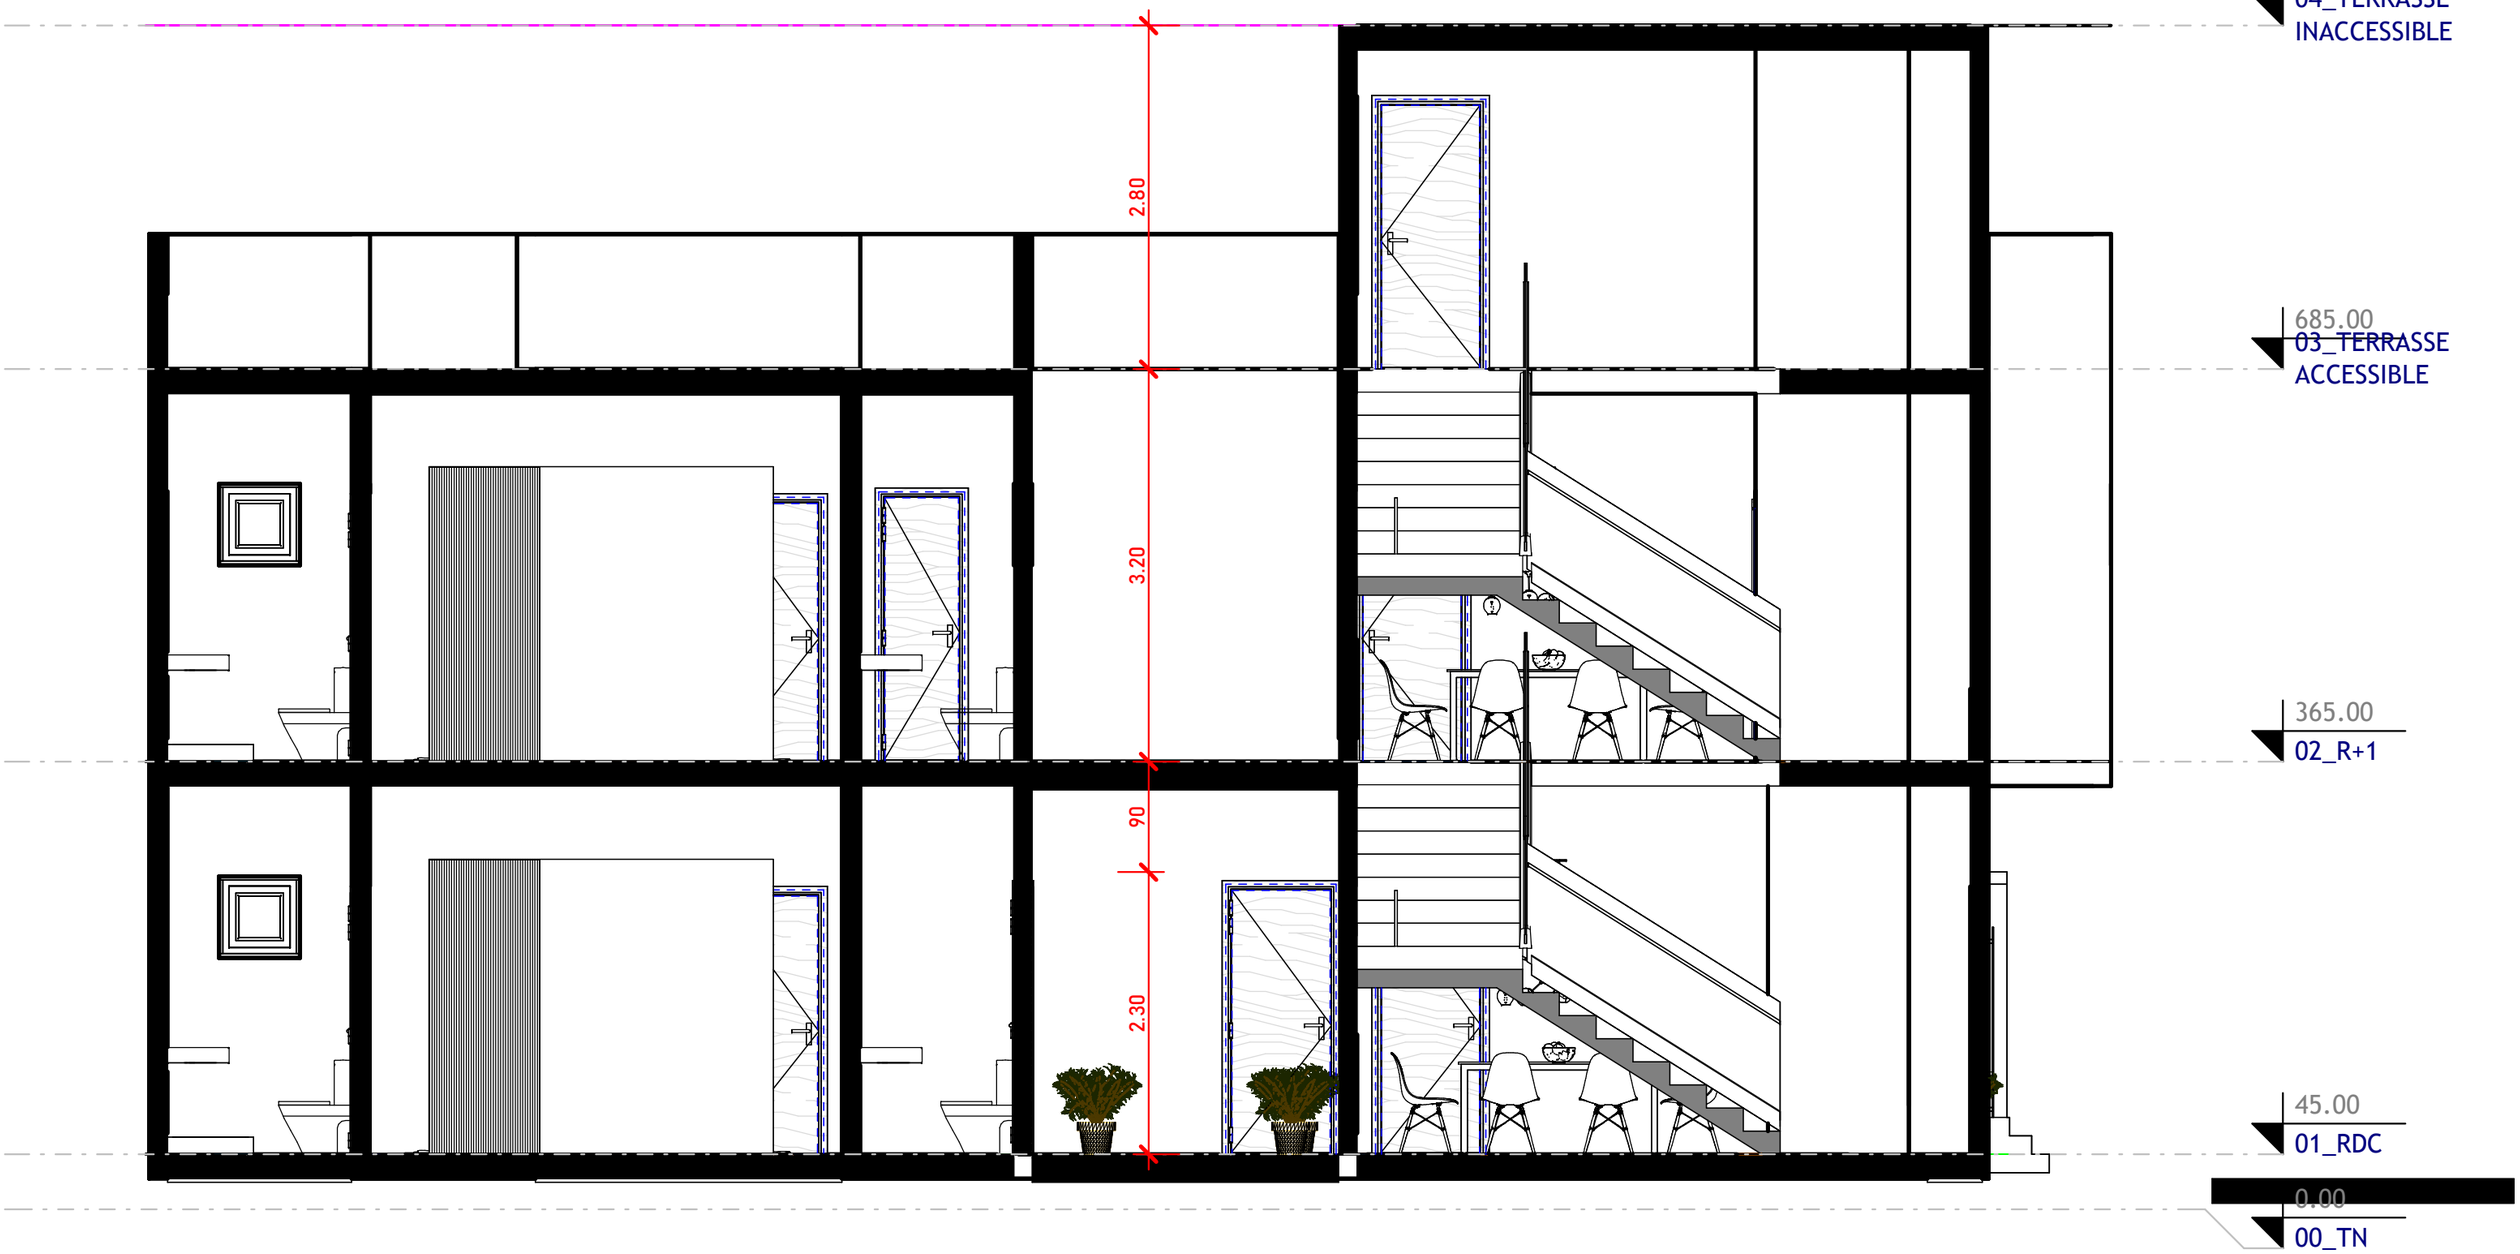

Mr CHEIKH AHMADOU BAMBA DJIKINE

COUPE A-A

Echelle: **1 : 50**

_ RDC + 1 ETAGES + TERRASSE

DAKAR_ TIVAOUNE PEULH

04

Ing.Moussa CISSÉ
TEL:+221 77 231 96 53
mail: moussac1994.21@gmail.com


PHASE : A.P.S

Date : 09/06/2026 20:33:13

POLYCONCEPT GROUP

965.00
04_TERRASSE INACCESSIBLE

685.00
03_TERRASSE ACCESSIBLE

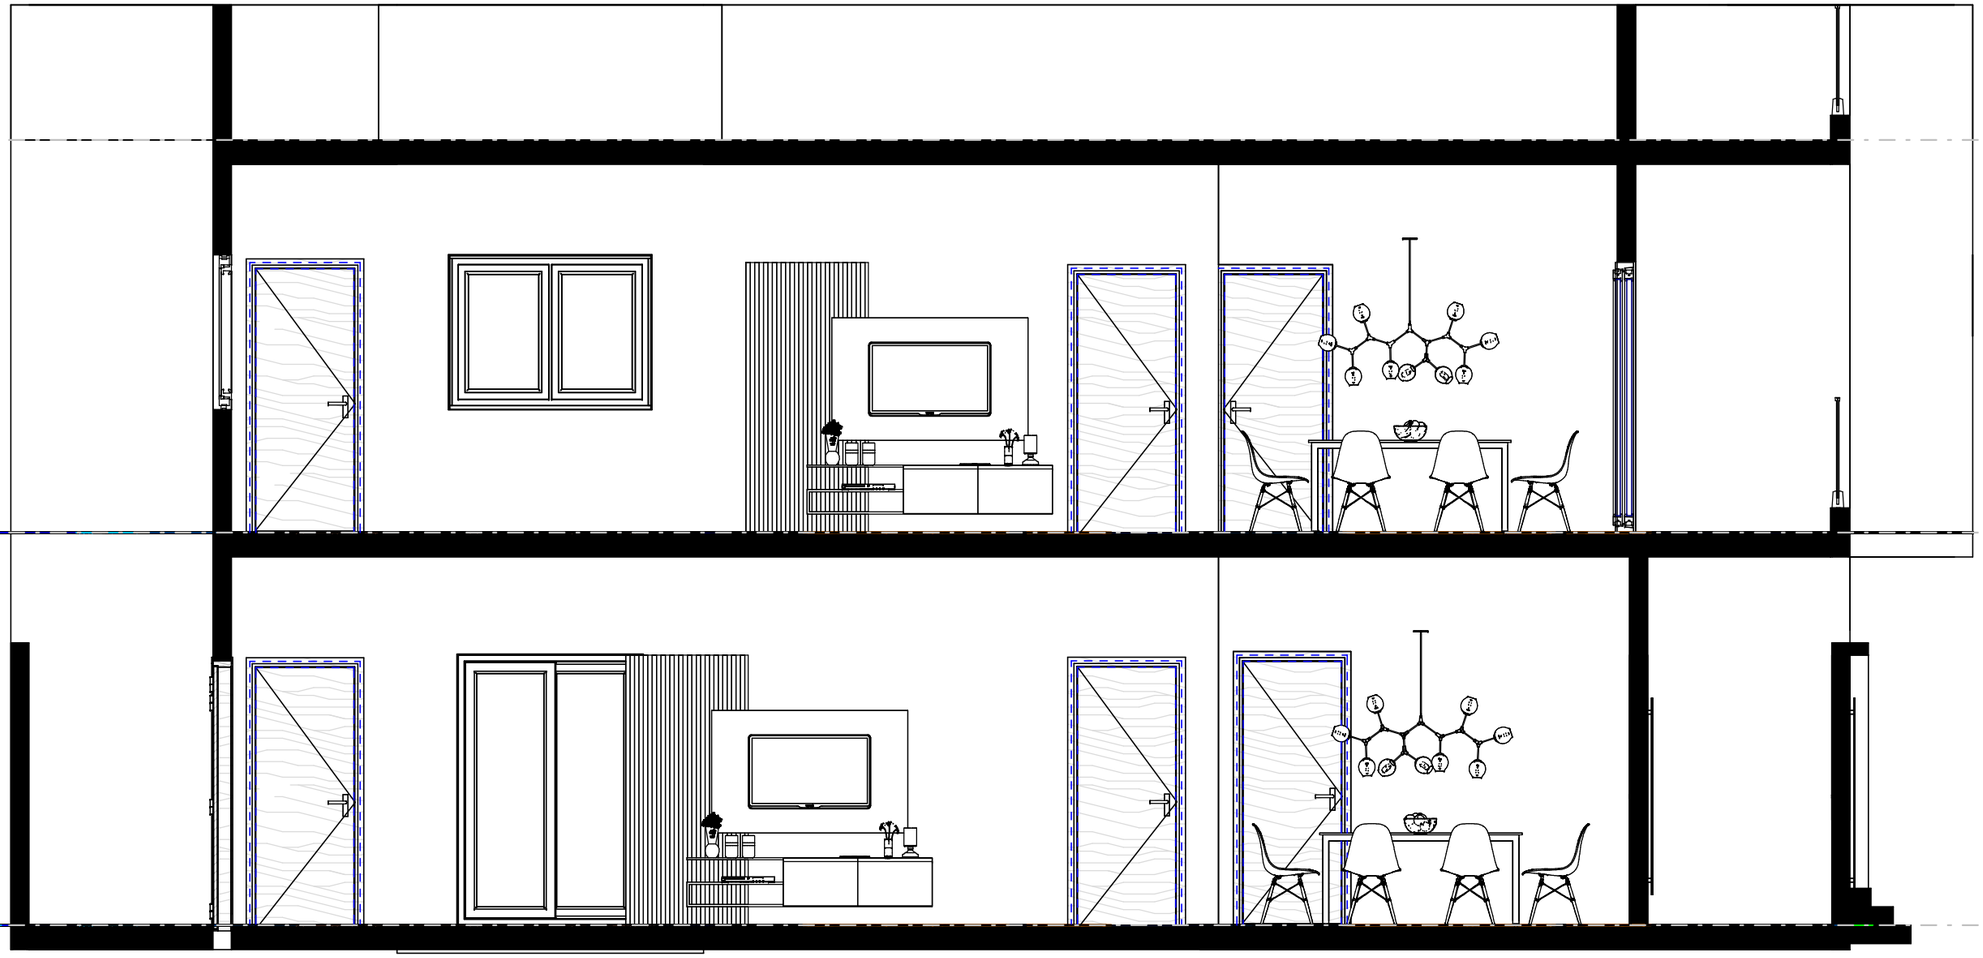

365.00
02_R+1

45.00
01_RDC

0.00
00_TN

Mr CHEIKH AHMADOU BAMBA DJIKINE	COUPE B-B Echelle: **1 : 50**	**_ RDC + 1 ETAGES + TERRASSE** **DAKAR**_ TIVAOUNE PEULH	**05**	Ing.Moussa CISSÉ TEL:+221 77 231 96 53 mail: moussac1994.21@gmail.com

PHASE : A.P.S

Date : 09/06/2026 20:33:25

POLYCONCEPT GROUP



Mr CHEIKH AHMADOU BAMBA DJIKINE

FAÇADE PRINCIPALE

Echelle: **1 : 50**

_ RDC + 1 ETAGES + TERRASSE

DAKAR_ TIVAOUNE PEULH

06

Ing.Moussa CISSÉ
TEL:+221 77 231 96 53
mail: moussac1994.21@gmail.com



PHASE : A.P.S

Date : 09/06/2026 20:33:29

POLYCONCEPT GROUP

Mr CHEIKH AHMADOU BAMBA DJIKINE	AXO RDC Echelle:	**_ RDC + 1 ETAGES + TERRASSE** **DAKAR**_ TIVAOUNE PEULH	**07**	POLYCONCEPT

Ing.Moussa CISSÉ
TEL:+221 77 231 96 53
mail: moussac1994.21@gmail.com

PHASE : A.P.S

Date : 09/06/2026 20:33:35

POLYCONCEPT GROUP



Mr CHEIKH AHMADOU BAMBA DJIKINE

AXO ETAGE 1

Echelle:

_ RDC + 1 ETAGES + TERRASSE

DAKAR_ TIVAOUNE PEULH


08

Ing.Moussa CISSÉ
TEL:+221 77 231 96 53
mail: moussac1994.21@gmail.com

PHASE : A.P.S

Date : 09/06/2026 20:33:38

POLYCONCEPT GROUP

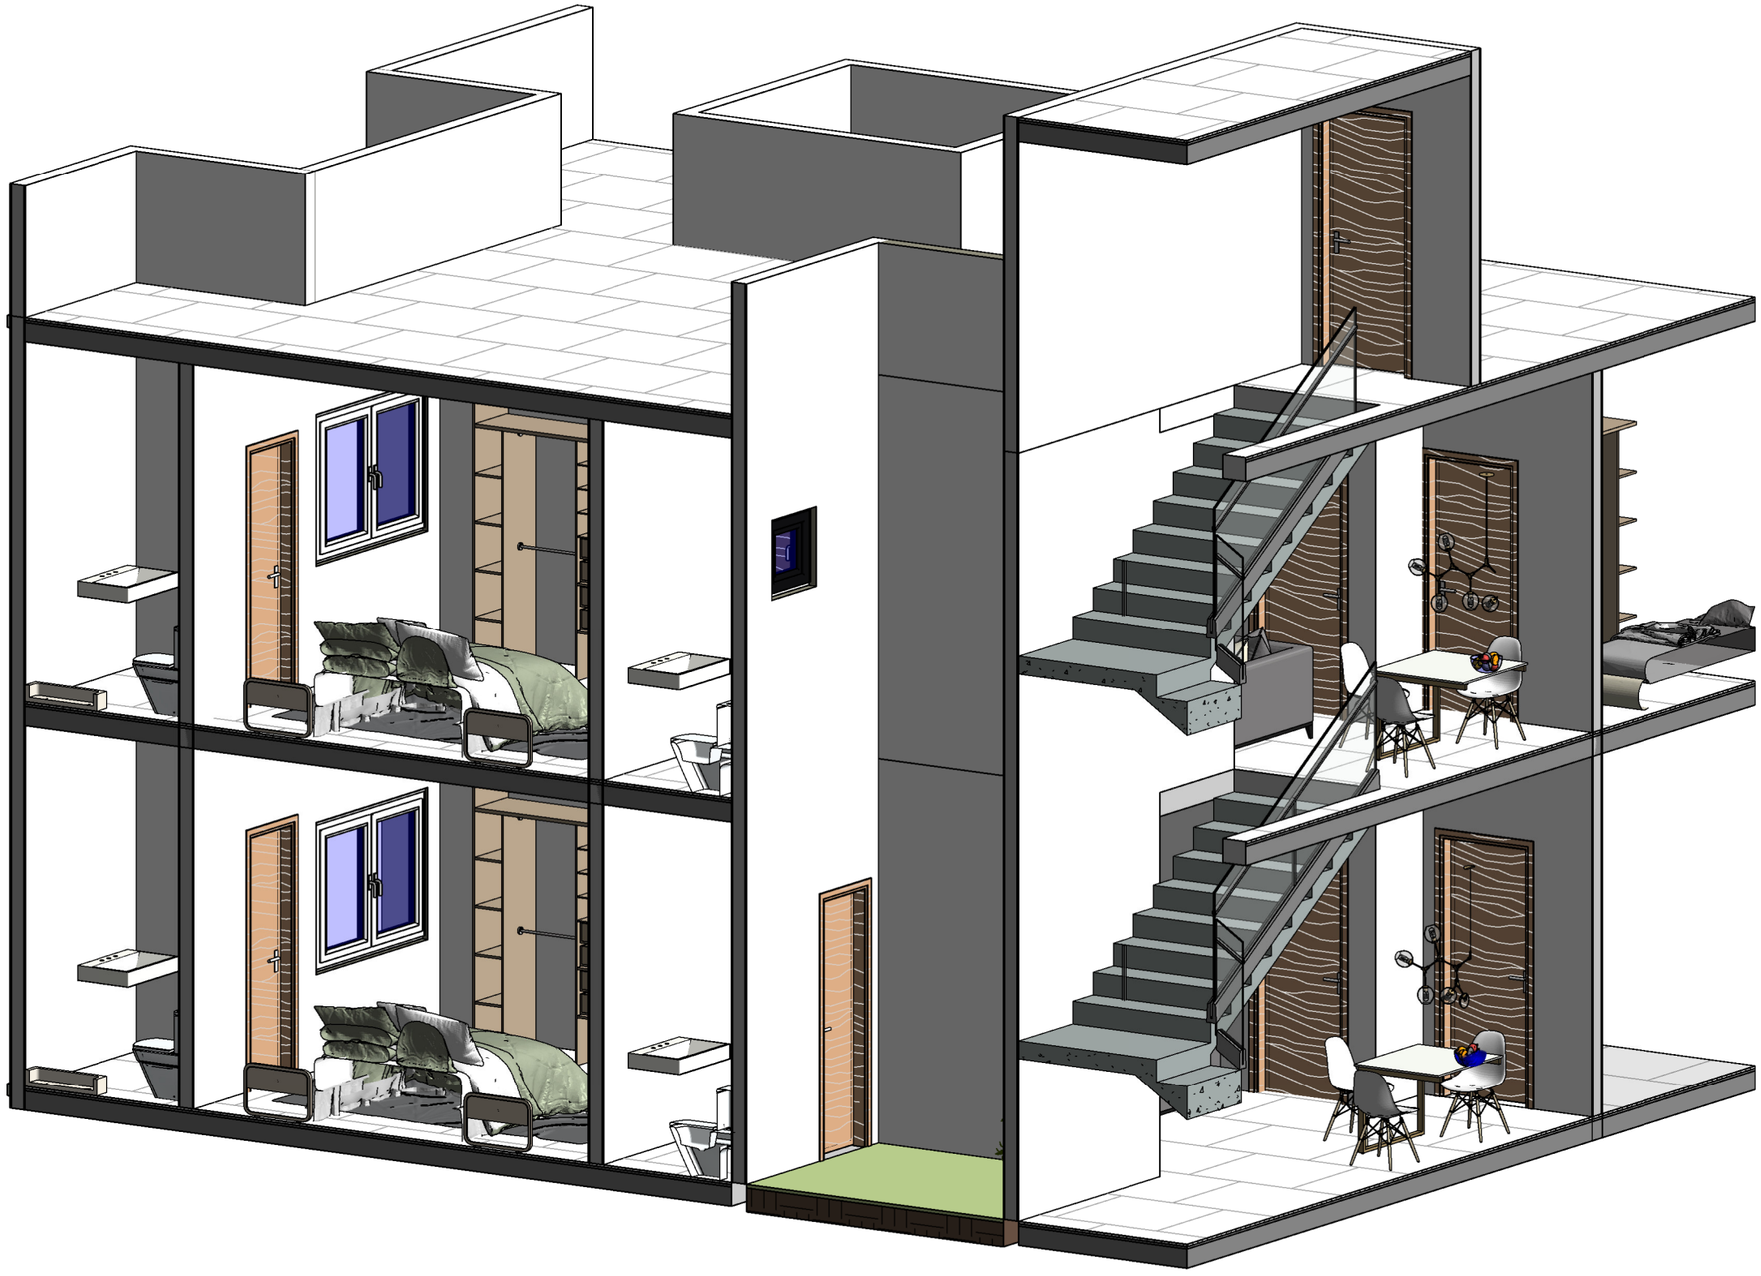

1 AXO COUPE A-A

Ech : COUPE A-A

Echelle:

Mr CHEIKH AHMADOU BAMBA DJIKINE

_ RDC + 1 ETAGES + TERRASSE

DAKAR_ TIVAOUNE PEULH

09

Ing.Moussa CISSÉ
TEL:+221 77 231 96 53
mail: moussac1994.21@gmail.com



Ing.Moussa CISSÉ
TEL:+221 77 231 96 53
mail: moussac1994.21@gmail.com