TERRASSE INACCESSIBLE

TERRASSE
Surf. au sol : 16.92m²
Sol : carrelage 60x60
Mur : peinture lisse
Plafond : staff lisse

TERRASSE
Surf. au sol : 21.03m²
Sol : carrelage 60x60
Mur : peinture lisse
Plafond : staff lisse

TERRASSE
Surf. au sol : 4.50m²
Sol : carrelage 60x60
Mur : peinture lisse
Plafond : staff lisse

SUITE PARENTAL
Surf. au sol : 38.58m²
Sol : carrelage 60x60
Mur : peinture lisse
Plafond : staff lisse

SALON/SEJOUR
Surf. au sol : 30.00m²
Sol : carrelage 60x60
Mur : peinture lisse
Plafond : staff lisse

ESPACE FAMILIAL
Surf. au sol : 30.20m²
Sol : carrelage 60x60
Mur : peinture lisse
Plafond : staff lisse

DEGAGEMENT
Surf. au sol : 9.77m²
Sol : carrelage 60x60
Mur : peinture lisse
Plafond : staff lisse

DRESSING
Surf. au sol : 10.14m²
Sol : carrelage 15x15
Mur : Faience
Plafond : staff lisse

DRESSING
Surf. au sol : 3.68m²
Sol : carrelage 15x15
Mur : Faience
Plafond : staff lisse

CHAMBRE 01
Surf. au sol : 14.00m²
Sol : carrelage 60x60
Mur : peinture lisse
Plafond : staff lisse

S.EAU
Surf. au sol : 10.47m²
Sol : carrelage 15x15
Mur : Faience
Plafond : staff lisse

S.EAU
Surf. au sol : 3.08m²
Sol : carrelage 15x15
Mur : Faience
Plafond : staff lisse

CUISINE / BARS
Surf. au sol : 11.14m²
Sol : carrelage
Mur : peinture lisse
Plafond : staff lisse

SAS
Surf. au sol : 1.19m²
Sol : carrelage 15x15
Mur : Faience
Plafond : staff lisse

T.VIS.
Surf. au sol : 2.39m²
Sol : carrelage 15x15
Mur : Faience
Plafond : staff lisse

VIDE SUR ESPACE FAMILIALE RDC

CHAMBRE 01
Surf. au sol : 16.89m²
Sol : carrelage 60x60
Mur : peinture lisse
Plafond : staff lisse

CHAMBRE 02
Surf. au sol : 23.56m²
Sol : carrelage 60x60
Mur : peinture lisse
Plafond : staff lisse

S.EAU
Surf. au sol : 4.01m²
Sol : carrelage 15x15
Mur : peinture lisse
Plafond : staff lisse

TERRASSE CHAMBRE 02
Surface au sol : 4.10m²
Sol : carrelage 60x60
Mur : Faience
Plafond : staff lisse

TERRASSE INACCESSIBLE


AUVENT

25.00

13.82 8.47 2.46

25.00

VUE EN PLAN R+1

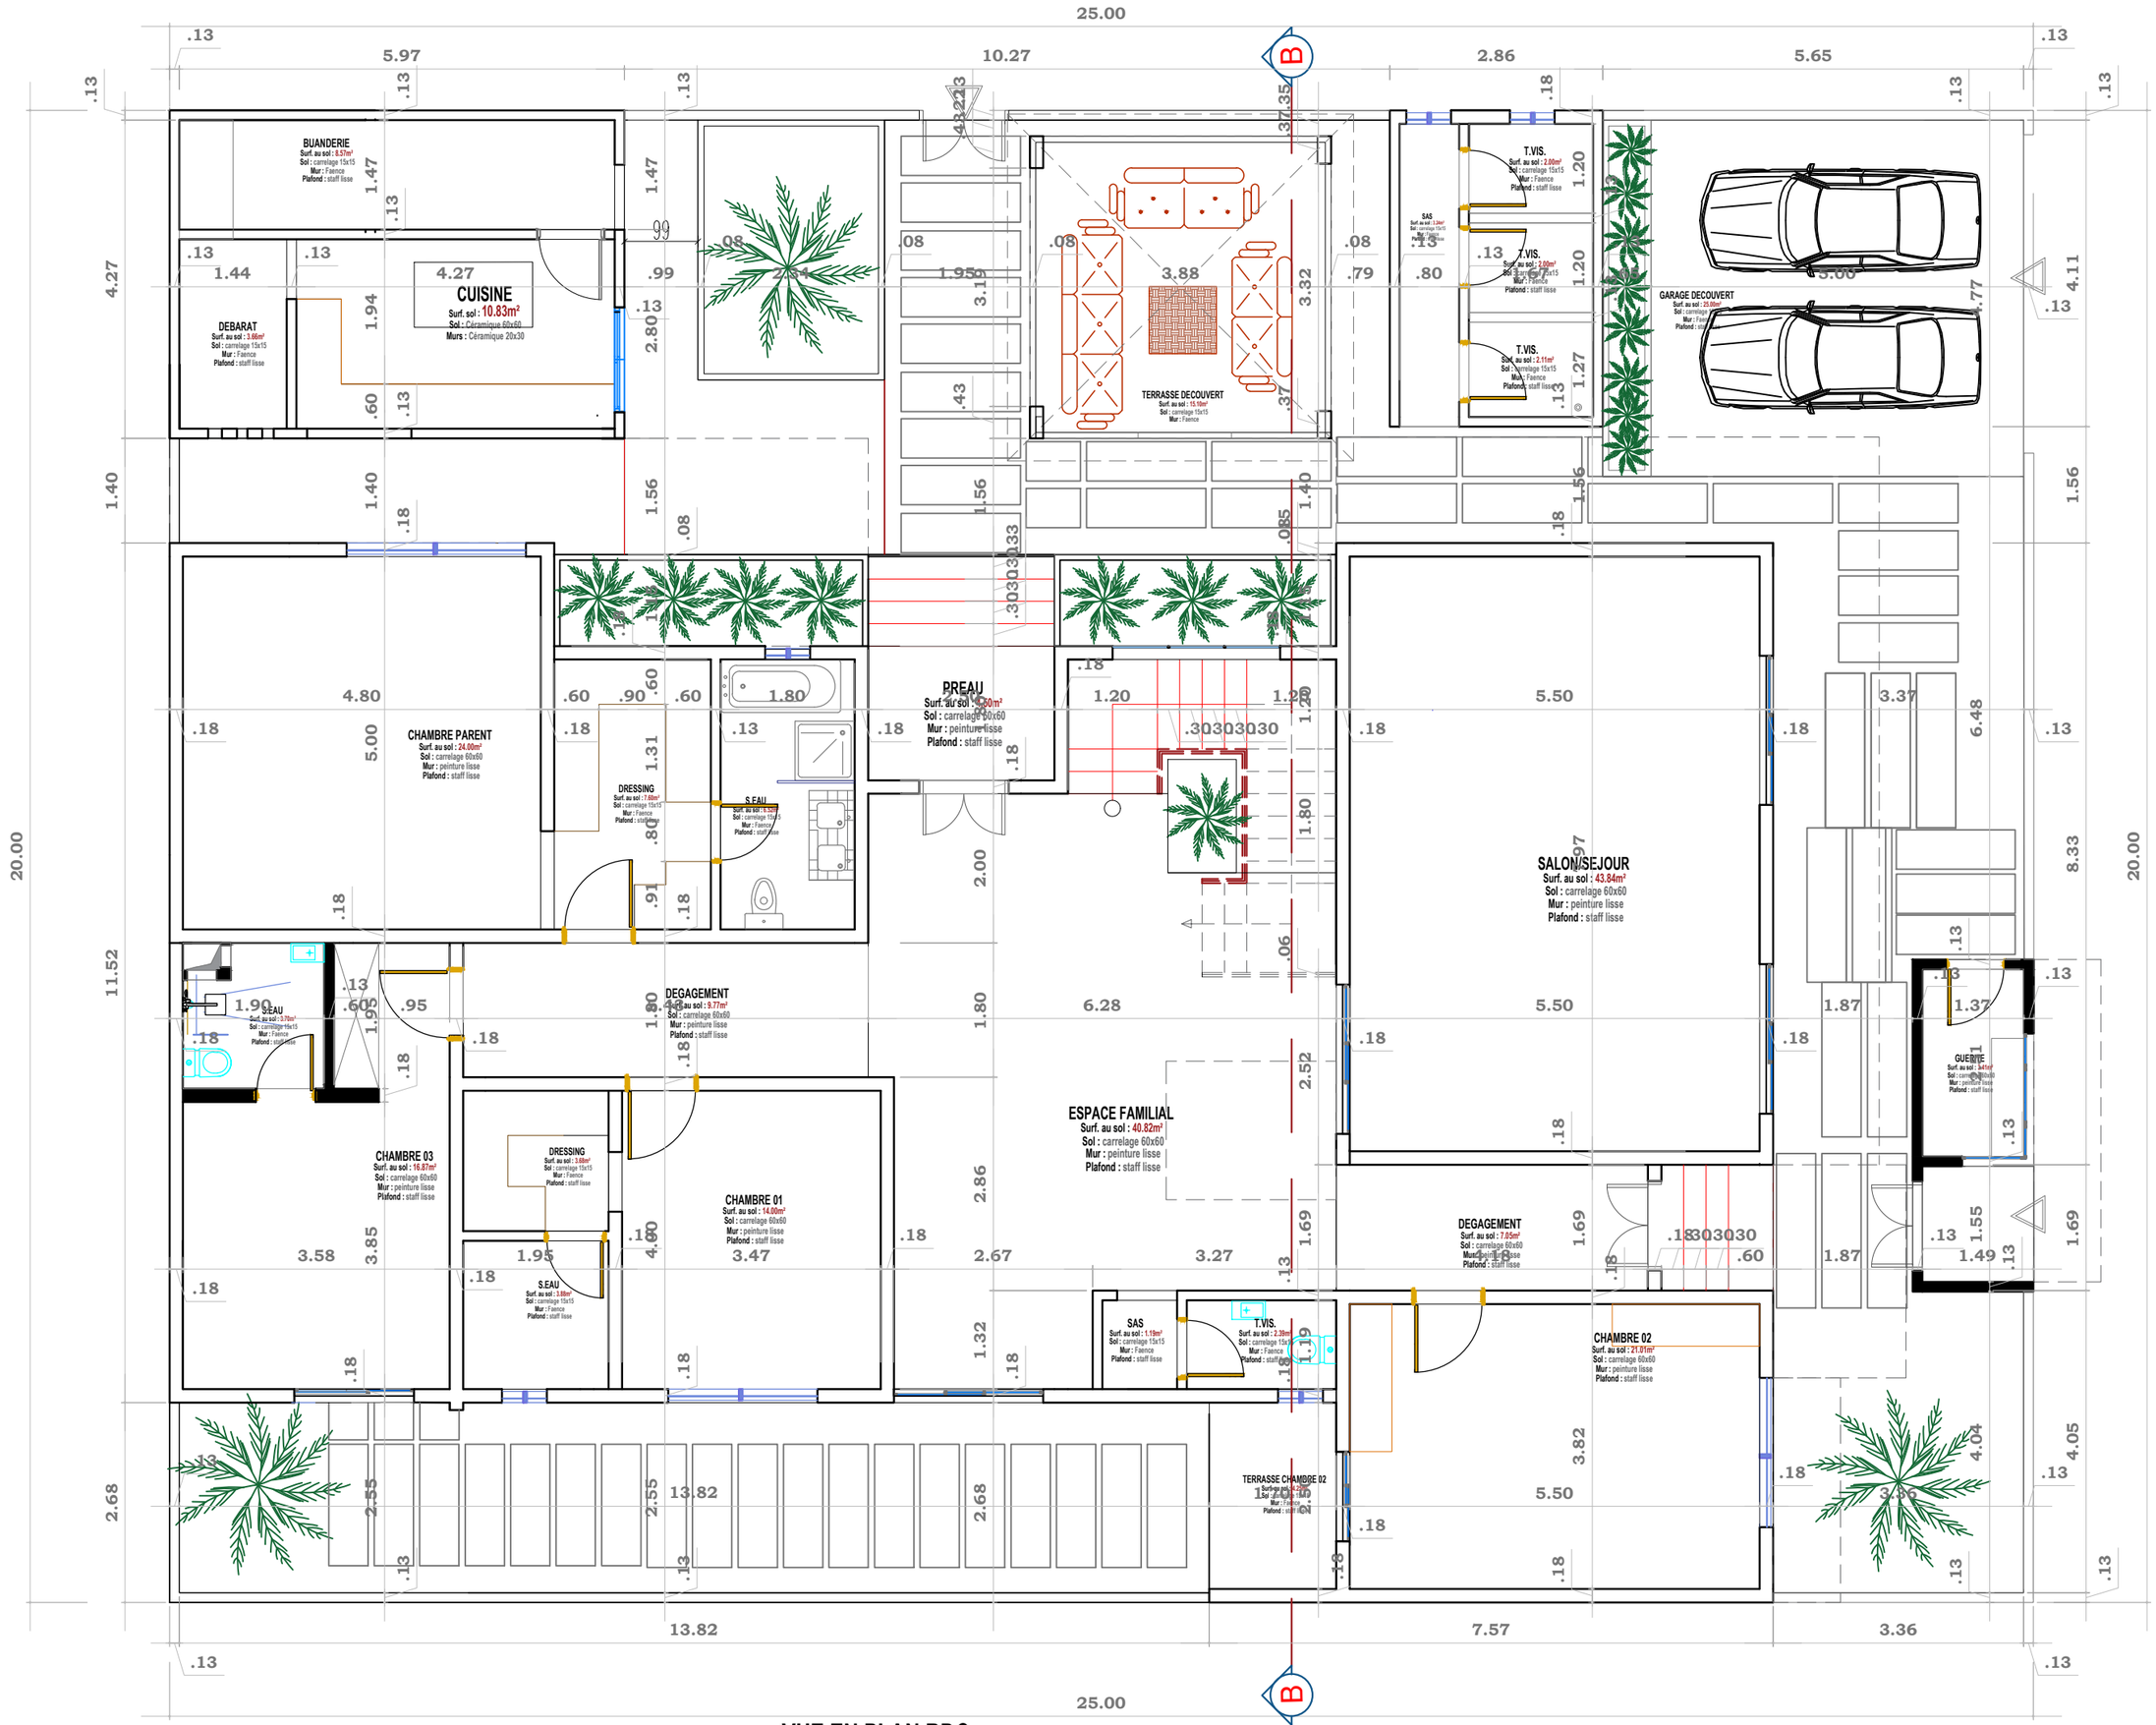

VUE EN PLAN RDC

TERRASSE INACCESSIBLE

TERRASSE INACCESSIBLE BLOC SANITAIRE

AUVENT

AUVENT

TERRASSE
Surf. au sol : 95.03m²
Sol : carrelage 60x30
Mur : peinture lisse

buanderie
Surf. au sol : 6.12m²
Sol : carrelage 60x60
Mur : peinture lisse
Plafond : staff lisse

SALON/SEJOUR
Surf. au sol : 77.08m²
Sol : carrelage 60x60
Mur : peinture lisse
Plafond : staff lisse

VIDE SUR ESPACE FAMILIALE RDC

Cuisine Africaine
Surf. au sol : 14.30m²
Sol : carrelage 60x60
Mur : peinture lisse
Plafond : staff lisse

CUISINE / BARS
Surf. au sol : 11.16m²
Sol : parquet
Mur : peinture lisse
Plafond : staff lisse

SAS
Surf. au sol : 1.71m²
Sol : carrelage 10x10
Mur : FAIENCE
Plafond : staff lisse

CHAMBRE 02
Surf. au sol : 23.56m²
Sol : carrelage 60x60
Mur : peinture lisse
Plafond : staff lisse

TERRASSE CHAMBRE 02
Surf. au sol : 4.10m²
Sol : carrelage 10x15
Mur : Faience
Plafond : staff lisse


TERRASSE INACCESSIBLE


TERRASSE INACCESSIBLE GUERITE

AUVENT

VUE EN PLAN TERRASSE

COUPE B-B

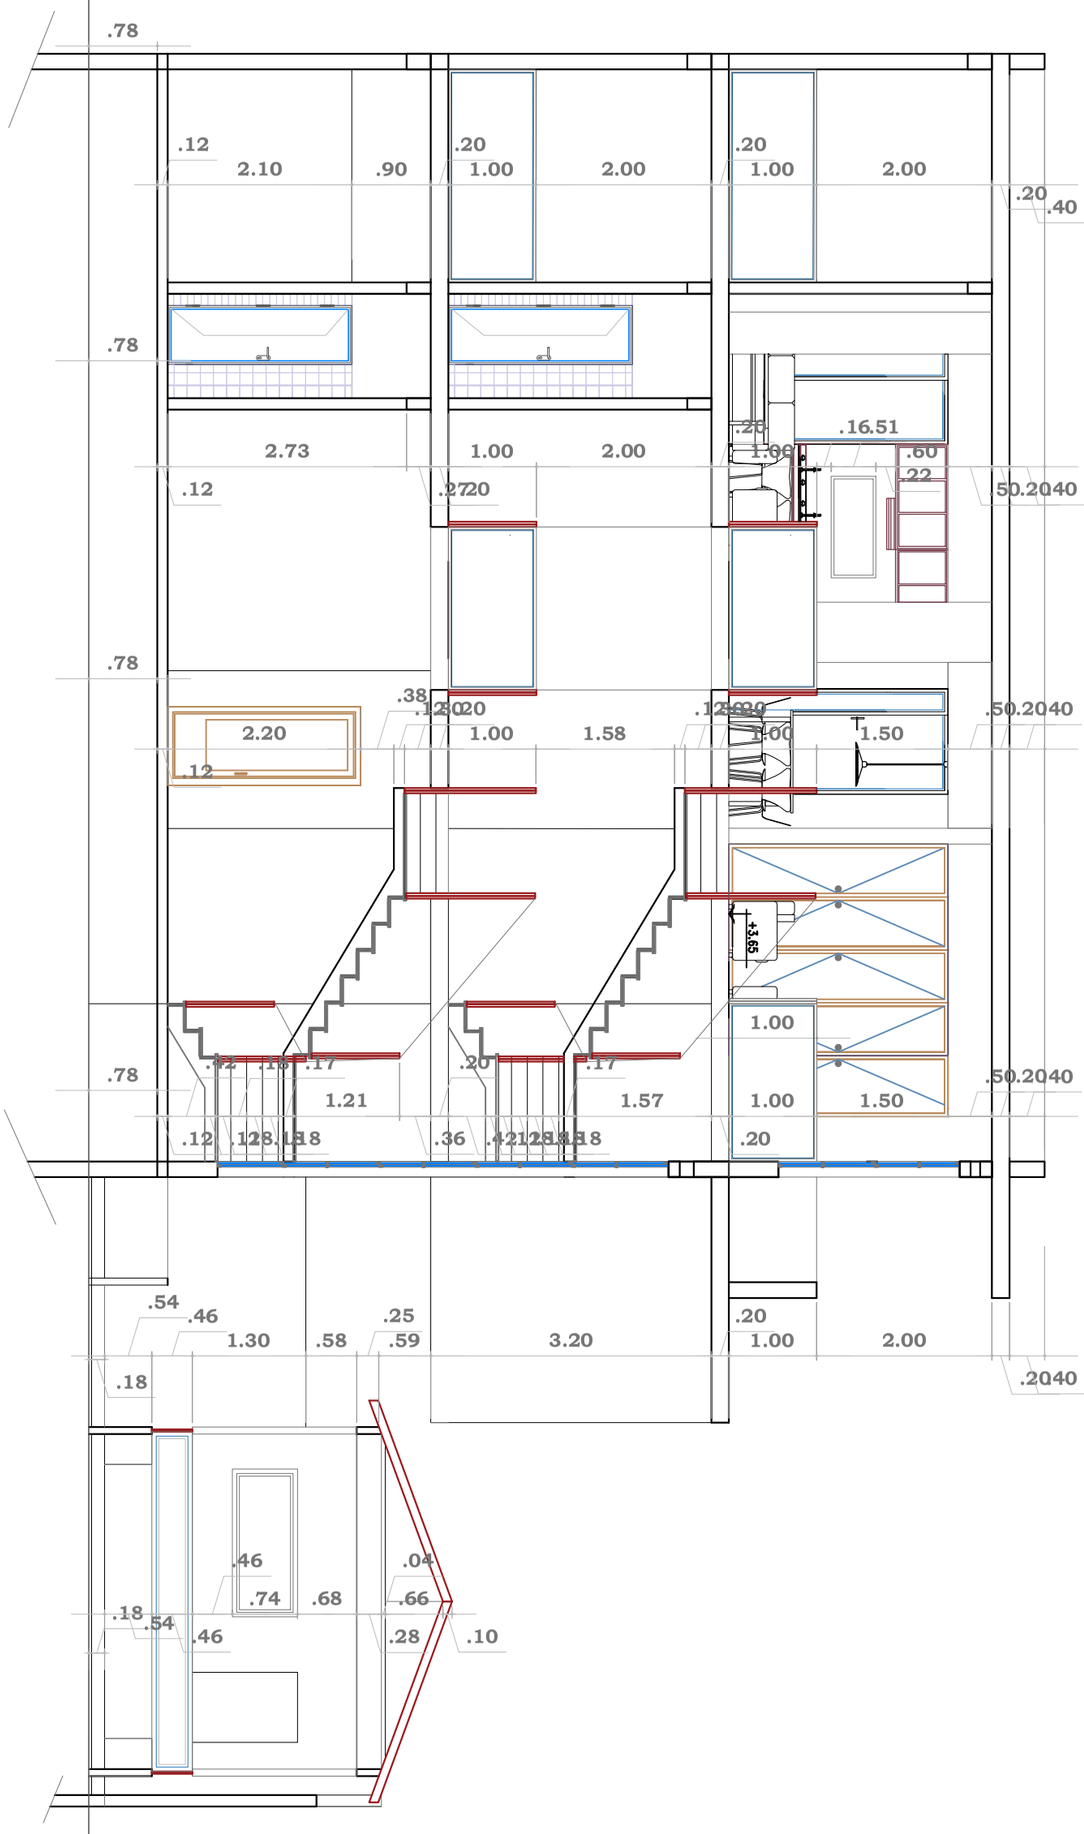

.78
.12
2.10
.90
.20
1.00
2.00
.20
1.00
2.00
.20
.40
.78
2.73
1.00
2.00
.16.51
.60
.22
.12
.50.2040
.78
.38
2.20
.12
1.00
1.58
1.00
1.50
.50.2040
+3.65
1.00
.78
1.21
1.57
1.00
1.50
.50.2040
.12
.36
.20
.54
.46
1.30
.58
.25
.59
3.20
.20
1.00
2.00
.18
.2040
.46
.74
.68
.04
.66
.18
.54
.46
.28
.10

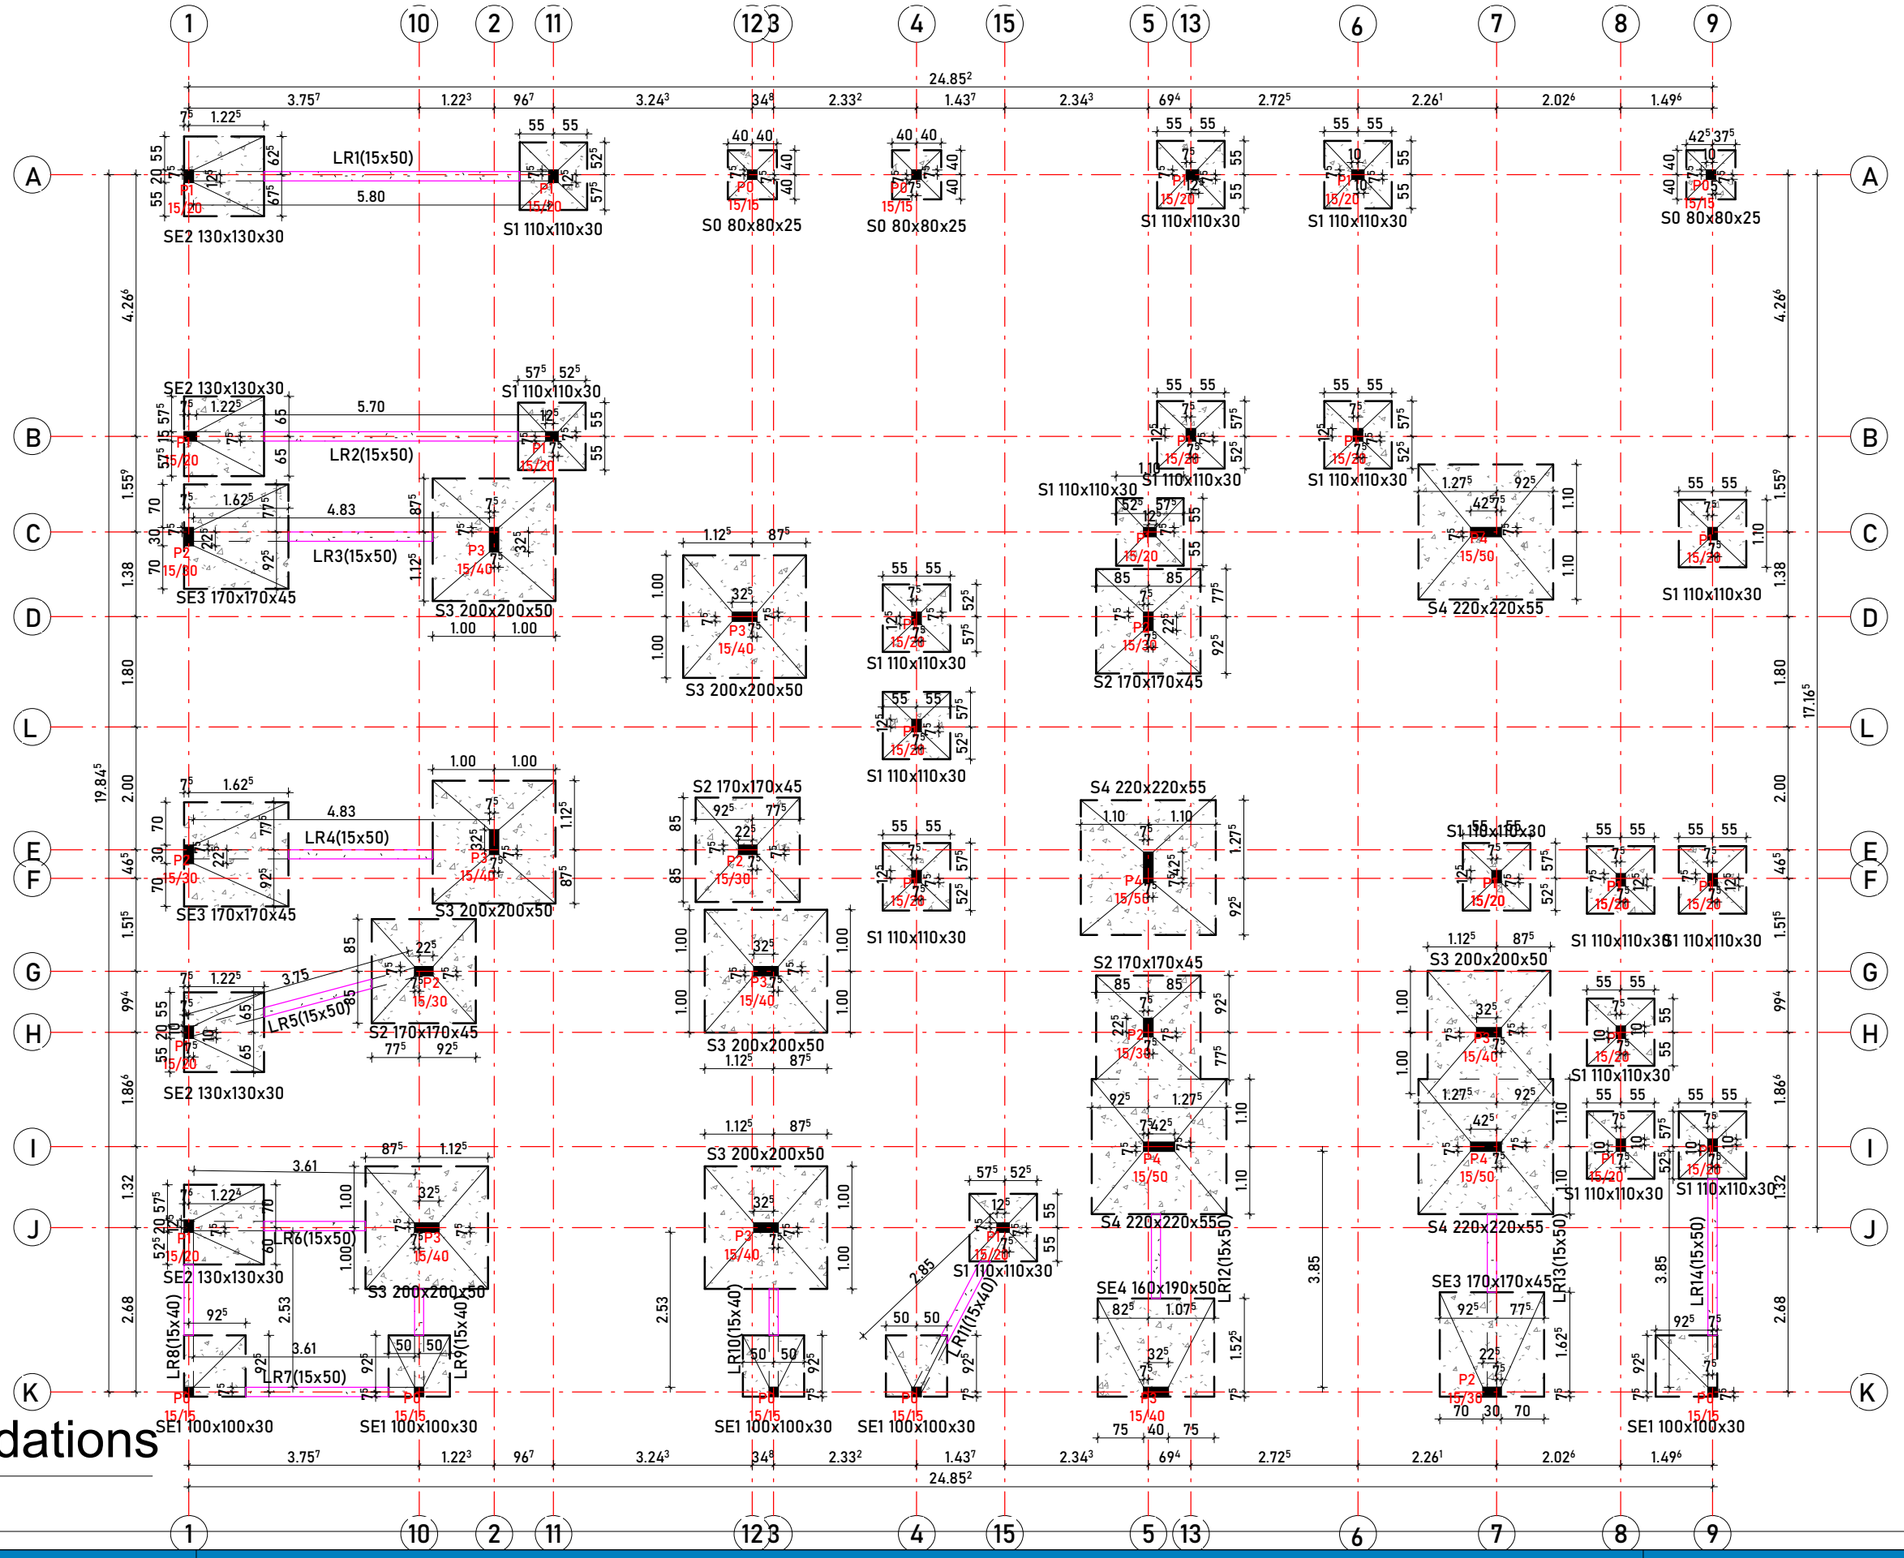

01 Fondations

1 : 100


Auteur: Moussa CISSÉ	MOUHAMADOU M.	PLAN D'IMPLANTATIONS DES SEMELLES
Vérifié par: Adja Ami MBOW	PROJET DE CONSTRUCTION D'UNE VILLA REZ DE CHAUSSEE+1ETAGE+TERRASSE ACCESSIBLE TOUBA / DIOURBEL	Phase: APD Date 10/03/2026 Echelle 1 : 100

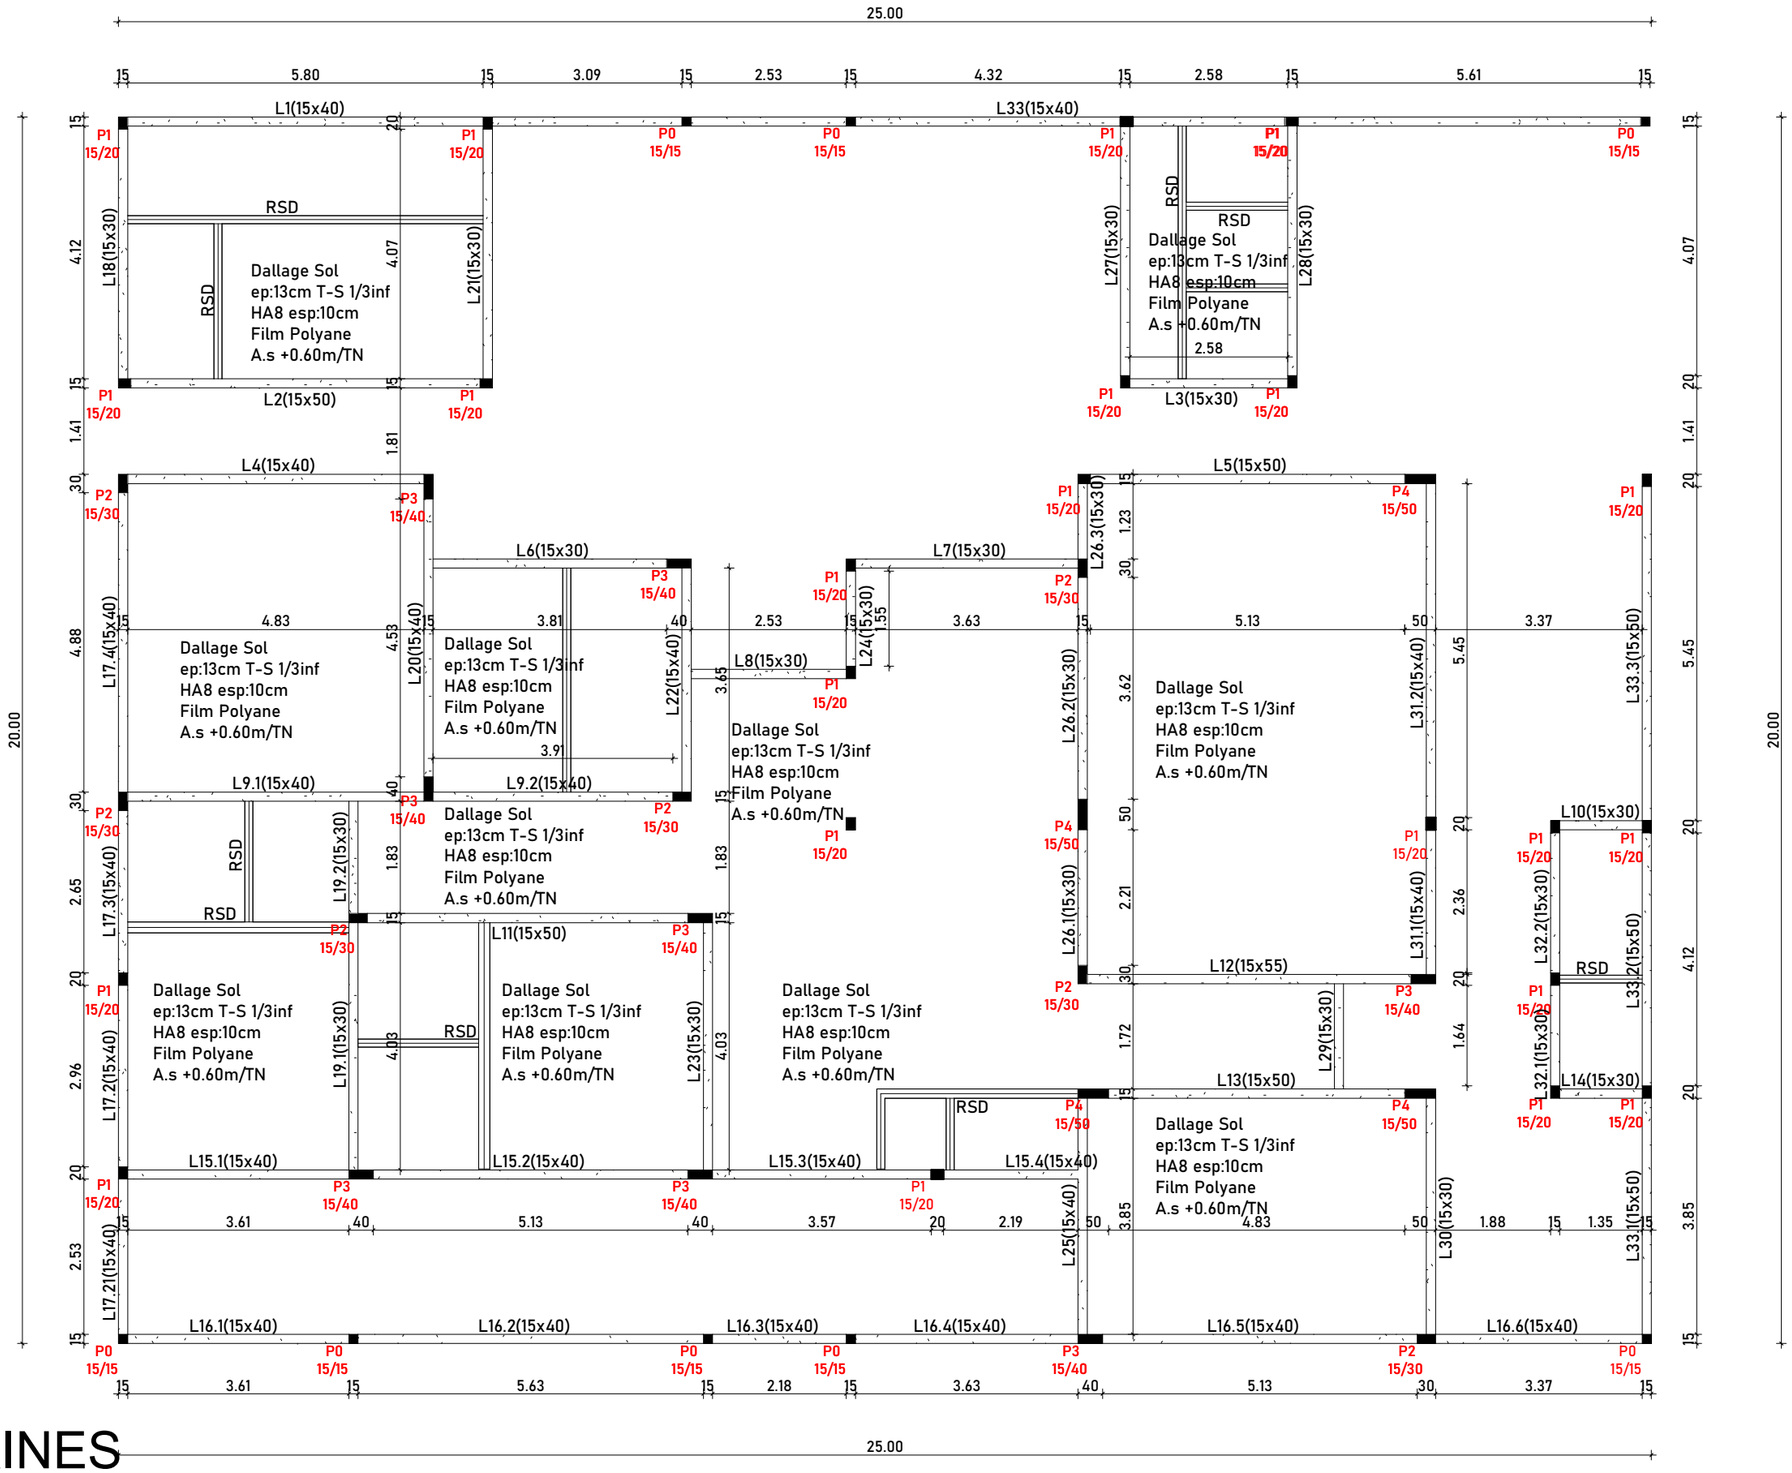

02 LONGRINES

1 : 100


Auteur: Moussa CISSÉ	MOUHAMADOU M.	COFFRAGE LONGRINES
Vérifié par: Adja Ami MBOW	PROJET DE CONSTRUCTION D'UNE VILLA REZ DE CHAUSSEE+1ETAGE+TERRASSE ACCESSIBLE TOUBA / DIOURBEL	Phase: APD Date 10/03/2026 Echelle 1 : 100

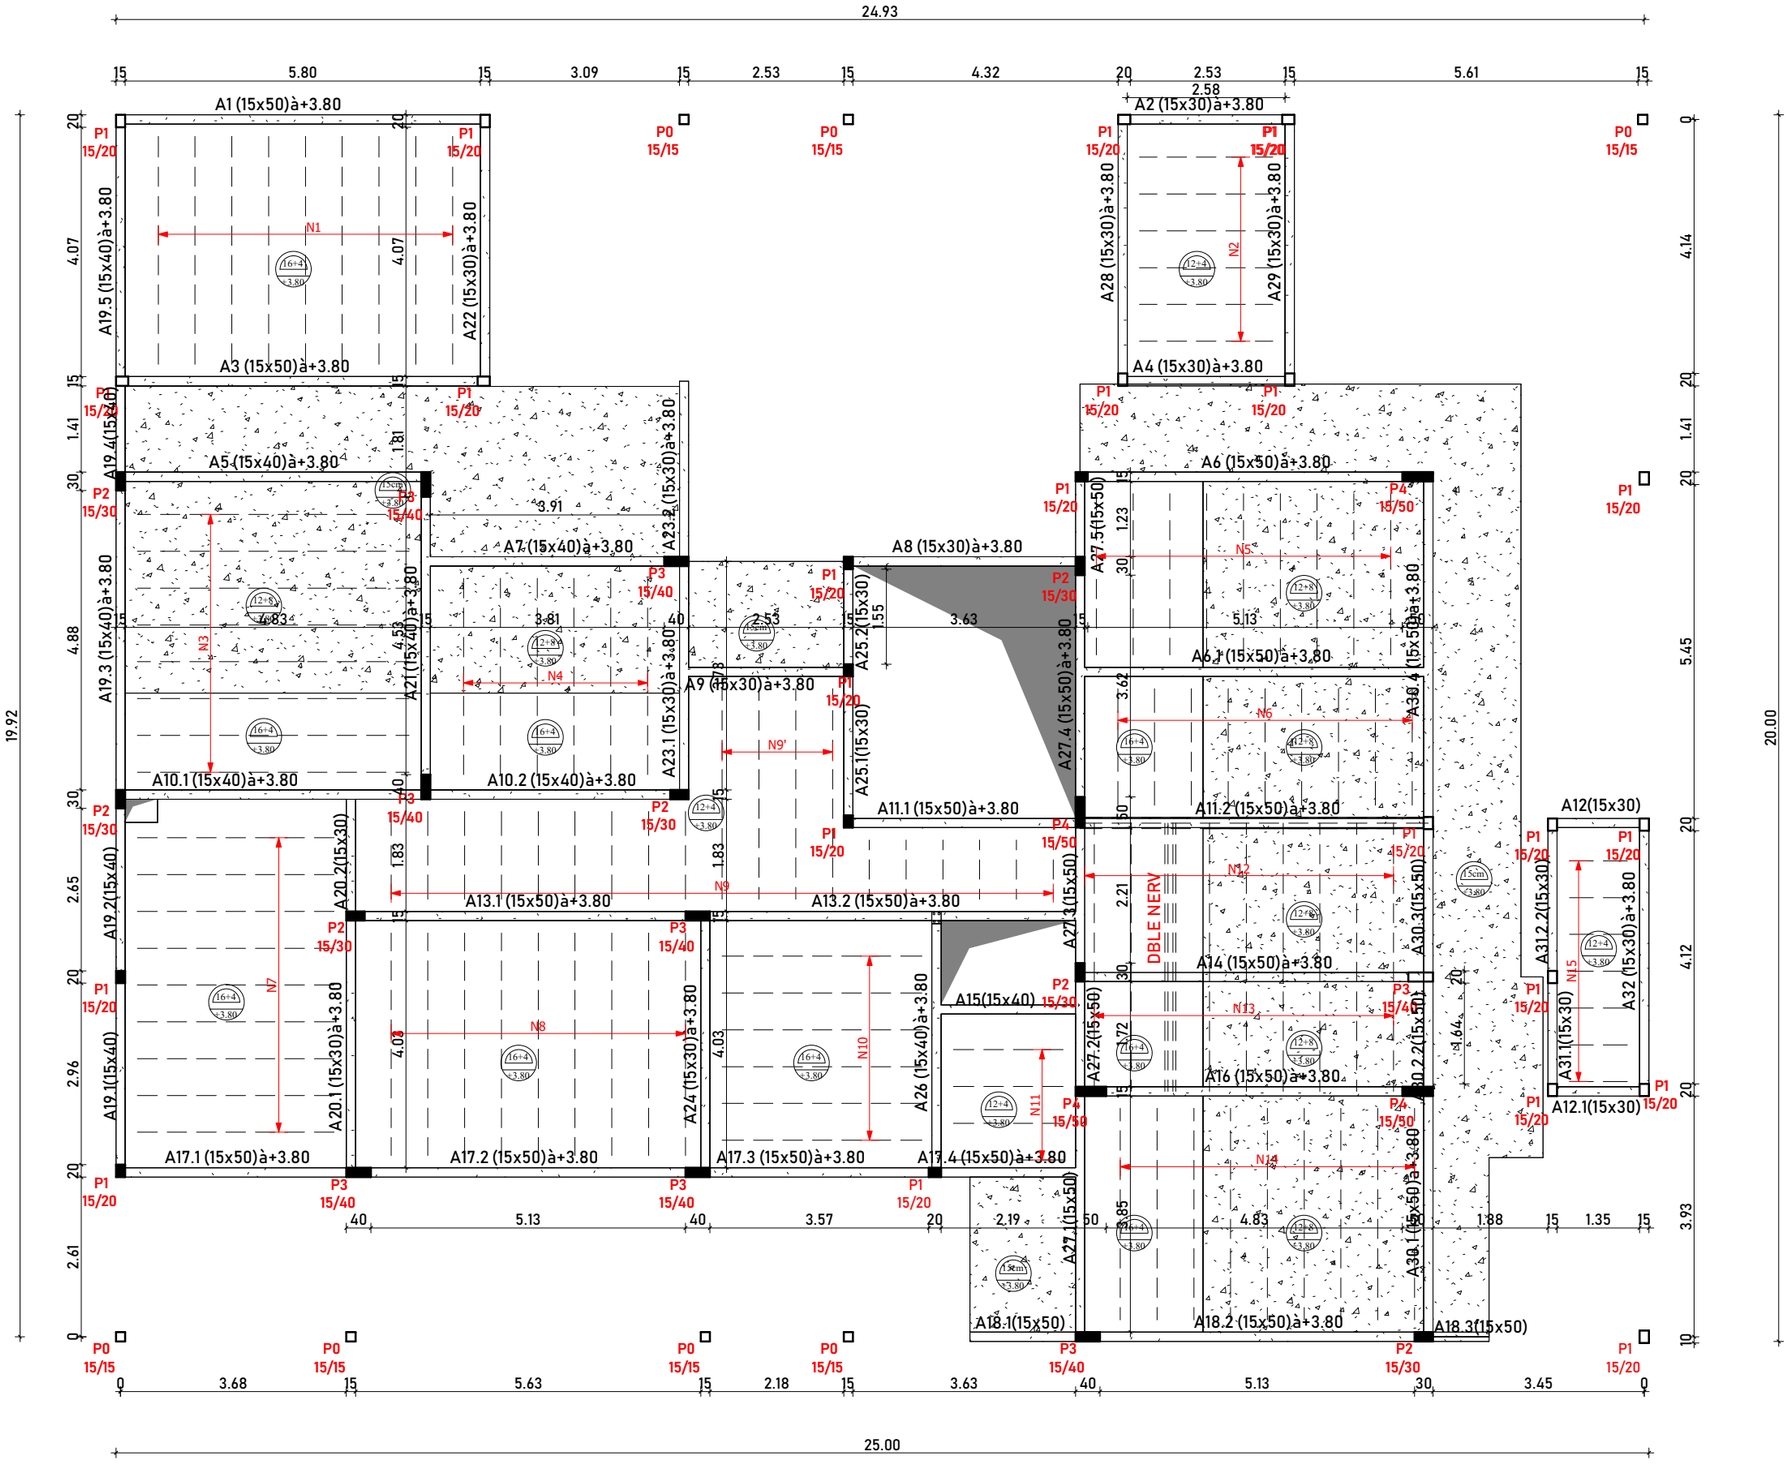

1 03 PH RDC

1 : 100


Auteur: Moussa CISSÉ	MOUHAMADOU M.	PLAN DE COFFRAGE PH RDC
Vérifié par: Adja Ami MBOW	PROJET DE CONSTRUCTION D'UNE VILLA REZ DE CHAUSSEE+1ETAGE+TERRASSE ACCESSIBLE TOUBA / DIOURBEL	Phase: APD Date 10/03/2026 Echelle 1 : 100

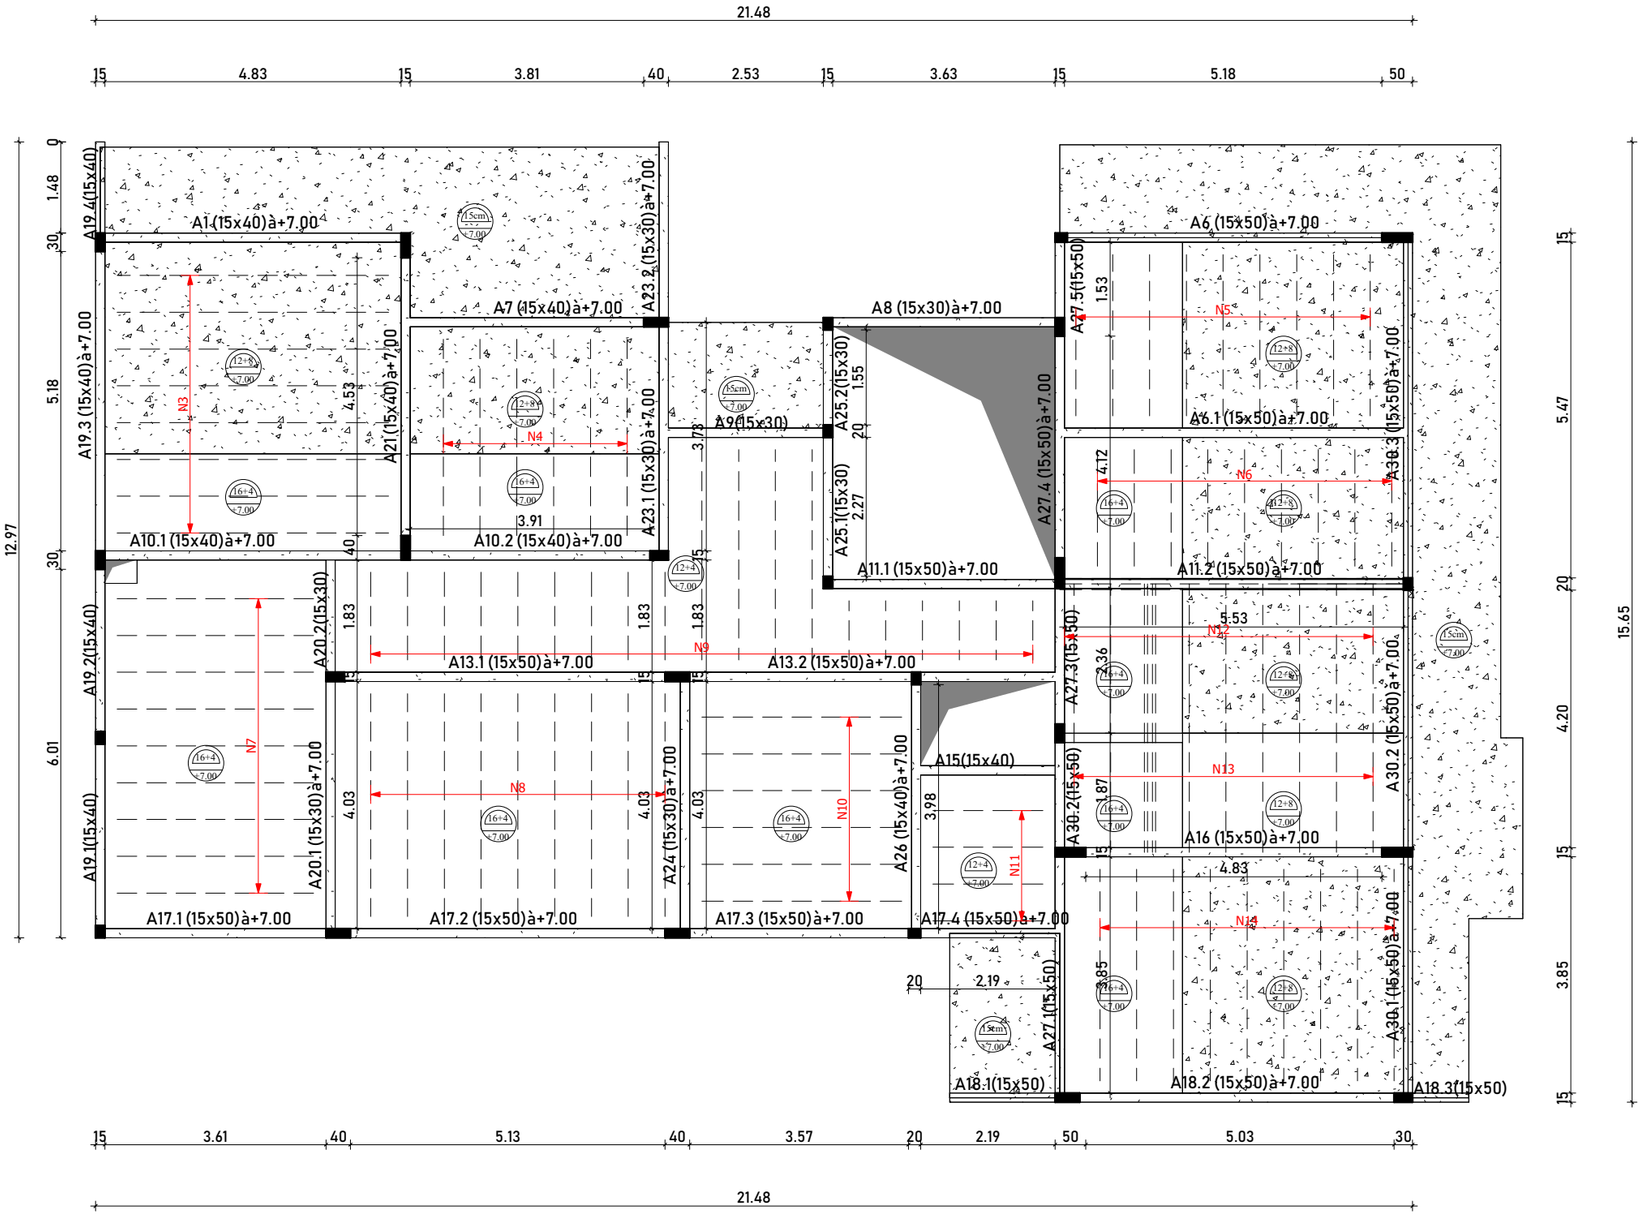

1 04 PH ETAGE

1 : 100

Auteur: Moussa CISSÉ	MOUHAMADOU M.	PLAN DE COFFRAGE PH ETAGE
	PROJET DE CONSTRUCTION D'UNE VILLA REZ DE CHAUSSEE+1ETAGE+TERRASSE ACCESSIBLE	Phase: APD
Vérifié par: Adja Ami MBOW	TOUBA / DIOURBEL	Date 10/03/2026
		Echelle 1 : 100

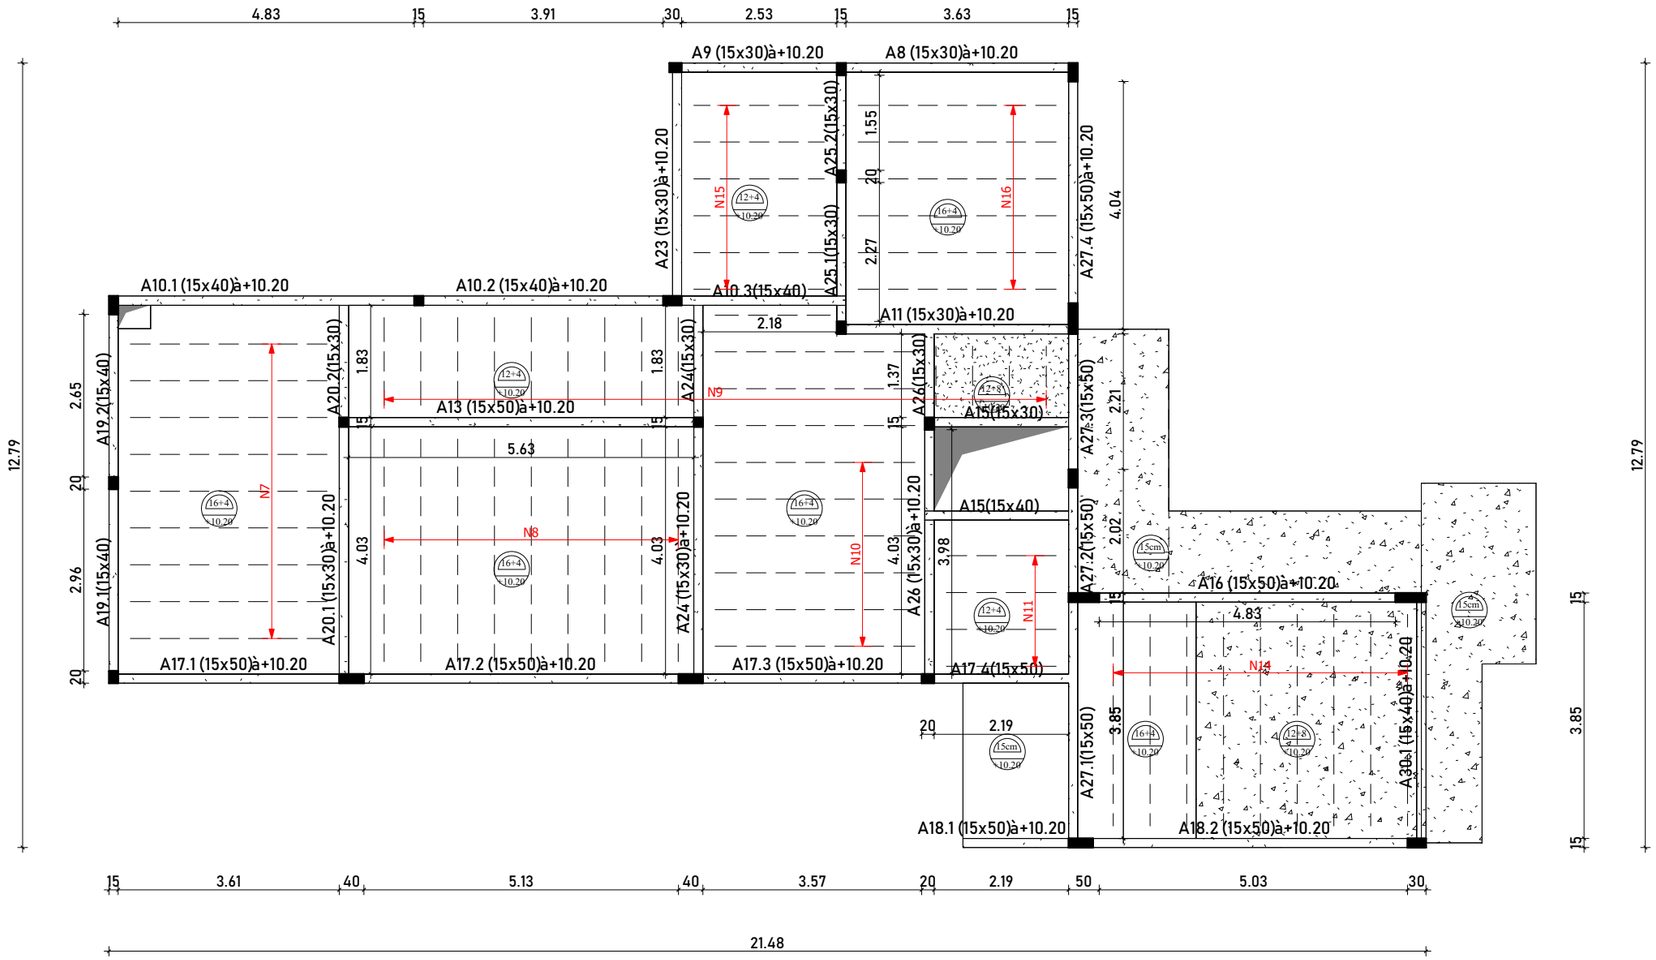



1 05 PH TERRASSE

1 : 100

Auteur: Moussa CISSÉ	MOUHAMADOU M.	PLAN DE COFFRAGE PH TERRASSE
Vérifié par: Adja Ami MBOW	PROJET DE CONSTRUCTION D'UNE VILLA REZ DE CHAUSSEE+1ETAGE+TERRASSE ACCESSIBLE TOUBA / DIOURBEL	Phase: APD Date 10/03/2026 Echelle 1 : 100


Pos.	Armature		Code	Forme	Acier
1	4HA10	l=3.64	00	3.64	HA 500
2	22HA6	l=48	31	9 8	HA 500

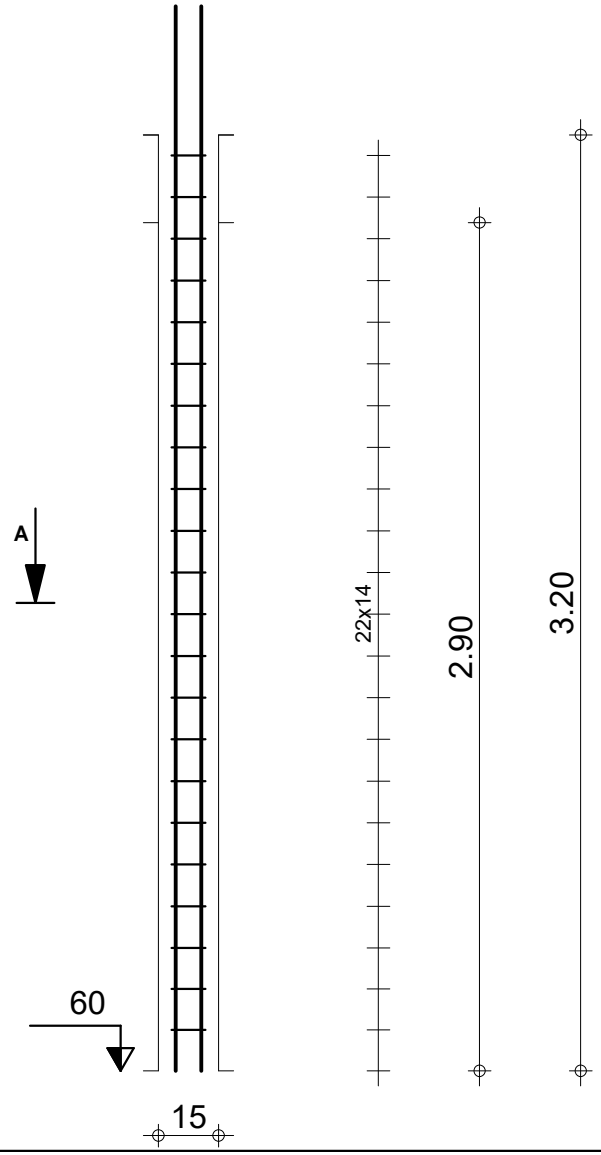

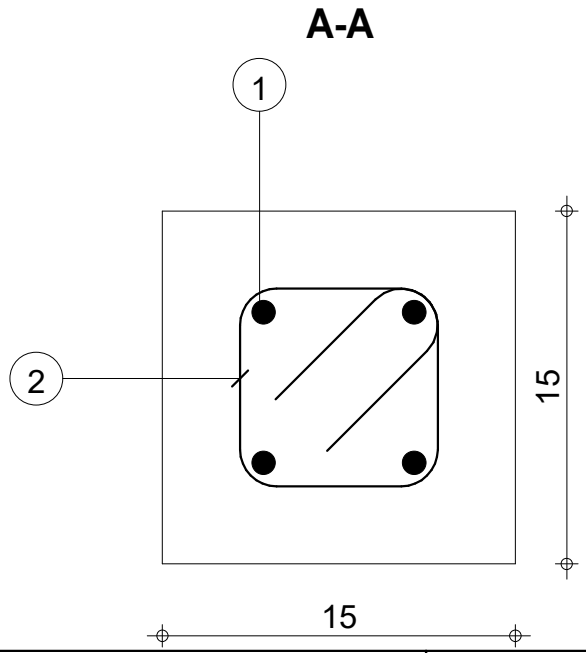


Ing.Moussa CISSÉ Dakar-Sénégal	Tél. 77 231 96 53 Fax		Acier HA 500 = 8.98 kg
Classe d'exposition : non agressif	Diamètre max. du granulat : 20mm	Béton : BETON = 0.0652 m3	Acier HA 500 = 2.33 kg
FERRAILLAGE DES POTEAUX	**P0** Nombre 1	Surface du coffrage = 1.74 m2	Enrobage 3 cm
PROJET R+1 TOUBA	**Section 15x15**	Densité = 173.3 kg/ m3	Echelle pour la vue 5.31cm/m x 3.88cm/m Echelle pour la section 31.2cm/m

Pos.	Armature		Code	Forme	Acier
1	4HA10	l=3.64	00	3.64	HA 500
6	22HA6	l=58	31	9 14 8	HA 500

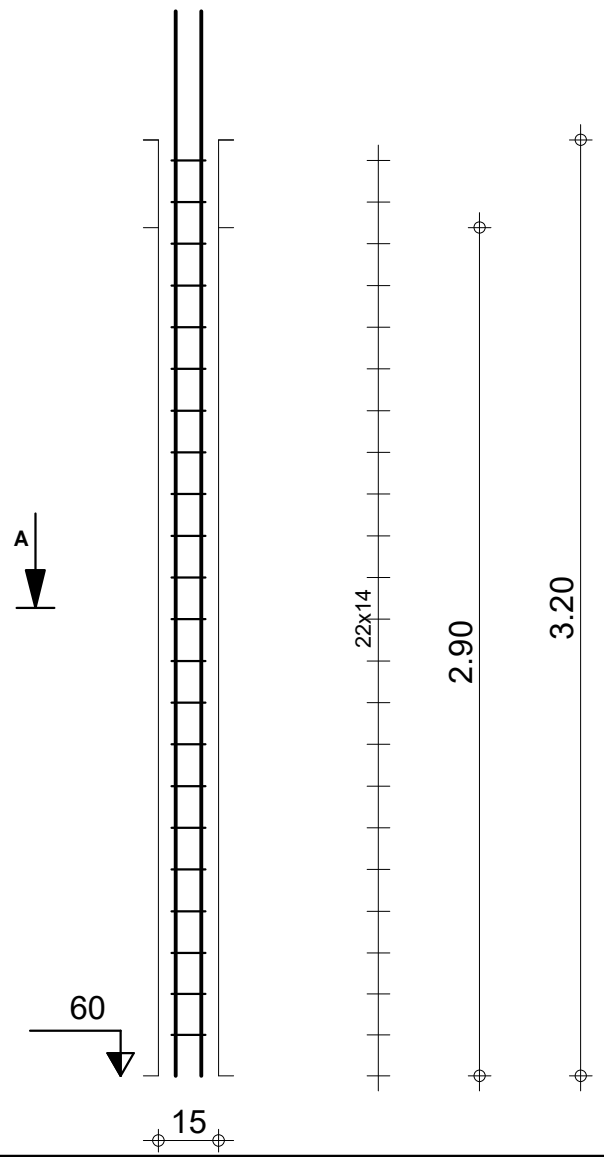

A-A

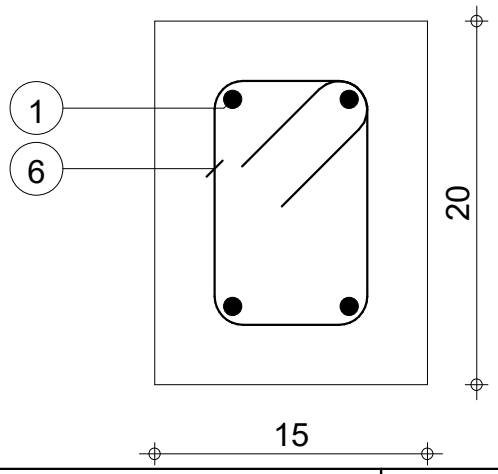

Ing.Moussa CISSÉ	Dakar-Sénégal		Tél. 77 231 96 53	Fax	
Classe d'exposition : non agressif		Diamètre max. du granulat : 20mm		Consistance : S1	

Béton : BETON = 0.087 m3	Acier HA 500 = 8.98 kg
	Acier HA 500 = 2.82 kg
Surface du coffrage = 2.03 m2	Enrobage 3 cm
Densité = 135.6 kg/ m3	Echelle pour la vue 5.31cm/m x 3.88cm/m
	Echelle pour la section 24.1cm/m


FERRAILLAGE DES POTEAUX


PROJET R+1 TOUBA

P1 **Nombre 1**

Section 15x20


Pos.	Armature		Code	Forme	Acier
1	6HA10	l=3.64	00	3.64	HA 500
4	22HA6	l=21	00	5 9	HA 500
5	22HA6	l=78	31	9 24 8	HA 500

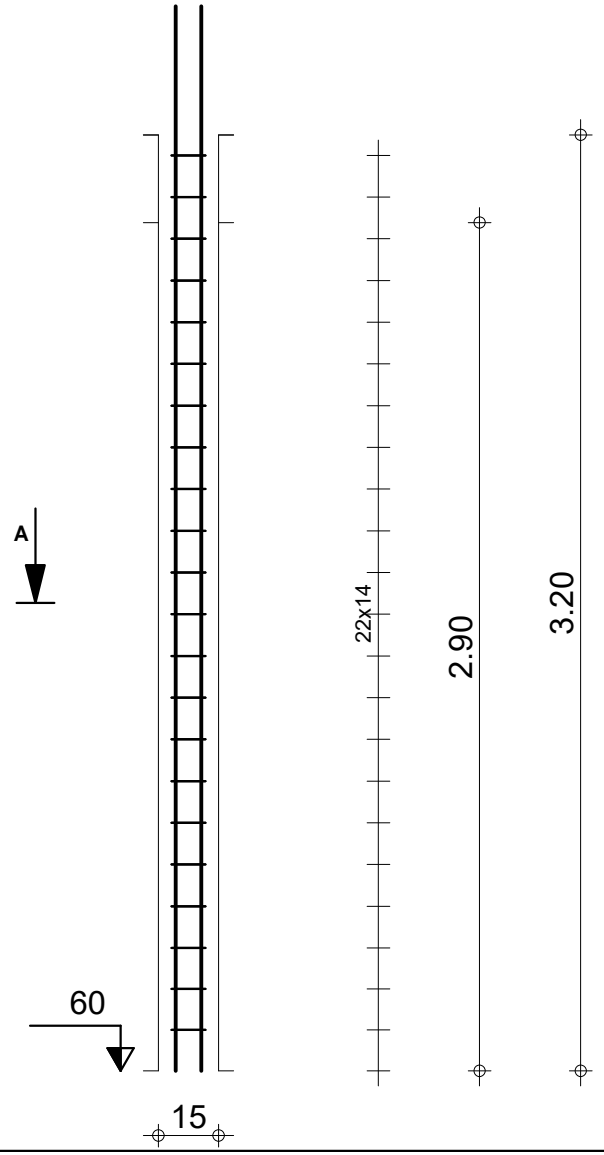

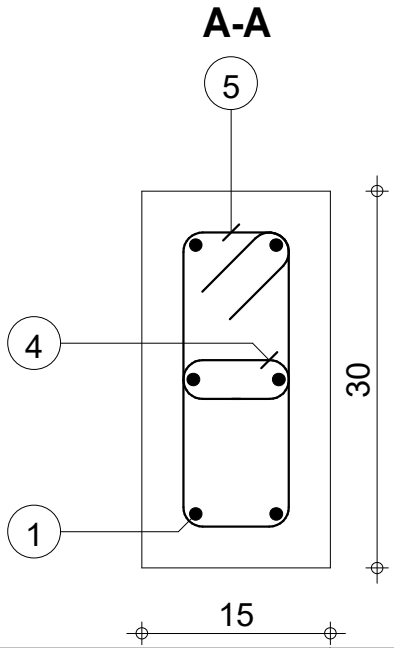


Ing.Moussa CISSÉ Dakar-Sénégal	Tél. 77 231 96 53 Fax		Acier HA 500 = 13.5 kg
Classe d'exposition : non agressif	Diamètre max. du granulat : 20mm	Béton : BETON = 0.13 m3	Acier HA 500 = 4.83 kg
FERRAILLAGE DES POTEAUX	**P2** **Nombre 1**	Surface du coffrage = 2.61 m2	Enrobage 3 cm
PROJET R+1 TOUBA	**Section 15x30**	Densité = 140.8 kg/ m3	Echelle pour la vue 5.31cm/m x 3.88cm/m Echelle pour la section 16.7cm/m

Pos.	Armature		Code	Forme	Acier
1	6HA10	l=3.64	00	3.64	HA 500
3	22HA6	l=98	31	9 / 34 / 8	HA 500
4	22HA6	l=21	00	5 — 9	HA 500

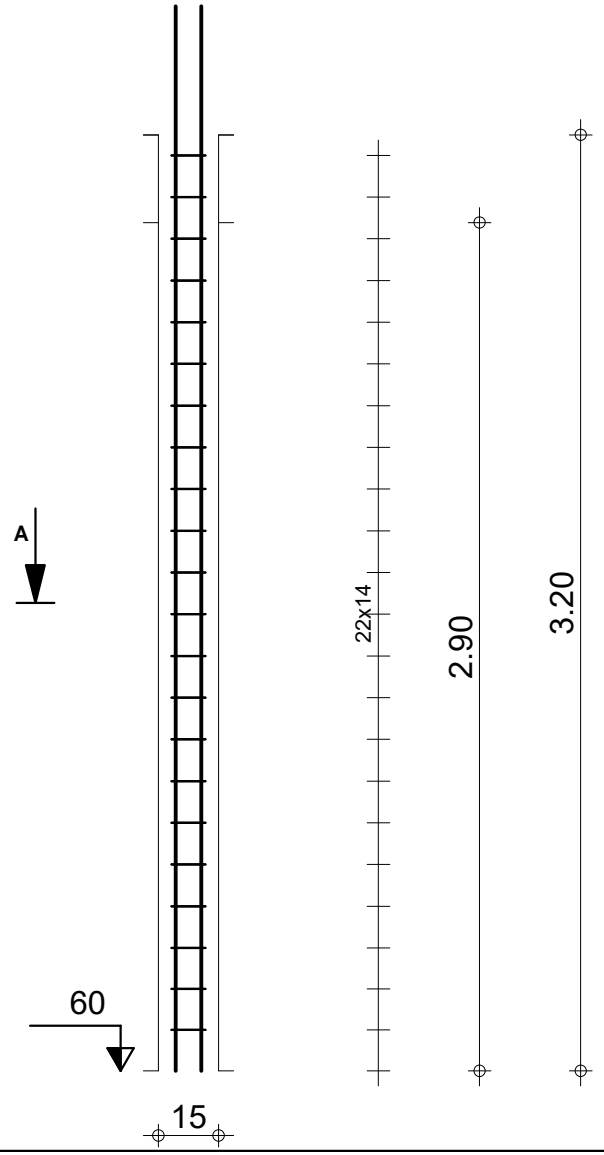

A-A

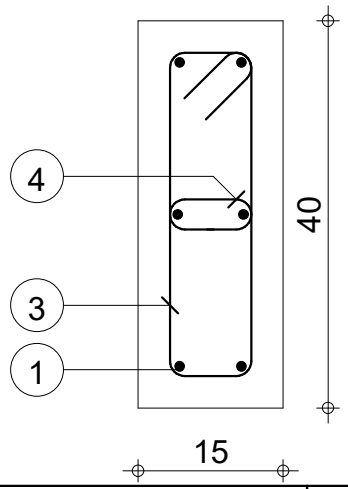

Ing.Moussa CISSÉ	Dakar-Sénégal		Tél. 77 231 96 53	Fax	
Classe d'exposition : non agressif		Diamètre max. du granulat : 20mm		Consistance : S1	

Béton : BETON = 0.174 m3	Acier HA 500 = 13.5 kg
	Acier HA 500 = 5.8 kg
Surface du coffrage = 3.19 m2	Enrobage 3 cm
Densité = 110.9 kg/ m3	Echelle pour la vue 5.31cm/m x 3.88cm/m
	Echelle pour la section 12.8cm/m

FERRAILLAGE DES POTEAUX


PROJET R+1 TOUBA

P3


Nombre 1

Section 15x40

Pos.	Armature		Code	Forme	Acier
1	2HA10	l=3.64	00	3.64	HA 500
4	20HA6	l=21	00	5 9	HA 500
7	4HA12	l=3.73	00	3.73	HA 500
8	20HA6	l=1.18	31	9 44 8	HA 500

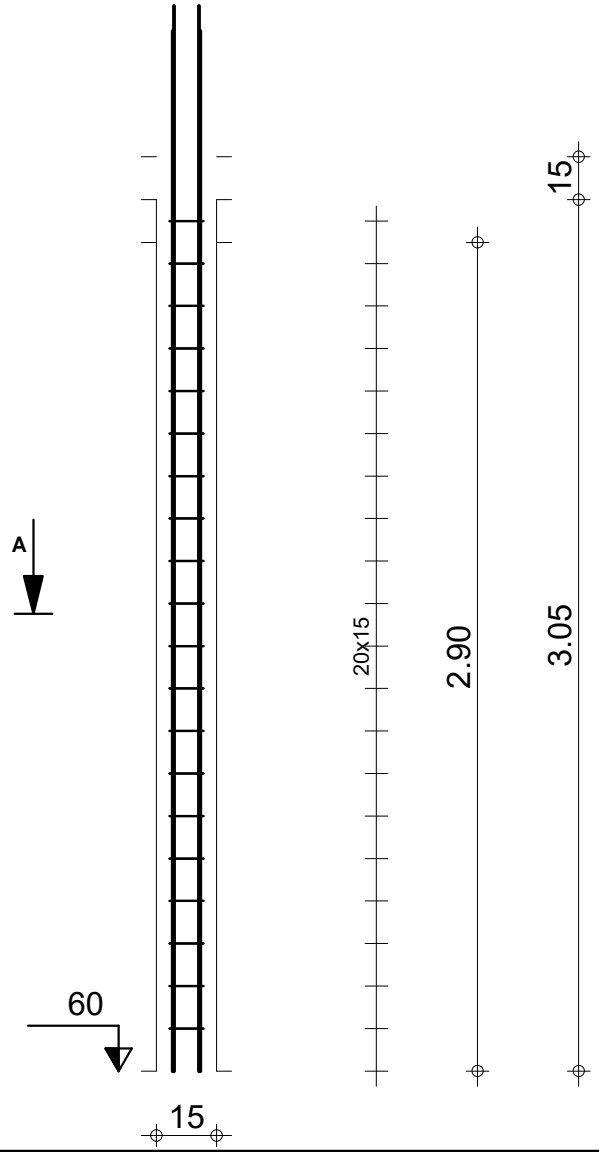

A-A

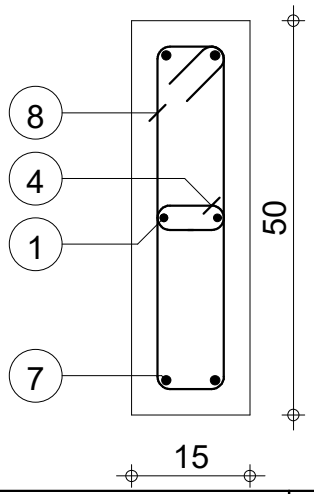

Ing.Moussa CISSÉ	Dakar-Sénégal	Tél. 77 231 96 53 Fax	
Classe d'exposition : non agressif	Diamètre max. du granulat : 20mm	Consistance : S1	Béton : BETON = 0.217 m3
			Surface du coffrage = 3.77 m2
			Densité = 110.1 kg/ m3

Acier HA 500 = 17.7 kg
Acier HA 500 = 6.16 kg
Enrobage 3 cm
Echelle pour la vue 5.31cm/m x 3.79cm/m
Echelle pour la section 10.5cm/m

FERRAILLAGE DES POTEAUX


PROJET R+1 TOUBA


P4

Nombre 1

Section 15x50


Pos.	Armature		Code	Forme	Acier
9	14HA10	l=1.34	00	6 1.00	HA 500

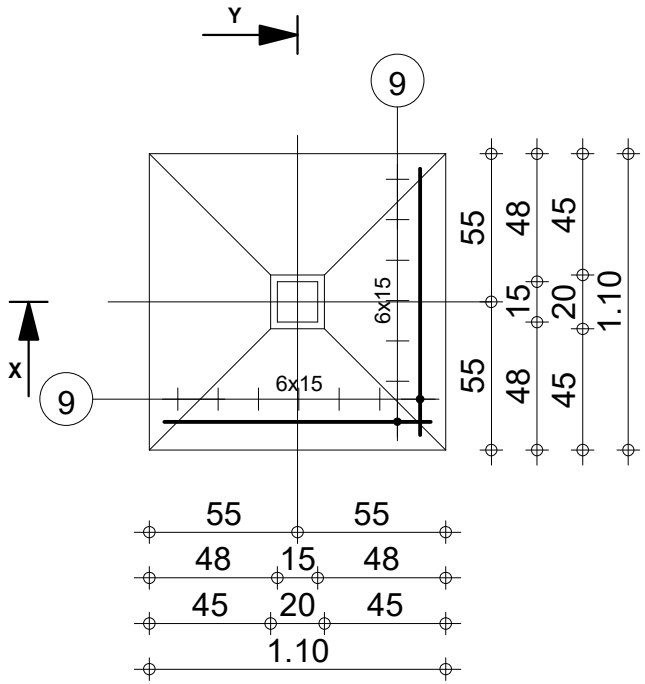


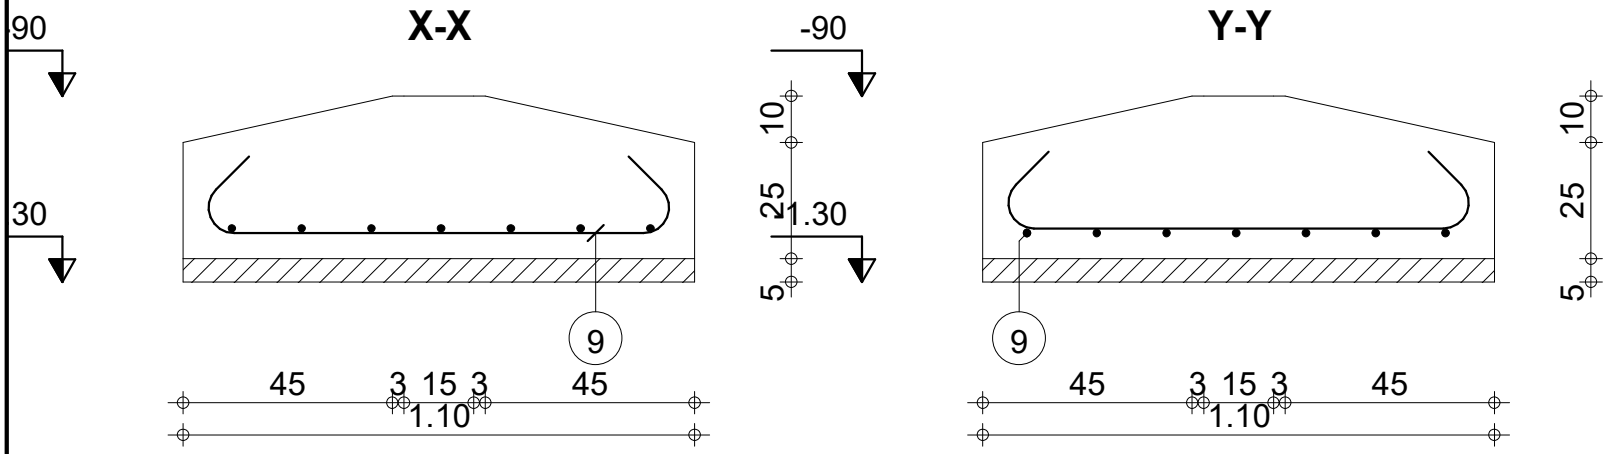

Ing.Moussa CISSÉ Dakar-Sénégal Tél. 77 231 96 53 Fax			Acier HA 500 = 11.6 kg
Fissuration préjudiciable		Béton : BETON25 = 0.37 m3	
FERRAILLAGE DES SEMELLES	**S1**	Surface du coffrage = 2.3 m2	Enrobage c1 = 5 cm, c2 = 5 cm
PROJET R+1 TOUBA	**Nombre 1**	Densité = 31.35 kg/ m3	Echelle pour la vue 3.57cm/m Echelle pour la section 6.16cm/m


Pos.	Armature		Code	Forme	Acier
11	22HA10	l=1.94	00	1.60	HA 500

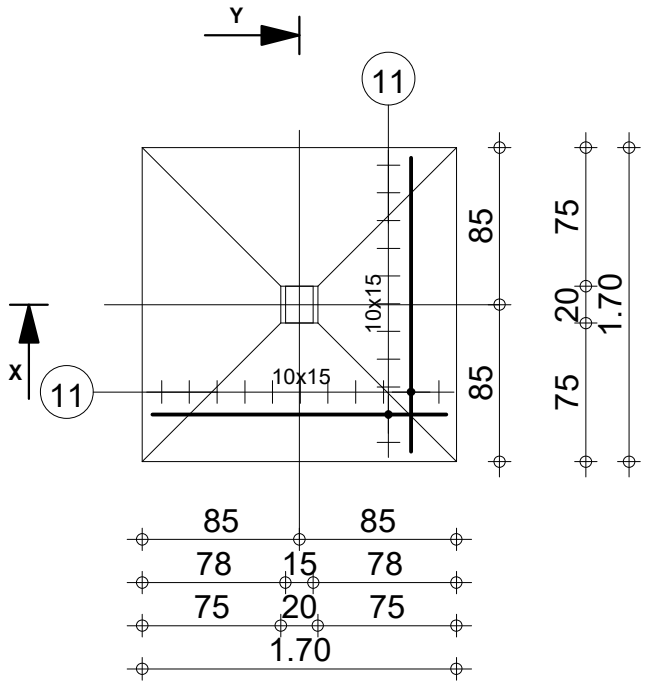


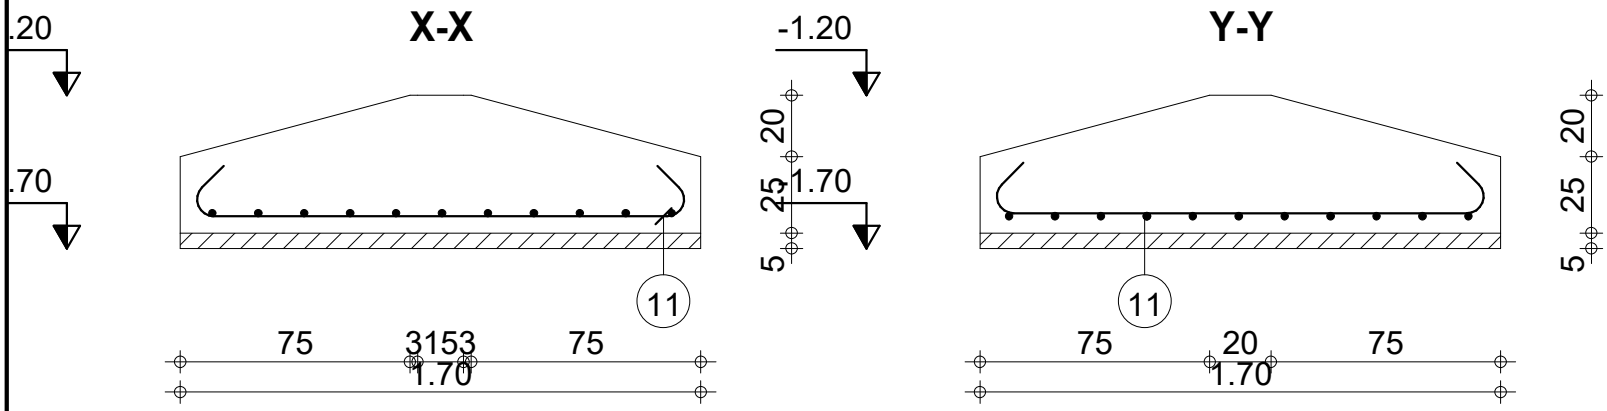

Ing.Moussa CISSÉ Dakar-Sénégal Tél. 77 231 96 53 Fax			Acier HA 500 = 26.3 kg
Fissuration préjudiciable		Béton : BETON25 = 1 m3	
FERRAILLAGE DES SEMELLES	**S2**	Surface du coffrage = 4.65 m2 Densité = 26.3 kg/ m3	Enrobage c1 = 5 cm, c2 = 5 cm
PROJET R+1 TOUBA	**Nombre 1**		Echelle pour la vue 2.45cm/m Echelle pour la section 4.06cm/m


Pos.	Armature		Code	Forme	Acier
12	26HA10	l=2.24	00	1.90	HA 500

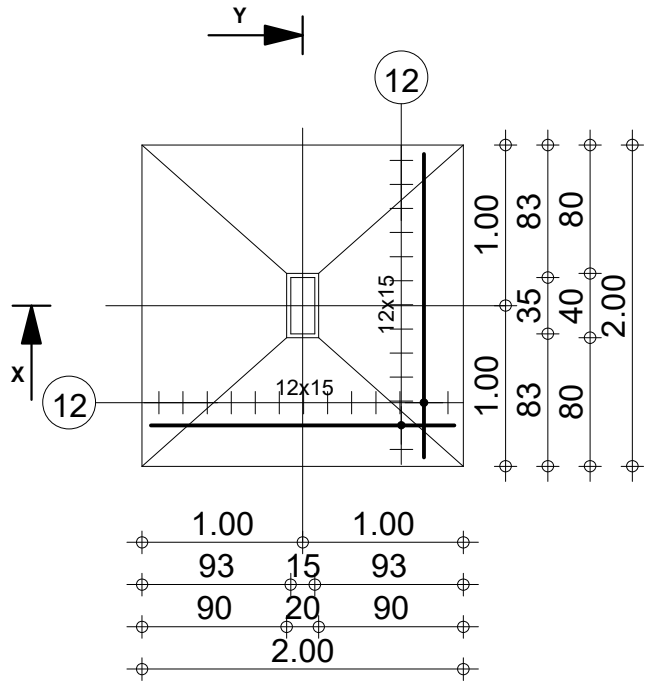


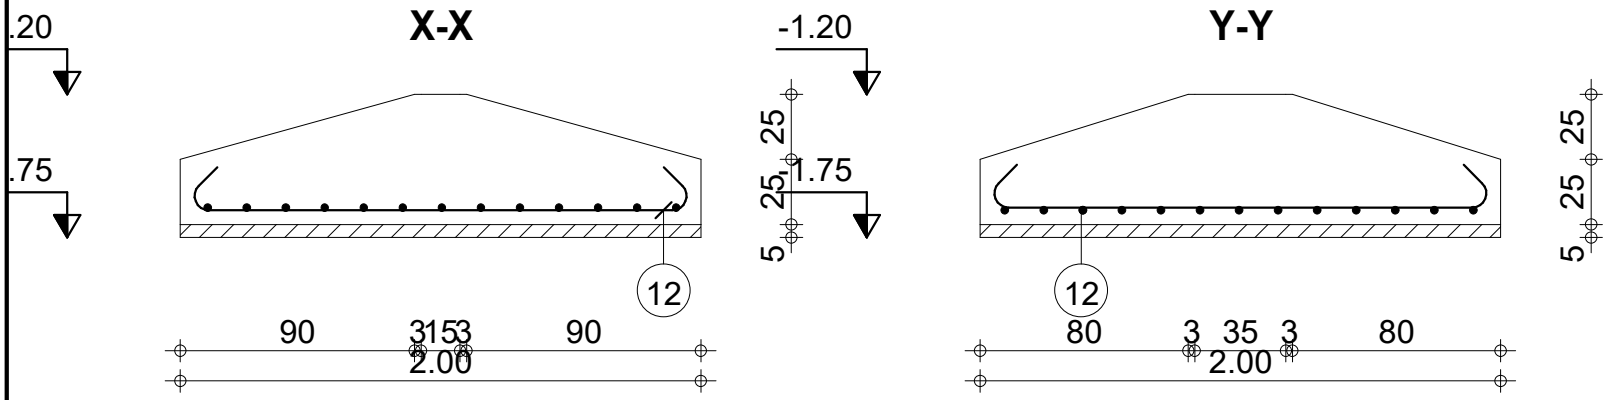


Ing.Moussa CISSÉ Dakar-Sénégal Tél. 77 231 96 53 Fax			Acier HA 500 = 35.9 kg
Fissuration préjudiciable		Béton : BETON25 = 1.52 m3	
FERRAILLAGE DES SEMELLES	**S3**	Surface du coffrage = 6.09 m2 Densité = 23.62 kg/ m3	Enrobage c1 = 5 cm, c2 = 5 cm
PROJET R+1 TOUBA	**Nombre 1**		Echelle pour la vue 2.13cm/m Echelle pour la section 3.45cm/m

Pos.	Armature		Code	Forme	Acier
13	32HA10	l=2.44	00	6 2.10	HA 500

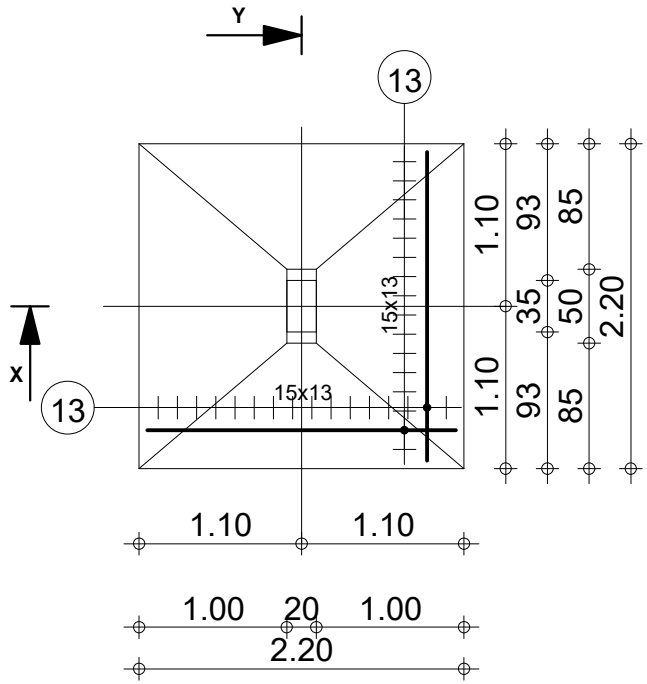


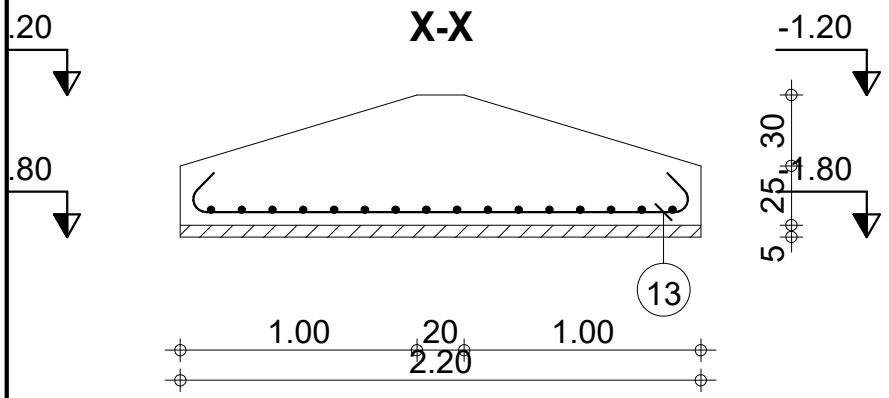


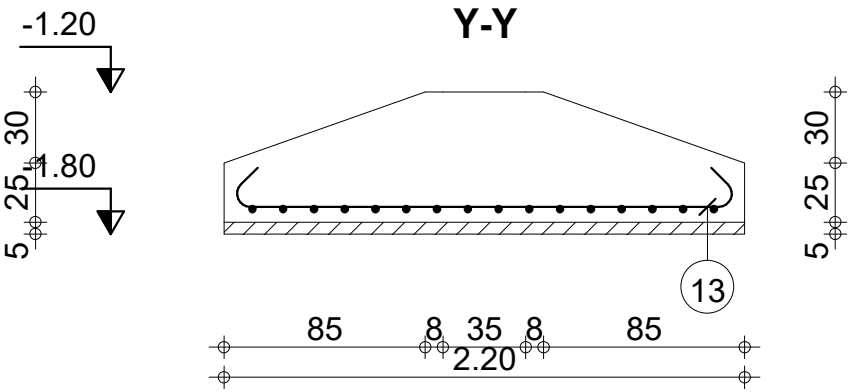


Ing.Moussa CISSÉ Dakar-Sénégal Tél. 77 231 96 53 Fax			Acier HA 500 = 48.1 kg
Fissuration préjudiciable		Béton : BETON25 = 1.98 m3	
FERRAILLAGE DES SEMELLES	**S4**	Surface du coffrage = 7.18 m2 Densité = 24.29 kg/ m3	Enrobage c1 = 5 cm, c2 = 5 cm
PROJET R+1 TOUBA	**Nombre 1**		Echelle pour la vue 1.96cm/m Echelle pour la section 3.14cm/m

Pos.	Armature	Code	Forme	Acier
10	8HA10 l=94	00	6 60	HA 500

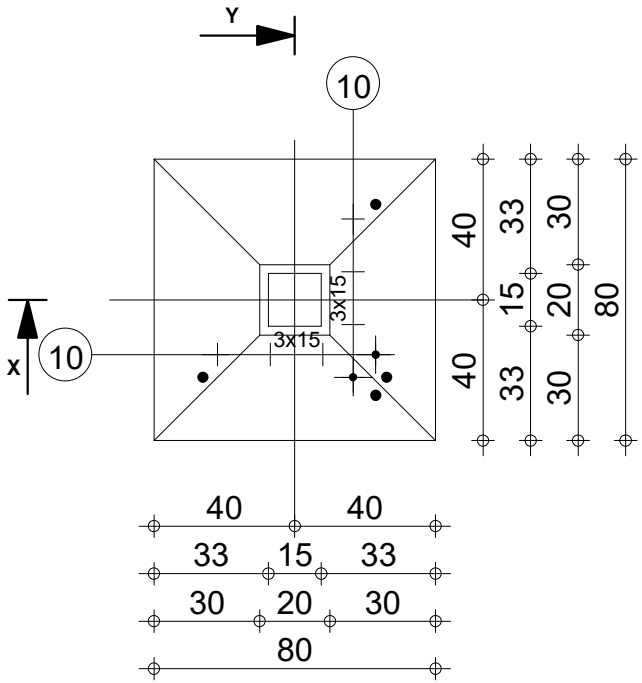

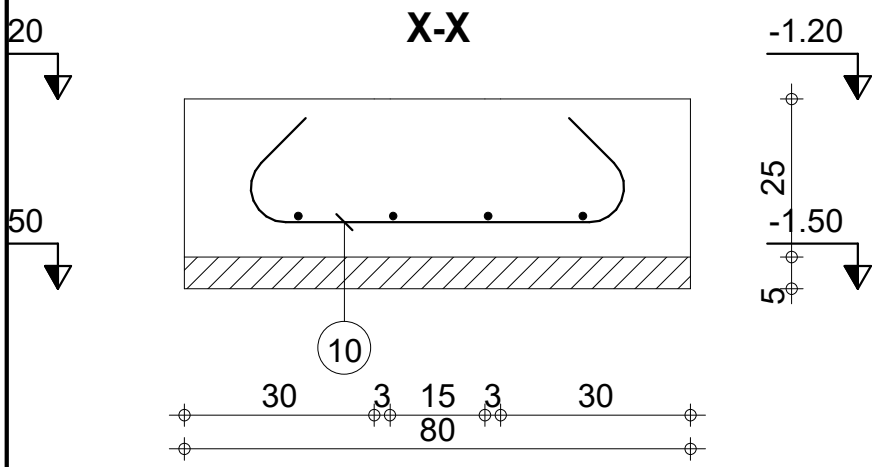

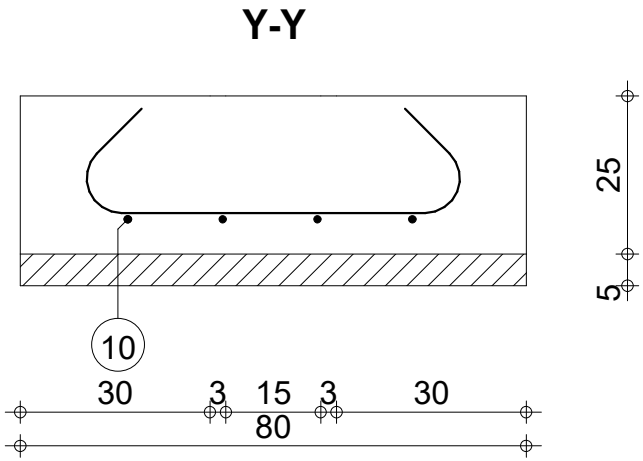

Ing.Moussa CISSÉ Dakar-Sénégal Tél. 77 231 96 53 Fax

Fissuration préjudiciable

Acier HA 500 = 4.63 kg

FERRAILLAGE DES SEMELLES **S0** **Nombre 1**

Surface du coffrage = 1.4 m2

Densité = 28.94 kg/ m3

Enrobage c1 = 5 cm, c2 = 5 cm

PROJET R+1 TOUBA

Echelle pour la vue 4.66cm/m

Echelle pour la section 8.38cm/m